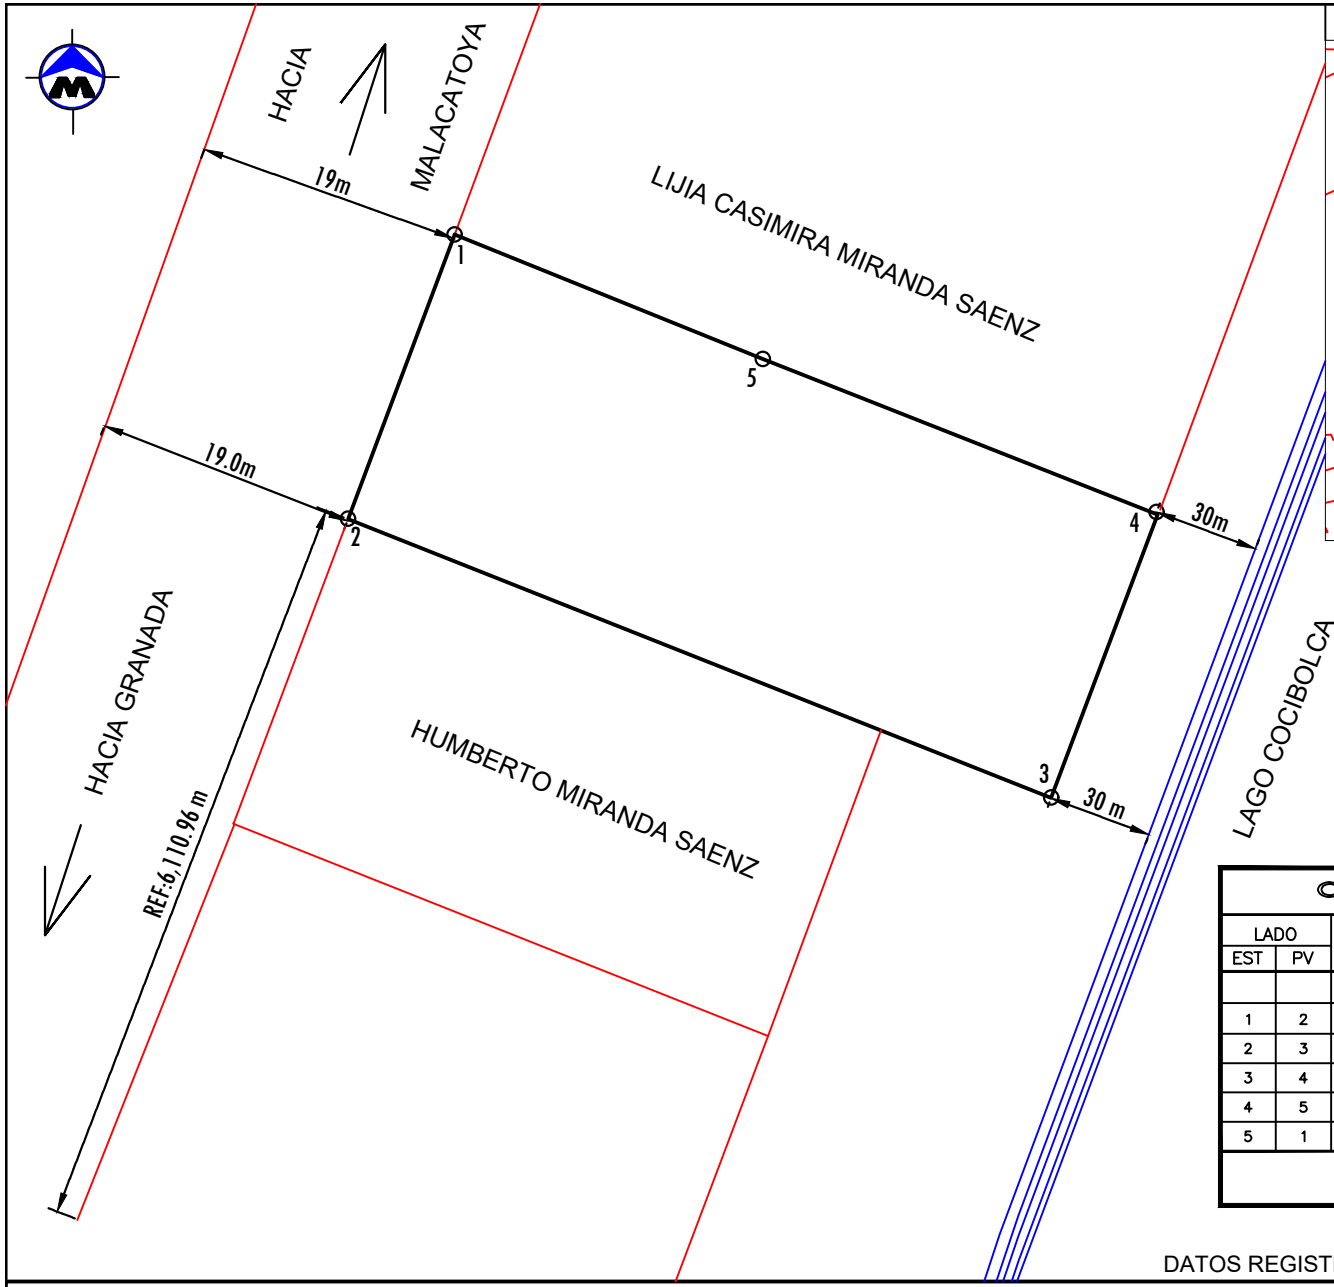

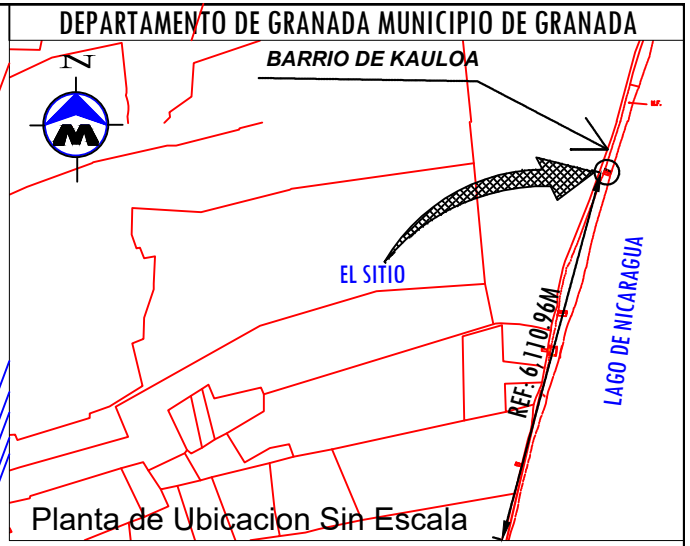

Numero Catastral: 3052-3-14-000-(00100)MF

COORDENADAS NO VINCULADAS A LA RED GEODESICA DE NICARAGUA

CUADRO DE CONSTRUCCION

LADO EST	LADO PV	RUMBO	DISTANCIA	V	COORDENADAS Y	COORDENADAS X
				1	1,326,673.7600	615,845.4800
1	2	S 20°31'46.37" W	10.12	2	1,326,664.2800	615,841.9300
2	3	S 68°21'47.81" E	25.20	3	1,326,654.9900	615,865.3500
3	4	N 20°36'33.26" E	10.09	4	1,326,664.4300	615,868.9000
4	5	N 68°29'58.95" W	14.13	5	1,326,669.6100	615,855.7500
5	1	N 67°59'48.77" W	11.08	1	1,326,673.7600	615,845.4800

SUPERFICIE = 253.91 m2

DATOS REGISTRALES FINCA: 35,389 TOMO: 559 FOLIO: 286 ASIENTO:1

Objeto Lev: Venta Total	Numero Catastral: 3052-3-14-000-(00100)MF	Fecha: 27 de agosto del 2024
Enajenante: Humberto Miranda Saenz Cédula: 201-230743-0003L	Ubicacion: Del Instituto Pedro Arauz Palacios 6,110.96m al Noreste, Barrio de Kauloa, Municipio de Granada. Depto de Granada.	Ejecuta: Ing..Bosco Javier Morgan Lic. Catastral: BMM100426 Cel: 8883-7568 Email: ingmorgan73@gmail.com www.morganconstrucciones.com
Adquiriente: George Pietras Pasaporte # P056355QS	Area: 253.91 m² = 360.15 vrs² — Escala: 1 / 250	FIRMA: