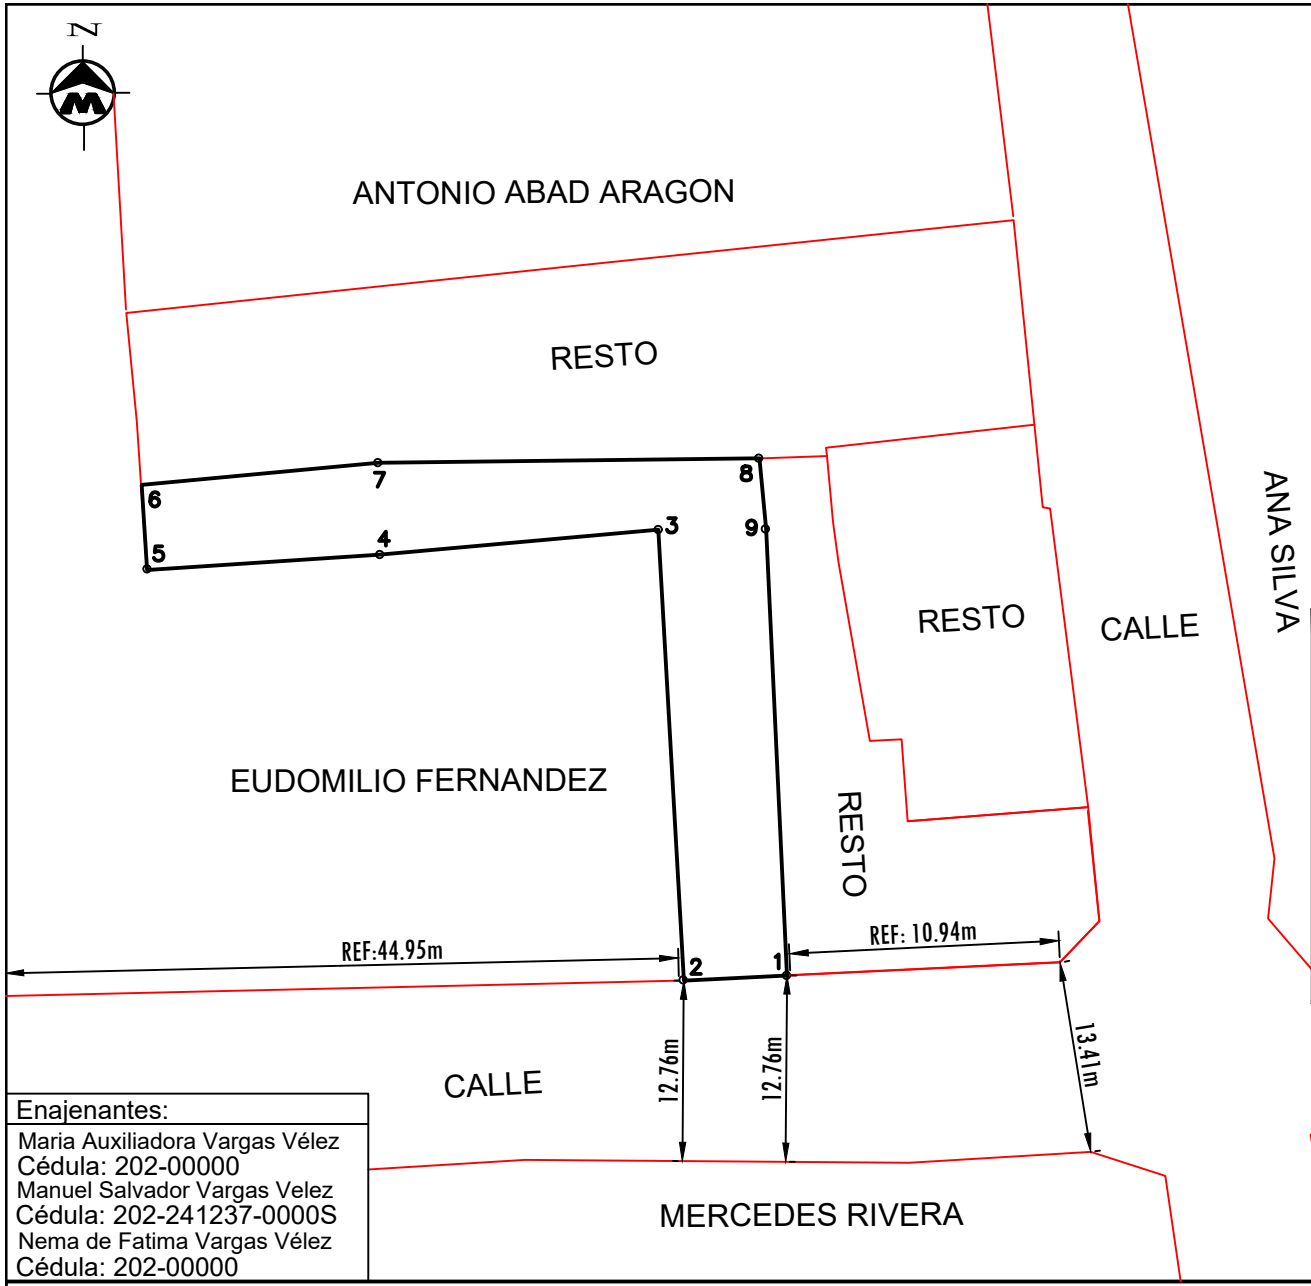

MUNICIPIO DE NANDAIME. DEPARTAMENTO DE GRANADA

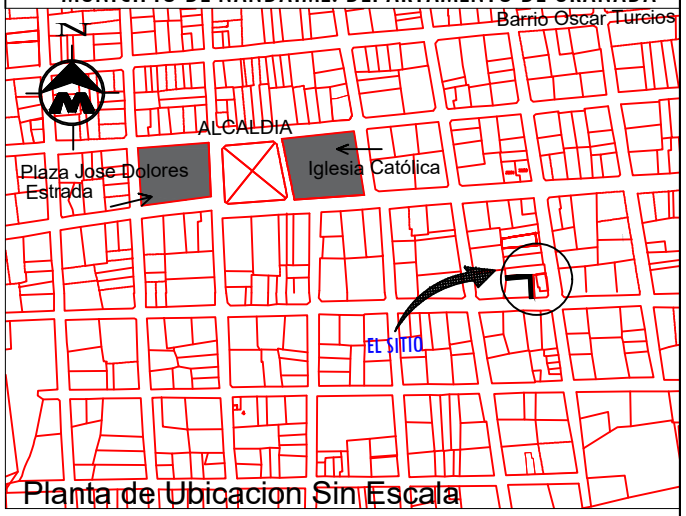

Planta de Ubicacion Sin Escala

Numero Catastral: 2951-2-08-092-40400

COORDENADAS NO VINCULADAS A LA RED GEODESICA DE NICARAGUA

CUADRO DE CONSTRUCCION

LADO EST	LADO PV	RUMBO	DISTANCIA	V	COORDENADAS Y	COORDENADAS X
				1	1,299,666.5600	603,387.5100
1	2	S 87°05'20.98" W	4.14	2	1,299,666.3500	603,383.3800
2	3	N 03°14'16.47" W	18.06	3	1,299,684.3800	603,382.3600
3	4	S 84°51'57.30" W	11.17	4	1,299,683.3800	603,371.2300
4	5	S 86°14'50.16" W	9.32	5	1,299,682.7700	603,361.9300
5	6	N 03°42'07.97" W	3.41	6	1,299,686.1700	603,361.7100
6	7	N 84°37'11.13" E	9.49	7	1,299,687.0600	603,371.1600
7	8	N 89°21'39.24" E	15.24	8	1,299,687.2300	603,386.4000
8	9	S 05°25'50.92" E	2.85	9	1,299,684.3900	603,386.6700
9	1	S 02°41'50.29" E	17.85	1	1,299,666.5600	603,387.5100
SUPERFICIE = 157.07 m2						

Enajenantes:
Maria Auxiliadora Vargas Vélez
Cédula: 202-00000
Manuel Salvador Vargas Velez
Cédula: 202-241237-0000S
Nema de Fatima Vargas Vélez
Cédula: 202-00000

Objeto Lev: Cesación de Comunidad	Numero Catastral: 2951-2-08-092-40400	Fecha: 23 de Septiembre del 2024	FIRMA:
ENAJENANTES: Arriba Reflejados	Ubicacion: Del Instituto Jose Dolores Estrada 1c al Este 1c al Sur Municipio de Nandaime. Departamento. Granada.	Ejecuta: Ing.Bosco Javier Morgan Lic. Catastral: BMM100426 Cel: 8883-7568 Email: ingmorgan73@gmail.com SERVICIOS TOPOGRAFICOS	
ADQUIRIENTE: Ileana del Socorro Vargas Vélez Cédula: 202-0000	Area: 157.07 m2 = 222.79 vrs2	Factor de Escala: 1.418415	Escala: 1 / 300