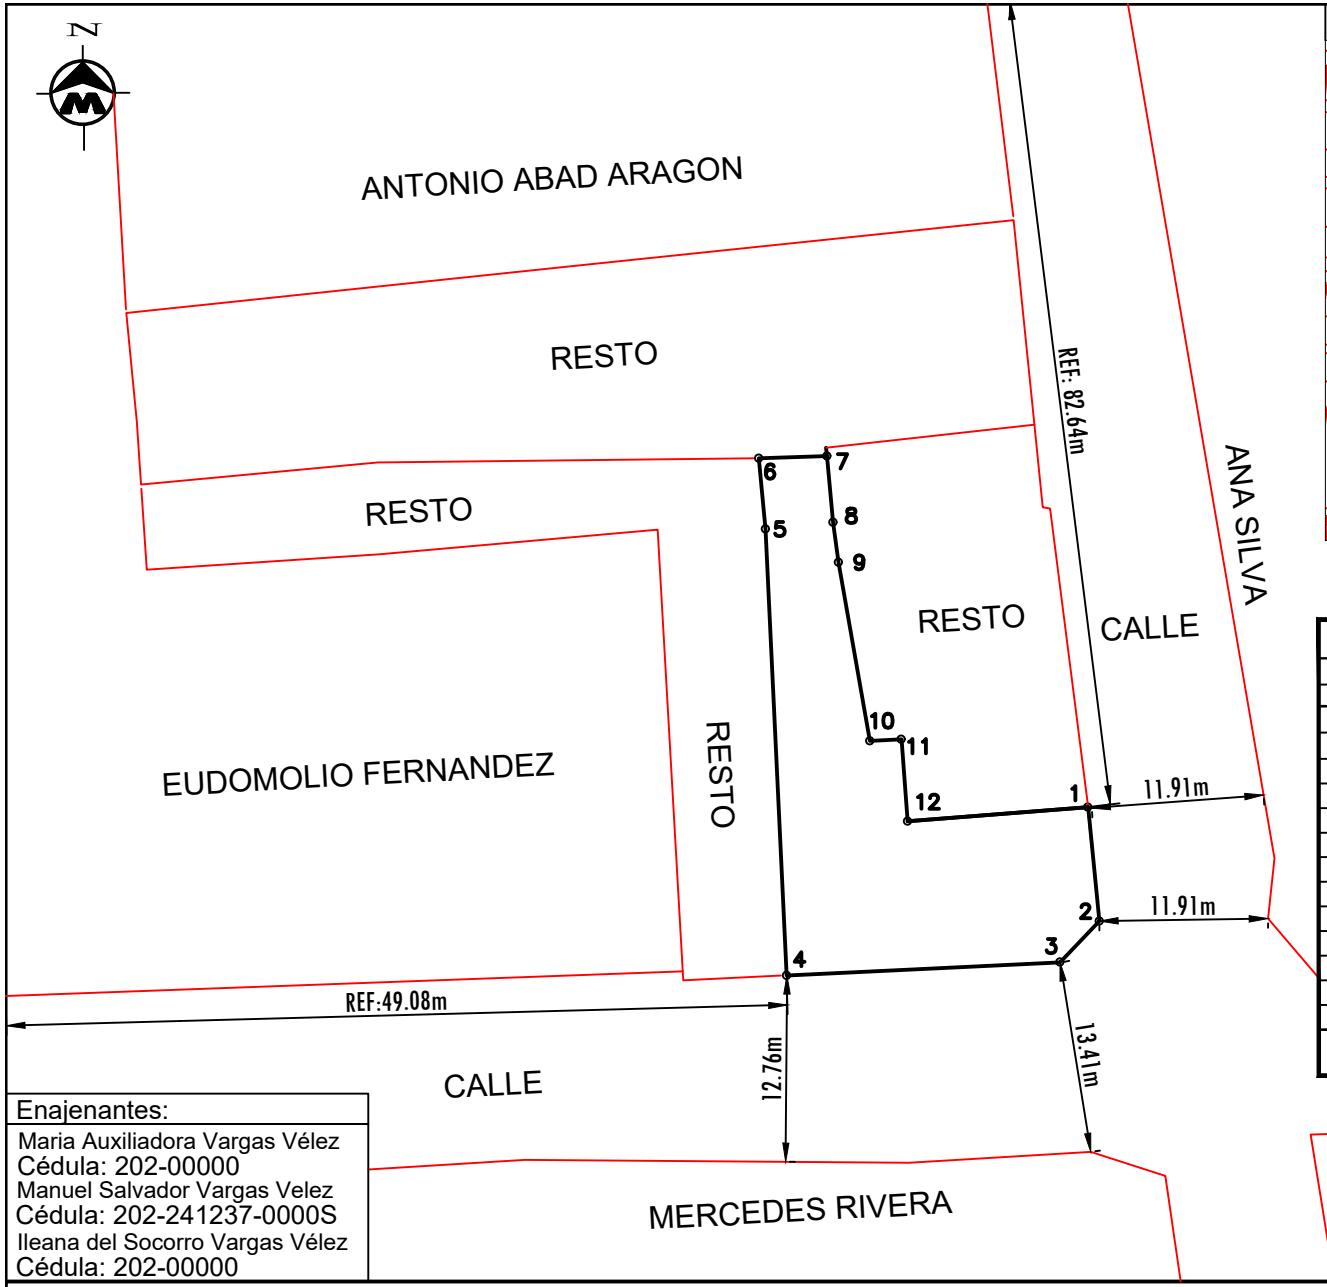

MUNICIPIO DE NANDAIME. DEPARTAMENTO DE GRANADA

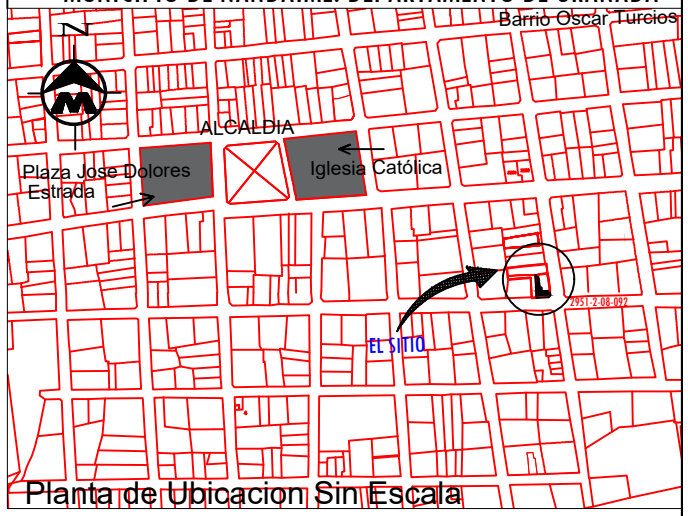

Planta de Ubicacion Sin Escala

Numero Catastral: 2951-2-08-092-40400

COORDENADAS NO VINCULADAS A LA RED GEODESICA DE NICARAGUA

CUADRO DE CONSTRUCCION

LADO EST	LADO PV	RUMBO	DISTANCIA	V	COORDENADAS Y	COORDENADAS X
				1	1,299,673.2800	603,399.5600
1	2	S 05°38'53.69" E	4.57	2	1,299,668.7300	603,400.0100
2	3	S 43°34'36.46" W	2.28	3	1,299,667.0800	603,398.4400
3	4	S 87°16'34.25" W	10.94	4	1,299,666.5600	603,387.5100
4	5	N 02°41'44.85" W	17.86	5	1,299,684.4000	603,386.6700
5	6	N 05°26'59.59" W	2.84	6	1,299,687.2300	603,386.4000
6	7	N 88°06'17.55" E	2.72	7	1,299,687.3200	603,389.1200
7	8	S 05°24'34.58" E	2.65	8	1,299,684.6800	603,389.3700
8	9	S 07°28'38.39" E	1.61	9	1,299,683.0800	603,389.5800
9	10	S 10°00'28.73" E	7.25	10	1,299,675.9400	603,390.8400
10	11	N 87°16'25.28" E	1.26	11	1,299,676.0000	603,392.1000
11	12	S 04°21'31.06" E	3.29	12	1,299,672.7200	603,392.3500
12	1	N 85°33'31.53" E	7.23	1	1,299,673.2800	603,399.5600

SUPERFICIE = 125.71 m2

Enajenantes:
Maria Auxiliadora Vargas Vélez
Cédula: 202-00000
Manuel Salvador Vargas Velez
Cédula: 202-241237-0000S
Ileana del Socorro Vargas Vélez
Cédula: 202-00000

Objeto Lev: Cesación de Comunidad	Numero Catastral: 2951-2-08-092-40400	Fecha: 23 de Septiembre del 2024	FIRMA:
ENAJENANTES: Arriba Reflejados	Ubicacion: Del Instituto Jose Dolores Estrada 1c al Este 1c al Sur Municipio de Nandaime. Departamento. Granada.	Ejecuta: Ing.Bosco Javier Morgan Lic. Catastral: BMM100426 Cel: 8883-7568 Email: ingmorgan73@gmail.com SERVICIOS TOPOGRAFICOS	
ADQUIRIENTE: Nema de Fatima Vargas Vélez Cédula: 202-0000	Area: 125.71 m2 = 178.31 vrs2 / Factor de Escala: 1.418415	Escala: 1 / 300	