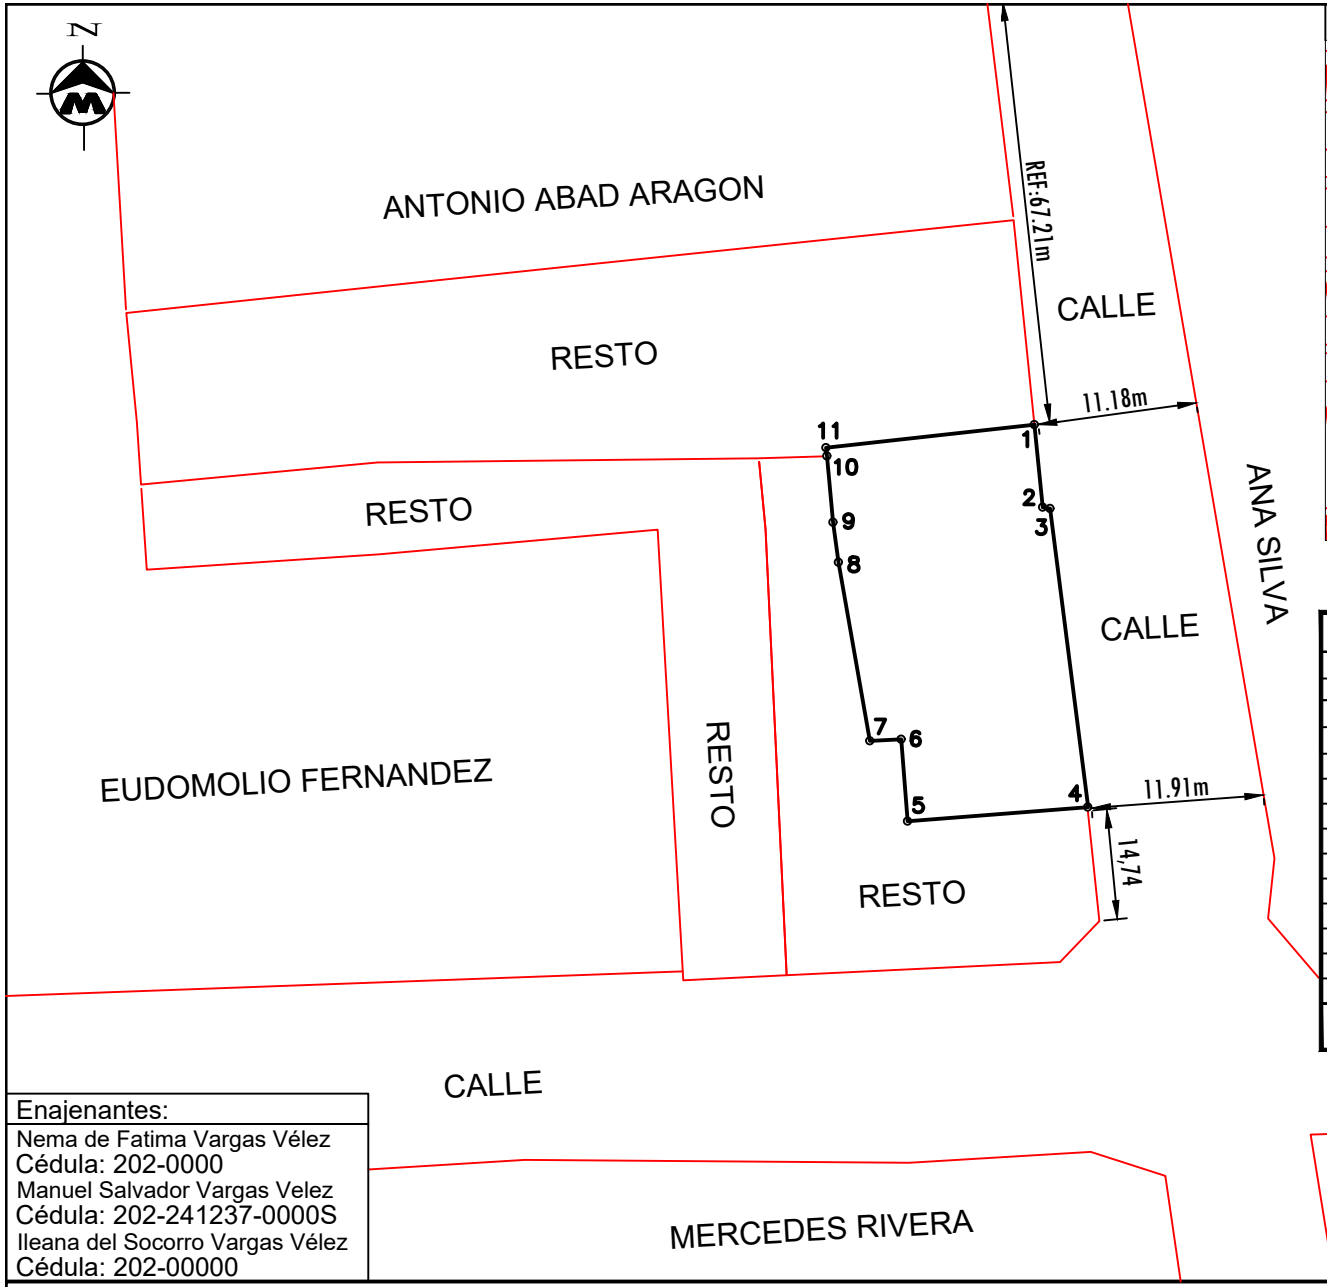

MUNICIPIO DE NANDAIME. DEPARTAMENTO DE GRANADA

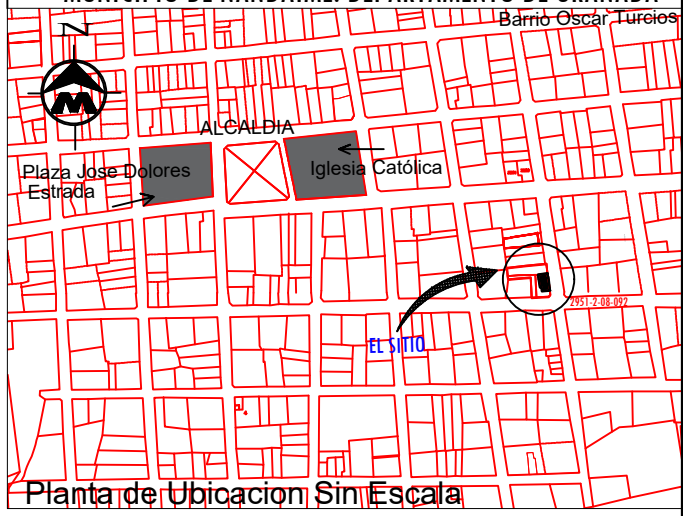

Planta de Ubicacion Sin Escala

Numero Catastral: 2951-2-08-092-40400

COORDENADAS NO VINCULADAS A LA RED GEODESICA DE NICARAGUA

CUADRO DE CONSTRUCCION

LADO EST	LADO PV	RUMBO	DISTANCIA	V	COORDENADAS Y	COORDENADAS X
				1	1,299,688.1800	603,397.8100
1	2	S 05°52'56.80" E	3.32	2	1,299,684.8800	603,398.1500
2	3	S 78°18'38.27" E	0.30	3	1,299,684.8200	603,398.4400
3	4	S 07°15'17.68" E	12.04	4	1,299,672.8800	603,399.9600
4	5	S 85°33'31.53" W	7.23	5	1,299,672.3200	603,392.7500
5	6	N 04°31'56.14" W	3.29	6	1,299,675.6000	603,392.4900
6	7	S 87°15'06.88" W	1.25	7	1,299,675.5400	603,391.2400
7	8	N 10°00'28.73" W	7.25	8	1,299,682.6800	603,389.9800
8	9	N 07°28'38.39" W	1.61	9	1,299,684.2800	603,389.7700
9	10	N 05°24'34.58" W	2.65	10	1,299,686.9200	603,389.5200
10	11	N 06°42'35.41" W	0.34	11	1,299,687.2600	603,389.4800
11	1	N 83°41'51.21" E	8.38	1	1,299,688.1800	603,397.8100

SUPERFICIE = 125.35 m2

Enajenantes:
Nema de Fatima Vargas Vélez
Cédula: 202-0000
Manuel Salvador Vargas Velez
Cédula: 202-241237-0000S
Ileana del Socorro Vargas Vélez
Cédula: 202-00000

Objeto Lev: Cesación de Comunidad	Numero Catastral: 2951-2-08-092-40400		Fecha: 23 de Septiembre del 2024 FIRMA:
ENAJENANTES: Arriba Reflejados	Ubicacion: Del Instituto Jose Dolores Estrada 1c al Este 1c al Sur Municipio de Nandaime. Departamento. Granada.		Ejecuta: Ing.Bosco Javier Morgan Lic. Catastral: BMM100426 Cel: 8883-7568 Email: ingmorgan73@gmail.com SERVICIOS TOPOGRAFICOS
ADQUIRIENTE: Maria Auxiliadora Vargas Vélez Cédula: 202-00000	Area: 125.35 m2 = 177.80 vrs2	Factor de Escala: 1.418415	Escala: 1 / 300