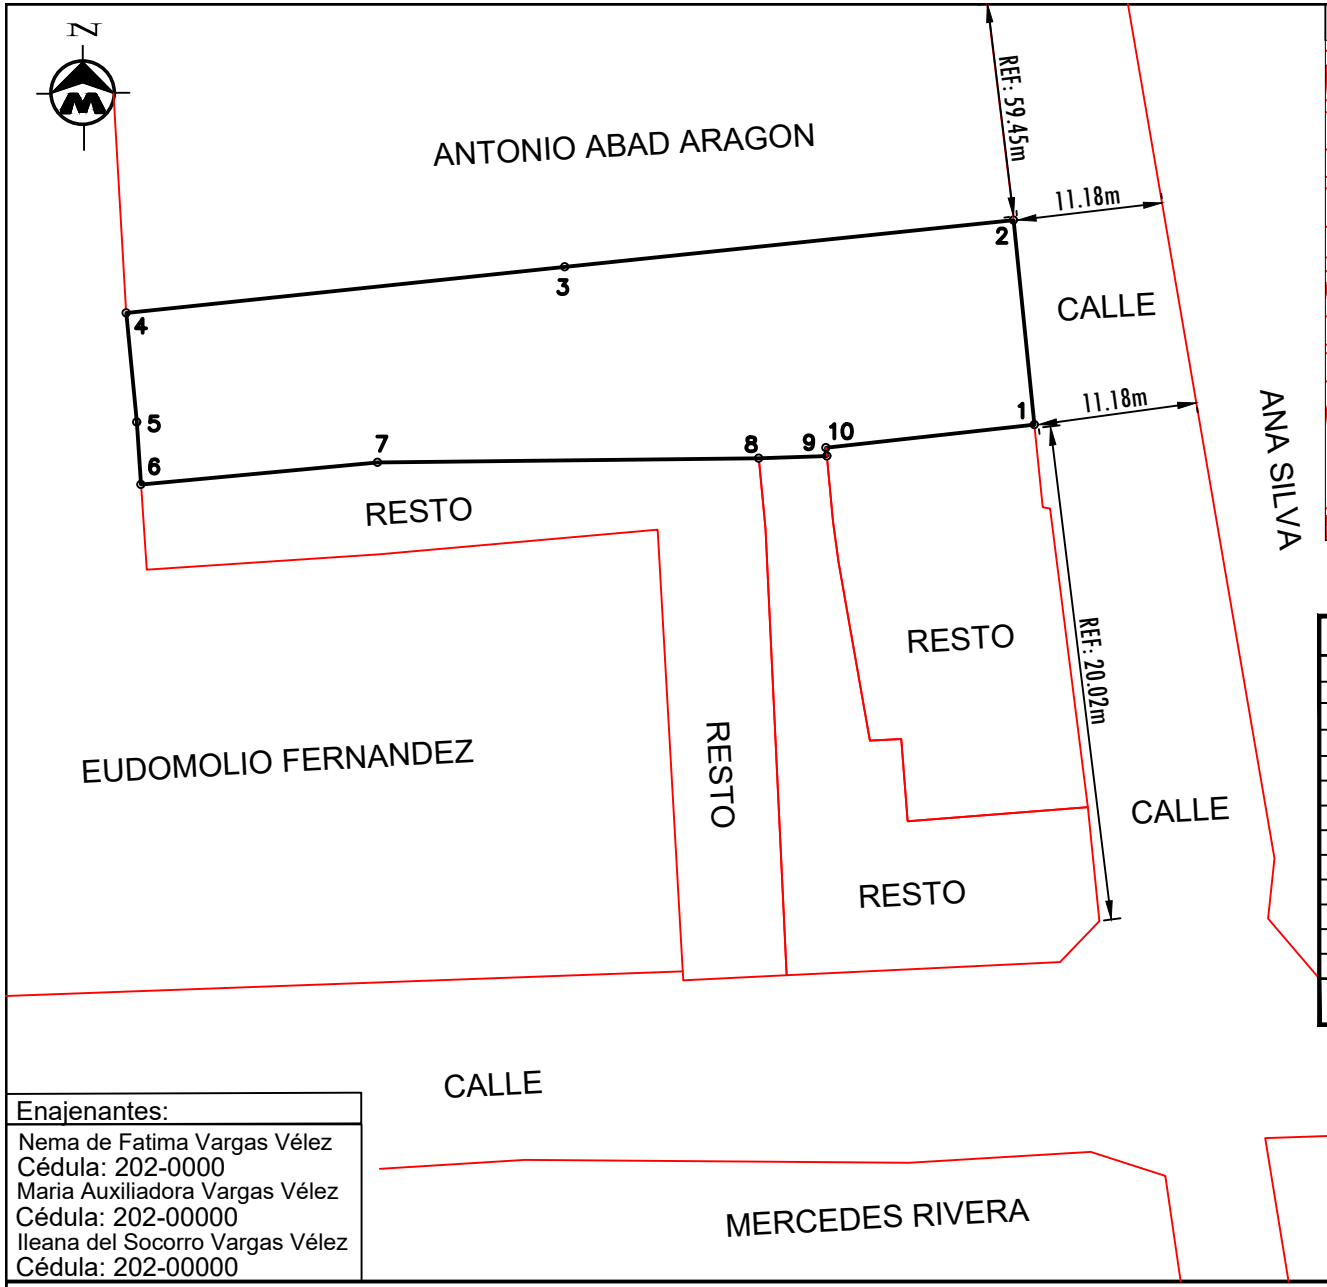

MUNICIPIO DE NANDAIME. DEPARTAMENTO DE GRANADA

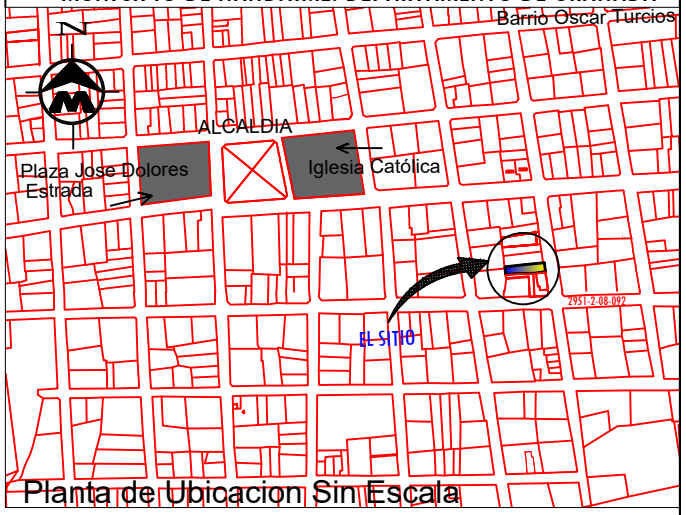

Planta de Ubicacion Sin Escala

Numero Catastral: 2951-2-08-092-40400

COORDENADAS NO VINCULADAS A LA RED GEODESICA DE NICARAGUA

CUADRO DE CONSTRUCCION

LADO EST	LADO PV	RUMBO	DISTANCIA	V	COORDENADAS Y	COORDENADAS X
				1	1,299,688.1753	603,397.8133
1	2	N 06°21'20.11" W	8.22	2	1,299,696.3453	603,396.9033
2	3	S 84°03'16.05" W	17.96	3	1,299,694.4853	603,379.0433
3	4	S 83°58'32.46" W	17.63	4	1,299,692.6353	603,361.5133
4	5	S 05°30'08.43" E	4.38	5	1,299,688.2753	603,361.9333
5	6	S 03°53'24.45" E	2.51	6	1,299,685.7753	603,362.1033
6	7	N 84°37'11.13" E	9.49	7	1,299,686.6653	603,371.5533
7	8	N 89°21'39.24" E	15.24	8	1,299,686.8353	603,386.7933
8	9	N 88°19'17.34" E	2.73	9	1,299,686.9153	603,389.5233
9	10	N 06°42'35.41" W	0.34	10	1,299,687.2553	603,389.4833
10	1	N 83°41'51.21" E	8.38	1	1,299,688.1753	603,397.8133

SUPERFICIE = 274.18 m2

Enajenantes:
Nema de Fatima Vargas Vélez
Cédula: 202-0000
Maria Auxiliadora Vargas Vélez
Cédula: 202-00000
Ileana del Socorro Vargas Vélez
Cédula: 202-00000

Objeto Lev: Cesación de Comunidad	Numero Catastral: 2951-2-08-092-40400		Fecha: 23 de Septiembre del 2024 FIRMA:
ENAJENANTES: Arriba Reflejados	Ubicacion: Del Instituto Jose Dolores Estrada 1c al Este 1c al Sur Municipio de Nandaime. Departamento. Granada.		Ejecuta: Ing.Bosco Javier Morgan Lic. Catastral: BMM100426 Cel: 8883-7568 Email: ingmorgan73@gmail.com SERVICIOS TOPOGRAFICOS
ADQUIRIENTE: Manuel Salvador Vargas Velez Cédula: 202-241237-0000S	Area: 274.18 m2 = 388.91 vrs2	Factor de Escala: 1.418415	Escala: 1 / 300