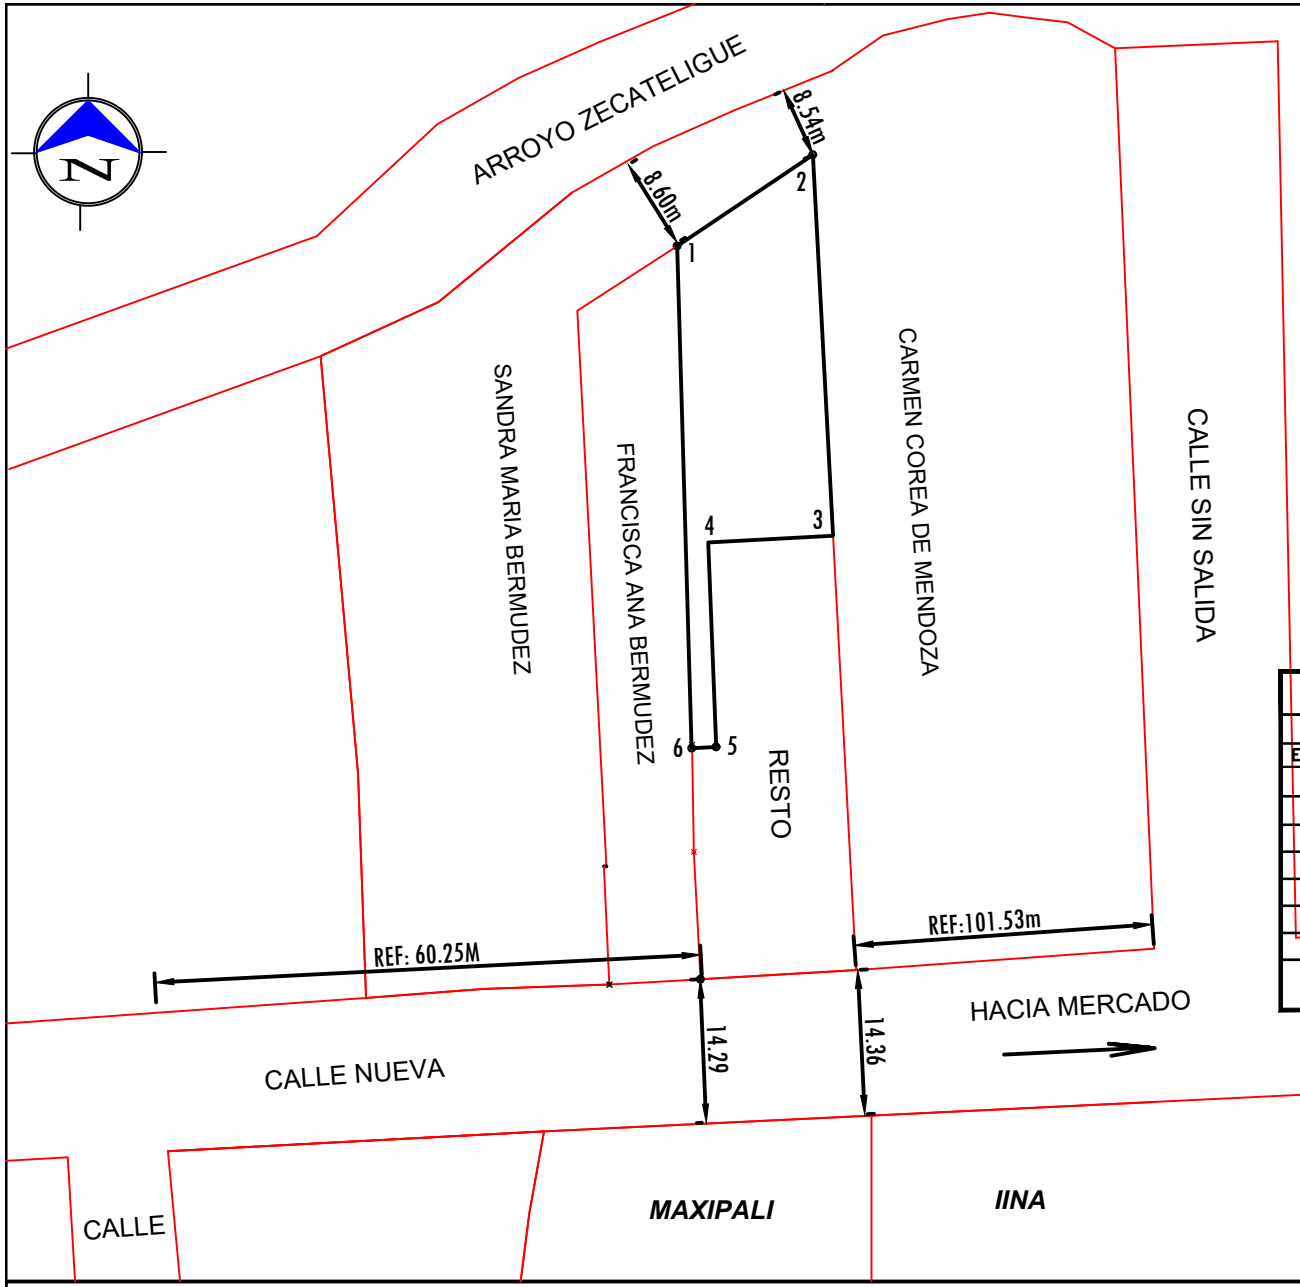

Planta de Ubicacion Sin Escala

COORDENADAS NO VINCULADAS A LA RED GEODESICA DE NICARAGUA

CUADRO DE CONSTRUCCION

LADO EST	LADO PV	RUMBO	DISTANCIA	V	COORDENADAS Y	COORDENADAS X
				1	1,318,403.1908	613,336.2087
1	2	N 56°01'17.03" E	10.89	2	1,318,409.2792	613,345.2424
2	3	S 03°01'50.85" E	25.42	3	1,318,383.8914	613,346.5866
3	4	S 86°58'09.39" W	8.31	4	1,318,383.4520	613,338.2875
4	5	S 02°14'26.97" E	13.65	5	1,318,369.8102	613,338.8213
5	6	S 87°31'21.67" W	1.65	6	1,318,369.7390	613,337.1756
6	1	N 01°39'20.28" W	33.47	1	1,318,403.1908	613,336.2087

SUPERFICIE = 237.59 m2

Objeto Lev: Desmembración- Compra Venta Parcial	Numero Catastral: 3051-4-05-087-16900	FIRMA:	SELLO
Enajenante: Wilfredo Bermudez Ortiz cédula: 201-041185-0003S	Ubicacion: Calle Nueva frente al supermercado Maxi Pali Municipio de Granada, Departamento de Granada.	Ejecuta: Ing.Carlos Solis Gaytan Lic. Catastral: CSG101406 Cel: 8884-3702 SERVICIOS TOPOGRAFICOS	
Adquiriente: Joseling Alejandra Delgado Abdalah cédula: 201-030393-0003U	Area:237.59 m2 = 337.01 vrs2 — Escala: 1 / 500	Fecha: 22 de Abril del 2024	