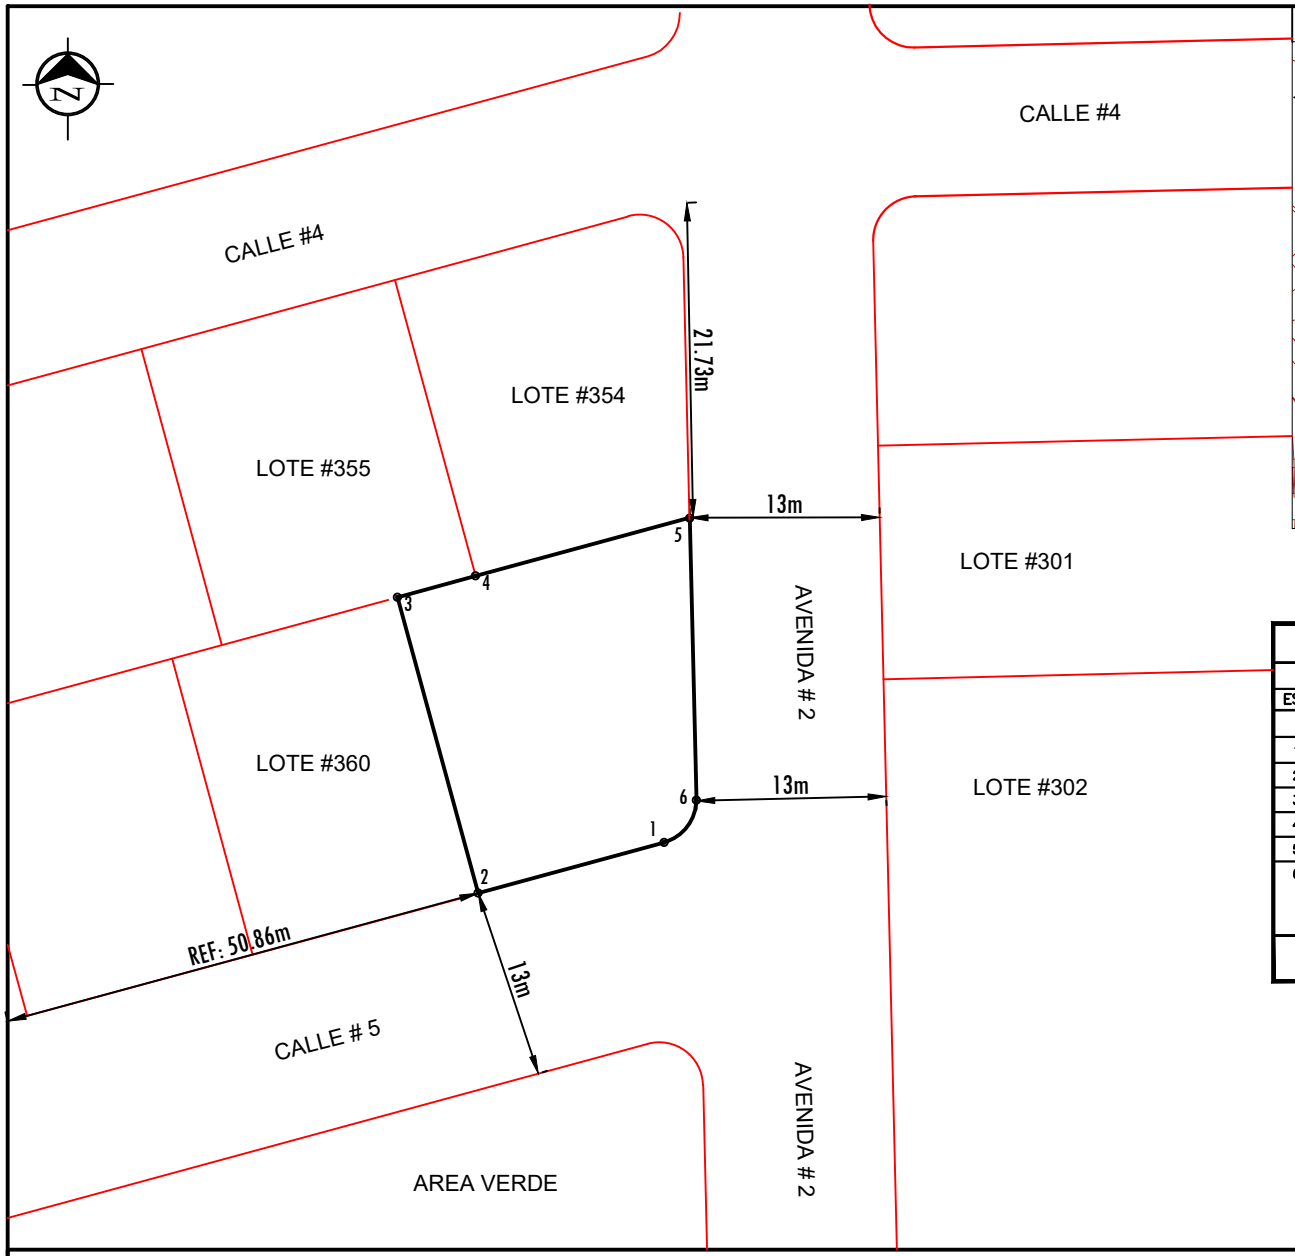

DEPARTAMENTO DE MASAYA, MUNICIPIO DE NINDIRI

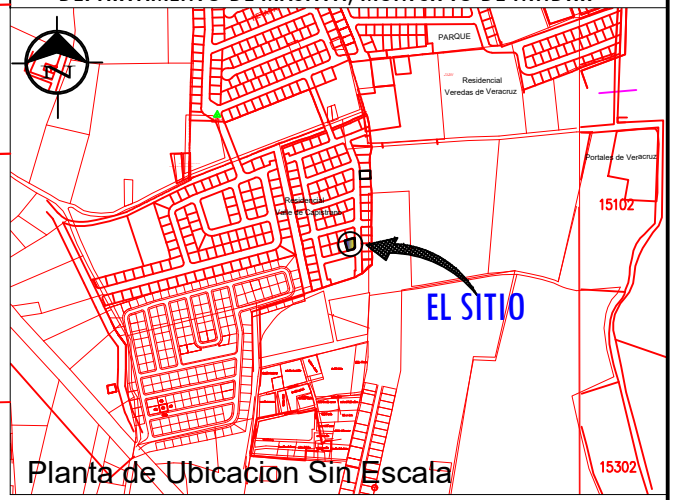

Planta de Ubicacion Sin Escala

Numero Catastral:2952-2-09-504-35600

COORDENADAS NO VINCULADAS A LA RED GEODESICA DE NICARAGUA

CUADRO DE CONSTRUCCION

LADO EST	LADO PV	RUMBO	DISTANCIA	V	COORDENADAS Y	COORDENADAS X
				1	1,332,345.7516	587,990.3985
1	2	S 74°46'21.84" W	13.19	2	1,332,342.2869	587,977.6700
2	3	N 15°13'38.16" W	21.00	3	1,332,362.5518	587,972.1538
3	4	N 74°46'21.84" E	5.53	4	1,332,364.0055	587,977.4942
4	5	N 74°46'21.84" E	15.20	5	1,332,367.9969	587,992.1576
5	6	S 01°20'38.60" E	19.29	6	1,332,348.7170	587,992.6099
6	1	S 36°42'51.62" W CENTRO DE CURVA DELTA = 76°7'0.44" RADIO = 3.00	3.70 LONG. CURVA = SUB.TAN.= 2.35	1 3.99	1,332,345.7516 1,332,348.6466	587,990.3985 587,989.6104

SUPERFICIE = 379.83 m2

Objeto Lev: Transcripcion Por Testamento Abierto	Numero Catastral:2952-2-09-504-35600	Fecha: 09 de septiembre del 2024	FIRMA:
Enajenante: Yamilelt del Carmen Gaitan Alvarado (Q.E.P.D) Defuncion: Partida # 152 Tomo: 10032 Folio: 152	Ubicacion: Residencial Valle de Capistrano lote # 361, Los Madrigales Municipio de Nindiri. Departamento de Masaya.	Ejecuta: Ing.Bosco Javier Morgan Lic. Catastral: BMM100426 Cel: 8883-7568 Email: ingmorgan73@gmail.com	
Adquiriente: Maria del Carmen Alvarado Guzman Cédula: 001-040245-0019Q	Area: 379.83 m2 = 538.75 vrs2	Escala: 1 /500	Factor de Escala: 1.418415