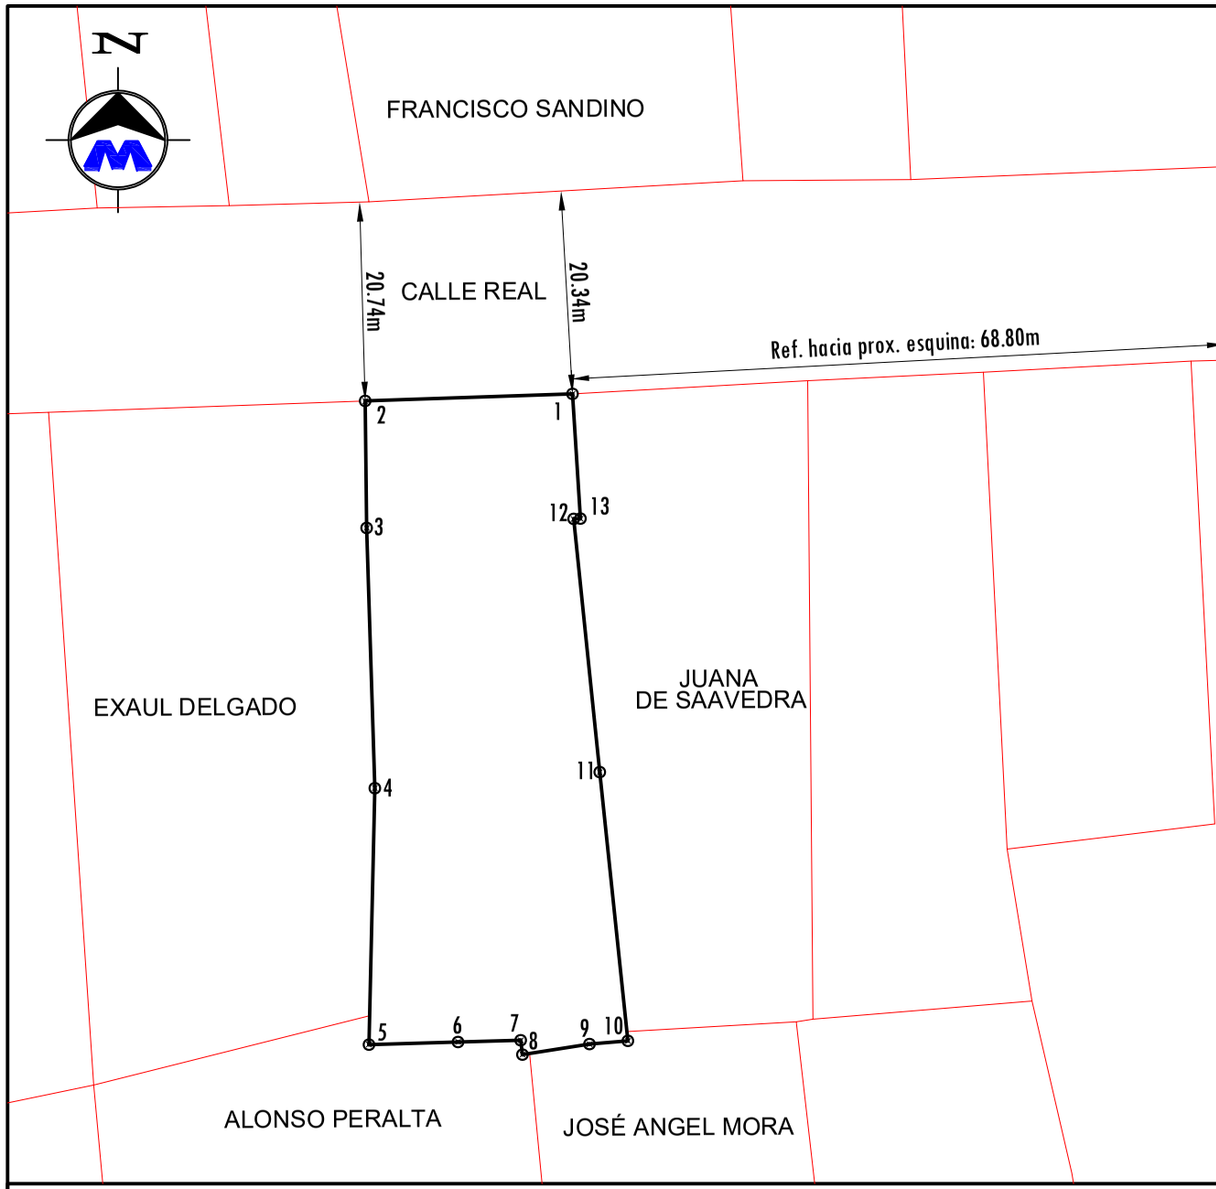

DEPARTAMENTO DE GRANADA MUNICIPIO DE GRANADA

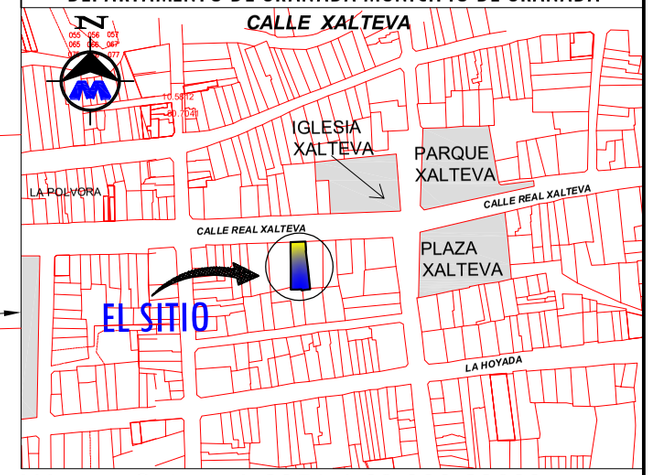

Número Catastral: 2951-1-08-000-20600
Planta de Ubicación Sin Escala

COORDENADAS NO VINCULADAS A LA RED GEODESICA DE NICARAGUA

CUADRO DE CONSTRUCCION

LADO EST	LADO PV	RUMBO	DISTANCIA	V	COORDENADAS Y	COORDENADAS X
				1	1,318,857.3059	613,100.9389
1	2	S 88°01'38.73" W	11.996	2	1,318,856.8930	613,088.9500
2	3	S 00°41'01.03" E	7.347	3	1,318,849.5466	613,089.0377
3	4	S 01°47'18.94" E	15.059	4	1,318,834.4950	613,089.5077
4	5	S 01°20'11.95" W	14.841	5	1,318,819.6578	613,089.1615
5	6	N 88°16'34.26" E	5.164	6	1,318,819.8131	613,094.3234
6	7	N 88°27'35.45" E	3.622	7	1,318,819.9105	613,097.9440
7	8	S 06°40'47.70" E	0.838	8	1,318,819.0785	613,098.0415
8	9	N 81°08'28.01" E	3.930	9	1,318,819.6836	613,101.9241
9	10	N 85°12'55.84" E	2.225	10	1,318,819.8692	613,104.1409
10	11	N 05°58'22.41" W	15.630	11	1,318,835.4147	613,102.5144
11	12	N 05°53'40.99" W	14.732	12	1,318,850.0690	613,101.0014
12	13	N 88°03'14.46" E	0.400	13	1,318,850.0825	613,101.4012
13	1	N 03°39'42.36" W	7.238	1	1,318,857.3059	613,100.9389

SUPERFICIE: 489.175 m2 = 693.85 Vrs2

ESPACIO PARA ESQUELA

Objeto Lev: Venta Total	Número Catastral: 3051-4-05-077-18000	FIRMA:
Enajenante: Angelina Mercedes Vega Duarte C.C. Angelina Vega de Perez. Ced: 201-070928-0001T	Ubicación: De Plaza Xalteva 75 Vrs al Oeste, Calle Real Xalteva. Municipio de Granada, Departamento de Granada.	Ejecuta: Ing.Bosco Javier Morgan Lic. Catastral: BMM100426 Cel: 8883-7568 Email: ingmorgan73@gmail.com servicios topograficos
Adquiriente: Alejandro Octavio Delgado Marquez Ced: 201-090569-0004C	Área: 489.175 m² = 693.85 Vrs² — Escala: 1 / 400	Fecha: 09 de Junio 2025