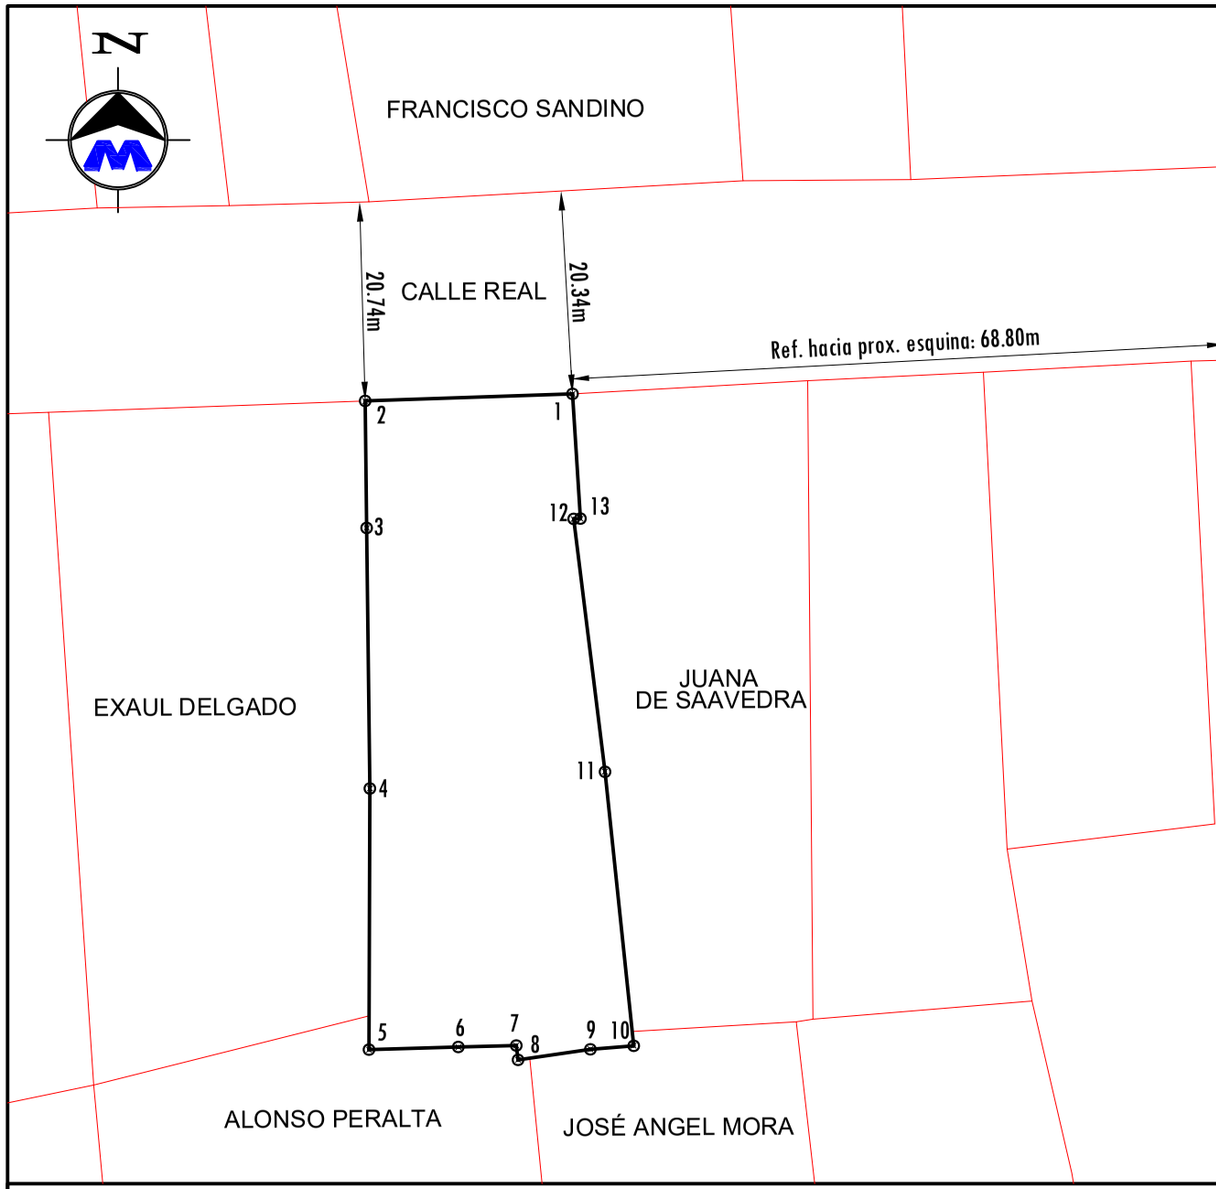

DEPARTAMENTO DE GRANADA MUNICIPIO DE GRANADA

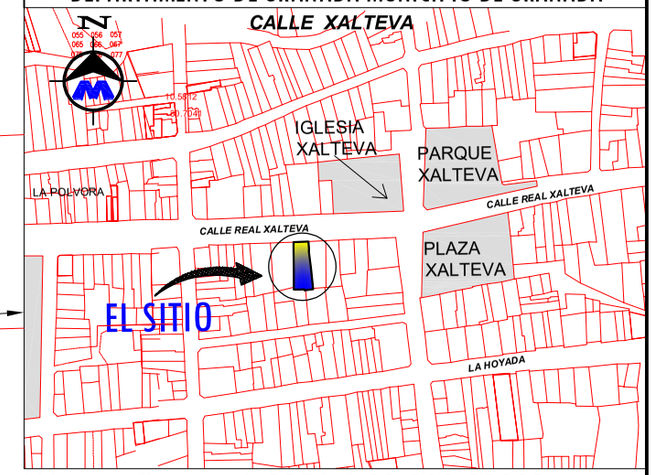

Número Catastral: 2951-1-08-000-20600
Planta de Ubicación Sin Escala

COORDENADAS NO VINCULADAS A LA RED GEODESICA DE NICARAGUA

CUADRO DE CONSTRUCCION

LADO EST	LADO PV	RUMBO	DISTANCIA	V	COORDENADAS Y	COORDENADAS X
				1	1,318,857.3059	613,100.9389
1	2	S 88°01'38.73" W	11.996	2	1,318,856.8930	613,088.9500
2	3	S 00°41'01.03" E	7.347	3	1,318,849.5466	613,089.0377
3	4	S 00°42'22.71" E	15.074	4	1,318,834.4739	613,089.2235
4	5	S 00°12'04.82" W	15.112	5	1,318,819.3621	613,089.1704
5	6	N 88°19'15.87" E	5.173	6	1,318,819.5136	613,094.3408
6	7	N 88°26'35.48" E	3.339	7	1,318,819.6043	613,097.6790
7	8	S 07°26'01.61" E	0.838	8	1,318,818.7737	613,097.7874
8	9	N 81°39'21.95" E	4.228	9	1,318,819.3872	613,101.9703
9	10	N 85°15'56.50" E	2.510	10	1,318,819.5943	613,104.4716
10	11	N 05°58'26.86" W	15.938	11	1,318,835.4453	613,102.8128
11	12	N 07°03'40.12" W	14.735	12	1,318,850.0690	613,101.0014
12	13	N 88°03'14.46" E	0.400	13	1,318,850.0825	613,101.4012
13	1	N 03°39'42.36" W	7.238	1	1,318,857.3059	613,100.9389

SUPERFICIE: 504.984 m2 = 716.28 Vrs2

Objeto Lev: Venta Total	Número Catastral: 3051-4-05-077-18000	FIRMA:
Enajenante: Angelina Mercedes Vega Duarte Ced: 201-070928-0001T	Ubicación: De Plaza Xalteva 75 Vrs al Oeste, Calle Real Xalteva. Municipio de Granada, Departamento de Granada.	Ejecuta: Ing.Bosco Javier Morgan Lic. Catastral: BMM100426 Cel: 8883-7568 Email: ingmorgan73@gmail.com servicios topograficos
Adquiriente: Alejandro Octavio Delgado Marquez Ced: 201-090569-0004C	Área: 504.984 m² = 716.28 Vrs² — Escala: 1 / 400	Fecha: 06 de Junio 2025

ESPACIO PARA ESQUELA