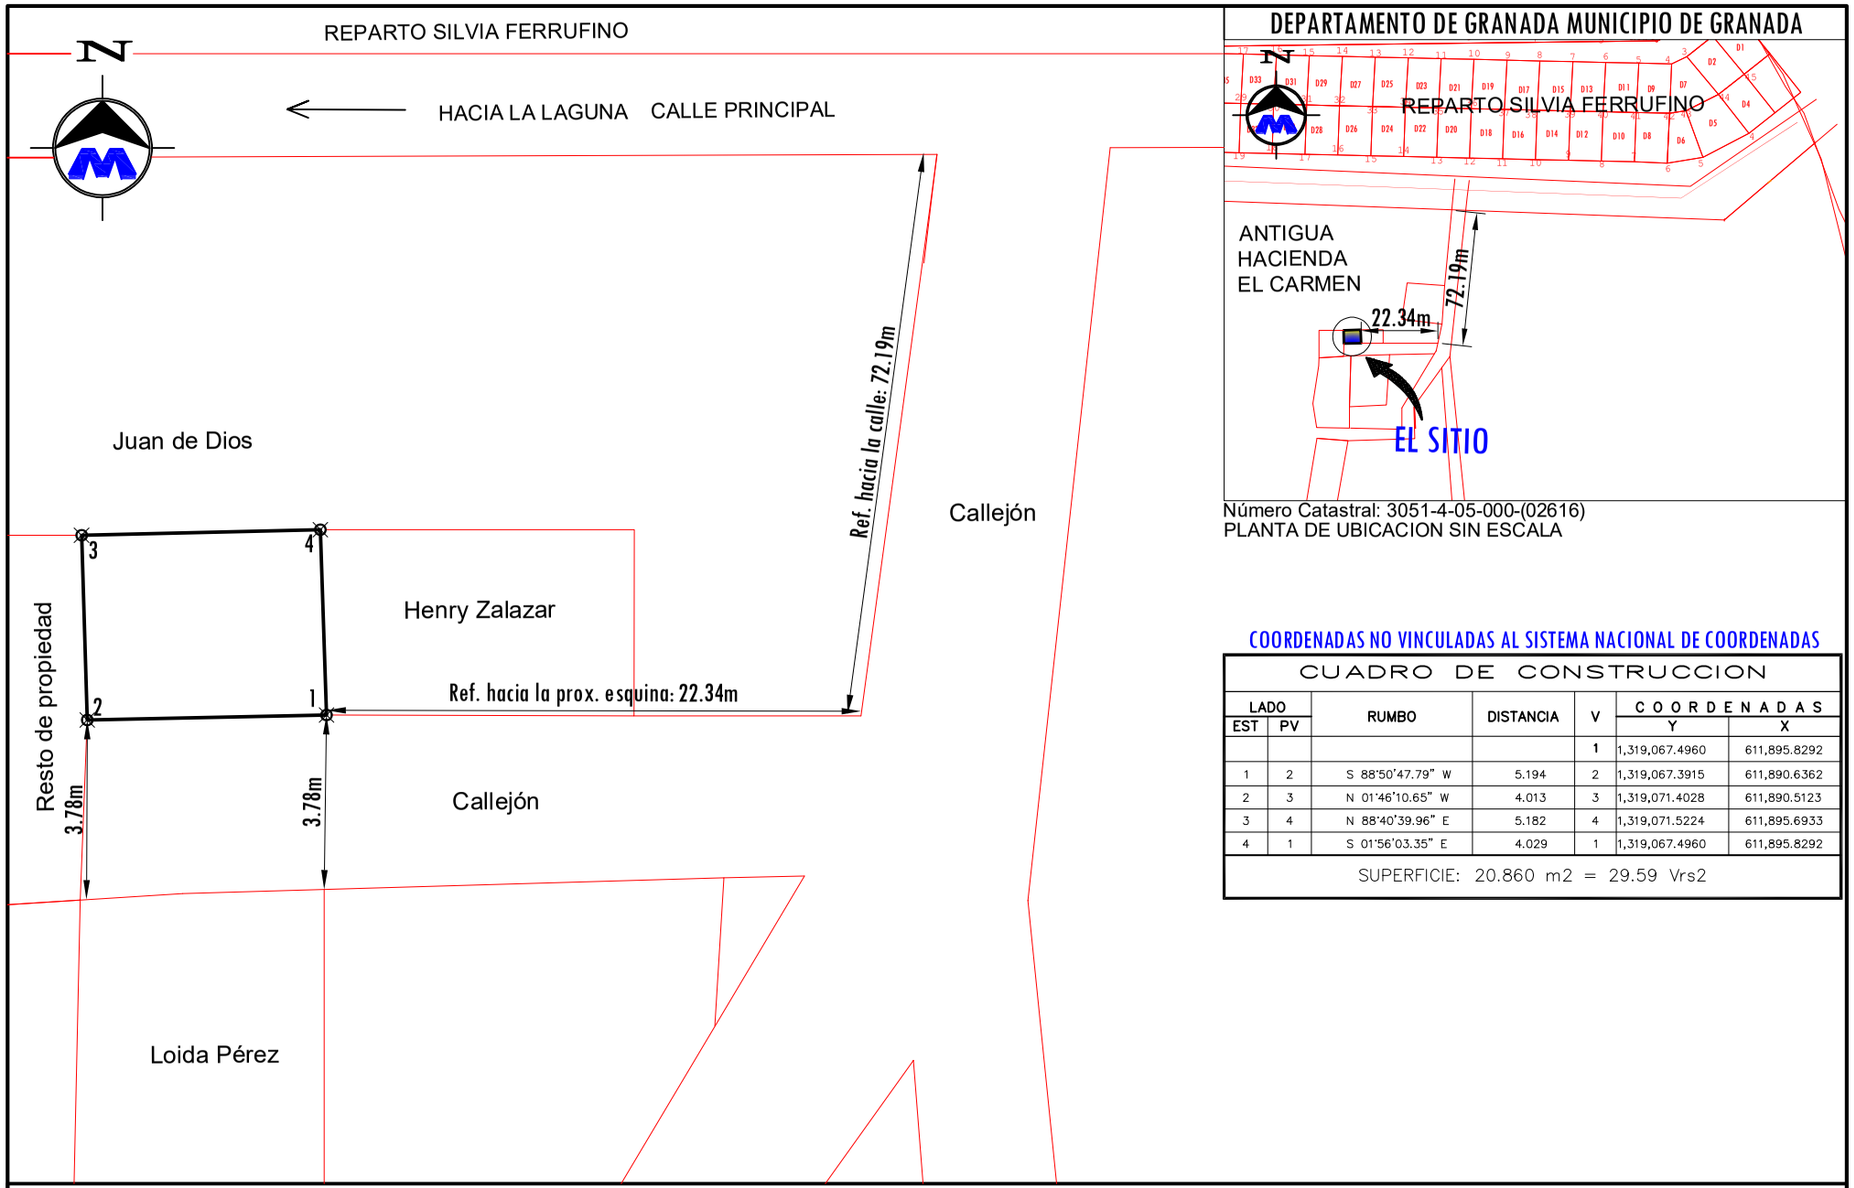

DEPARTAMENTO DE GRANADA MUNICIPIO DE GRANADA

Número Catastral: 3051-4-05-000-(02616)
PLANTA DE UBICACION SIN ESCALA

COORDENADAS NO VINCULADAS AL SISTEMA NACIONAL DE COORDENADAS

CUADRO DE CONSTRUCCION

LADO EST	LADO PV	RUMBO	DISTANCIA	V	COORDENADAS Y	COORDENADAS X
				1	1,319,067.4960	611,895.8292
1	2	S 88°50'47.79" W	5.194	2	1,319,067.3915	611,890.6362
2	3	N 01°46'10.65" W	4.013	3	1,319,071.4028	611,890.5123
3	4	N 88°40'39.96" E	5.182	4	1,319,071.5224	611,895.6933
4	1	S 01°56'03.35" E	4.029	1	1,319,067.4960	611,895.8292

SUPERFICIE: 20.860 m2 = 29.59 Vrs2

Objeto Lev: Desmembración- Venta Parcial	Número Catastral: 3051-4-05-000-02616	FIRMA:
Enajenante: Luis Emilio Pabon Arias Cédula: 203-210626-0001A	Ubicación: De la primera entrada al Rpto Silvia Ferrufino 139 m al oeste 72.19 m al Sur y 22.34 m al Oeste. Sector El Carmen Municipio de Granada. Departamento de Granada.	Ejecuta: Ing.Bosco Javier Morgan Lic. Catastral: BMM100426 Cel: 8883-7568 Email: ingmorgan73@gmail.com www.morganconstrucciones.com
Adquiriente: Bernarda del Socorro Barberena Suarez Ced:201-200570-0006X	Área: 20.86 m² = 29.59 Vrs2 — Escala: 1 /150	Fecha: 24 de Junio del 2025

ESPACIO PARA ESQUELA