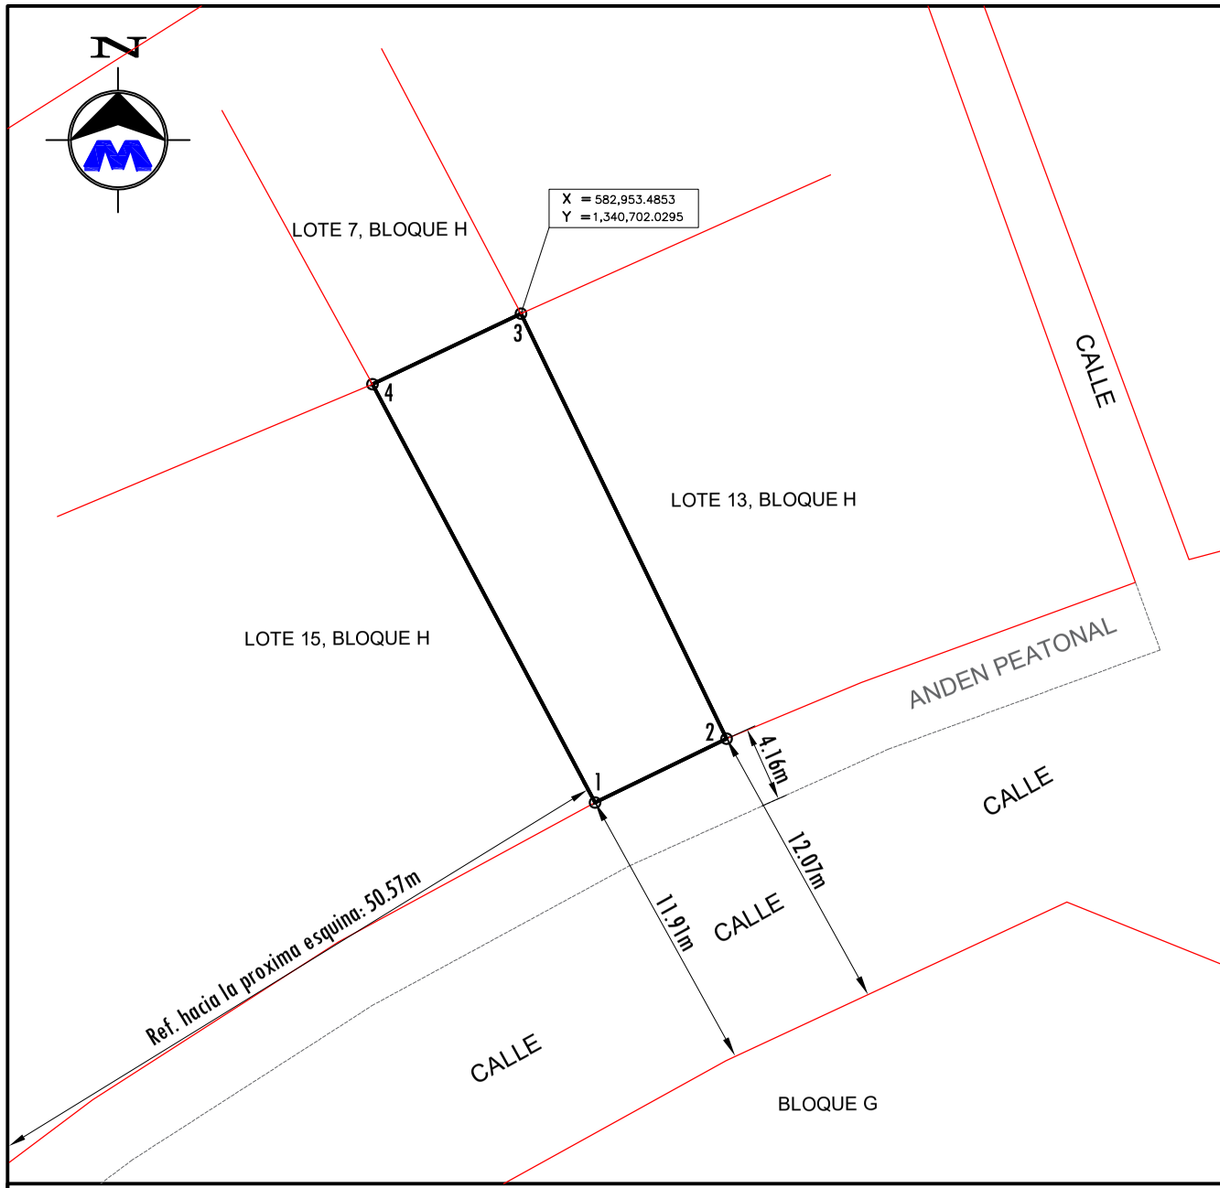

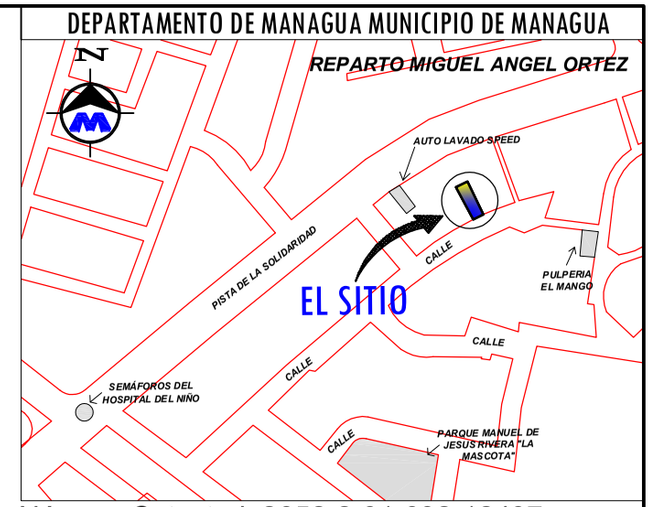

Número Catastral: 2952-2-01-092-12407
Planta de Ubicación Sin Escala

COORDENADAS NO VINCULADAS A LA RED GEODESICA DE NICARAGUA

CUADRO DE CONSTRUCCION

LADO EST	LADO PV	RUMBO	DISTANCIA	V	COORDENADAS Y	COORDENADAS X
				1	1,340,677.8201	582,966.3514
1	2	N 64°04'01.69" E	8.460	2	1,340,681.5198	582,973.9596
2	3	N 25°48'49.28" W	27.317	3	1,340,706.1114	582,962.0643
3	4	S 64°33'18.89" W	9.501	4	1,340,702.0295	582,953.4853
4	1	S 27°59'18.62" E	27.416	1	1,340,677.8201	582,966.3514

SUPERFICIE: 245.658 m2 = 348.44 Vrs2

Objeto Lev: Transcripción por Declaratoria de Herederos	Número Catastral: 2952-2-01-092-12407	FIRMA:
Enajenante: Celina del Carmen Flores Leiva Tomo:10098; Folio: 198; Partida: 198 Conocida Registralmente como Celina Flores Leiva	Ubicación: Reparto Miguel Angel Ortez, de los Semáforos del Hospital del Niño 1c al S, 2 ½ c al E. Municipio de Managua, Departamento de Managua.	Ejecuta: Ing.Bosco Javier Morgan Lic. Catastral: BMM100426 Cel: 8883-7568 Email: ingmorgan73@gmail.com servicios topograficos
Adquiriente: Maria Angela Flores de Elgaard Pasaporte: 212711674	Área: 245.658 m² = 348.44 Vrs² — Escala: 1 / 400	Fecha: 05 de Junio del 2025

ESPACIO PARA ESQUELA