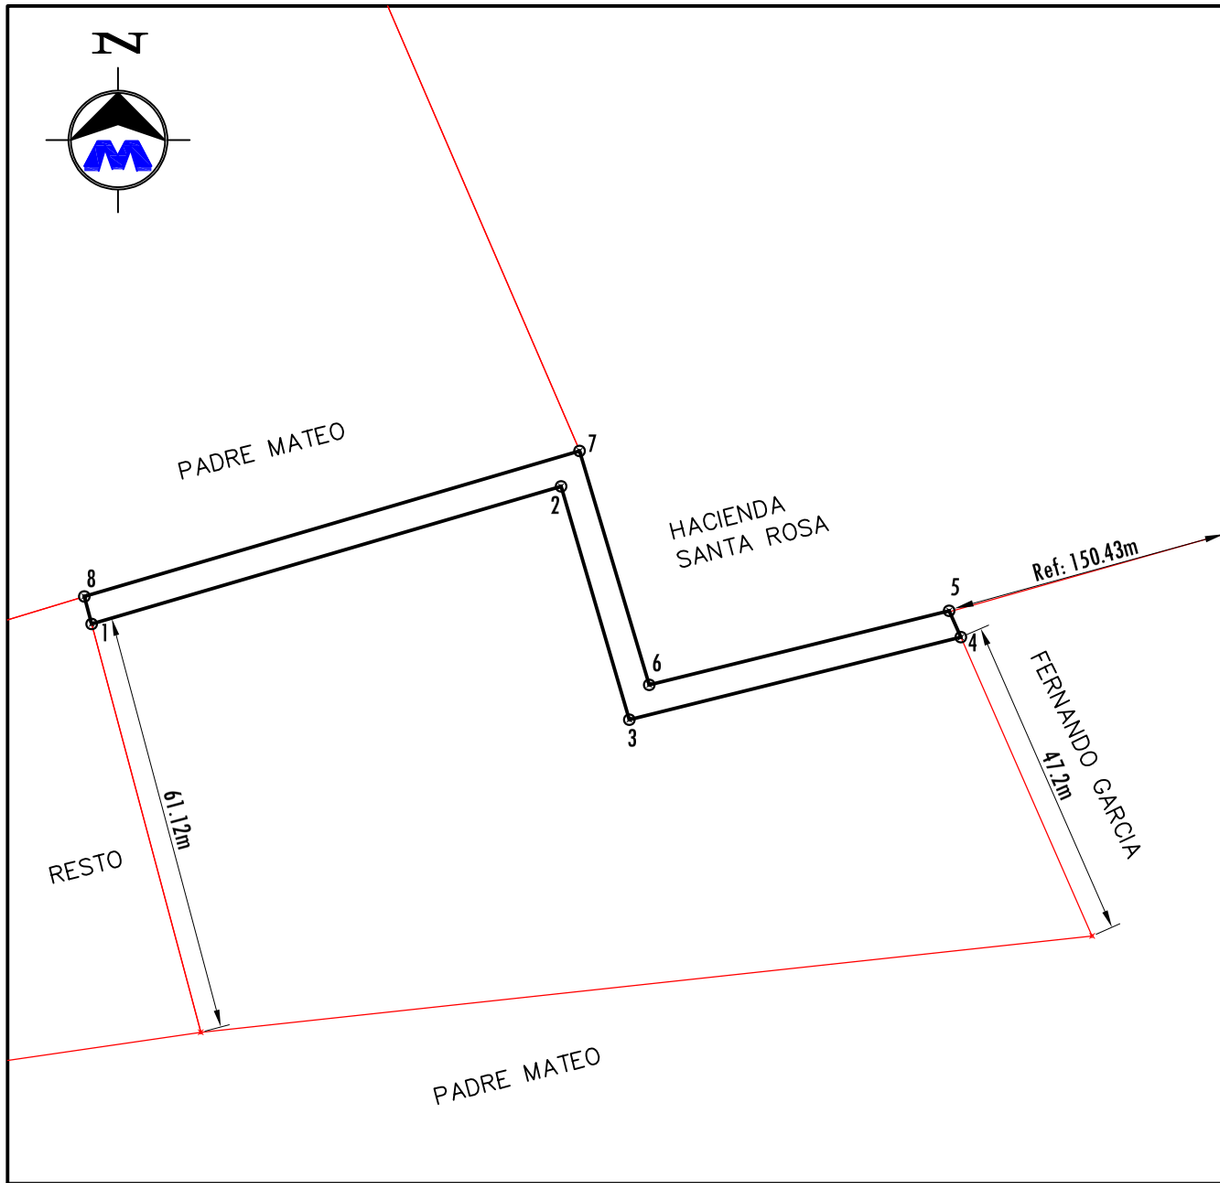

DEPARTAMENTO DE GRANADA MUNICIPIO DE GRANADA

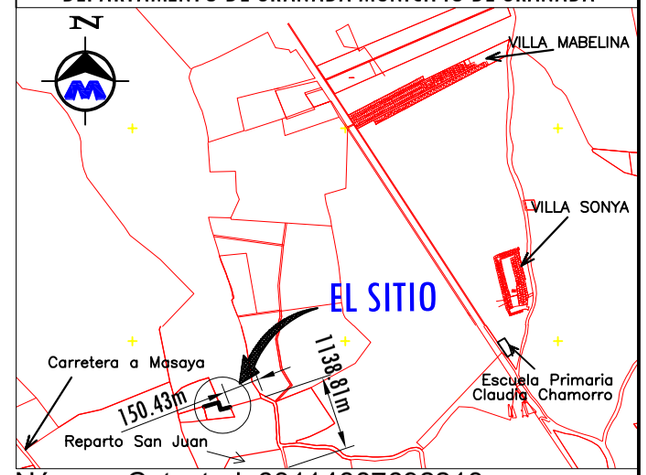

Número Catastral: 63114887692213
Planta de Ubicación Sin Escala

COORDENADAS NO VINCULADAS A LA RED GEODESICA DE NICARAGUA

CUADRO DE CONSTRUCCION

LADO EST	LADO PV	RUMBO	DISTANCIA	V	COORDENADAS Y	COORDENADAS X
				1	1,321,891.8037	611,348.1296
1	2	N 14°56'58.61" W	4.119	2	1,321,895.7832	611,347.0670
2	3	N 73°36'35.32" E	74.635	3	1,321,916.8434	611,418.6688
3	4	S 16°33'59.12" E	35.299	4	1,321,883.0100	611,428.7334
4	5	N 76°07'01.56" E	44.674	5	1,321,893.7289	611,472.1020
5	6	S 23°42'54.52" E	4.190	6	1,321,889.8927	611,473.7871
6	7	S 76°02'21.87" W	49.387	7	1,321,877.9779	611,425.8589
7	8	N 16°20'05.14" W	35.129	8	1,321,911.6889	611,415.9789
8	1	S 73°39'54.86" W	70.703	1	1,321,891.8037	611,348.1296

SUPERFICIE: 642.219 m2 = 910.43 Vrs2

Objeto Lev: Constitución de Servidumbre de Paso	Numero Catastral: 3051-4-05-000-01008	FIRMA:
Dominante: Alberto Jose Padilla Ced: 201-151062-0005M	Ubicacion: Comarca Capulín # 1, costado Este del Reparto San Juan 1,081.34m al Noroeste,57.47m N-W, 150.43m S-W Municipio de Granada, Dpto. de Granada.	Ejecuta: Ing.Bosco Javier Morgan Lic. Catastral: BMM100426 Cel: 8883-7568 Email: ingmorgan73@gmail.com servicios topograficos
Sirviente: Alvaro Jose Ramirez Garcia Ced: 281-070388-0001U	Área: 642.219 m² = 910.43 Vrs² — Escala: 1 / 1000	Fecha: 20 de Junio 2025

ESPACIO PARA ESQUELA