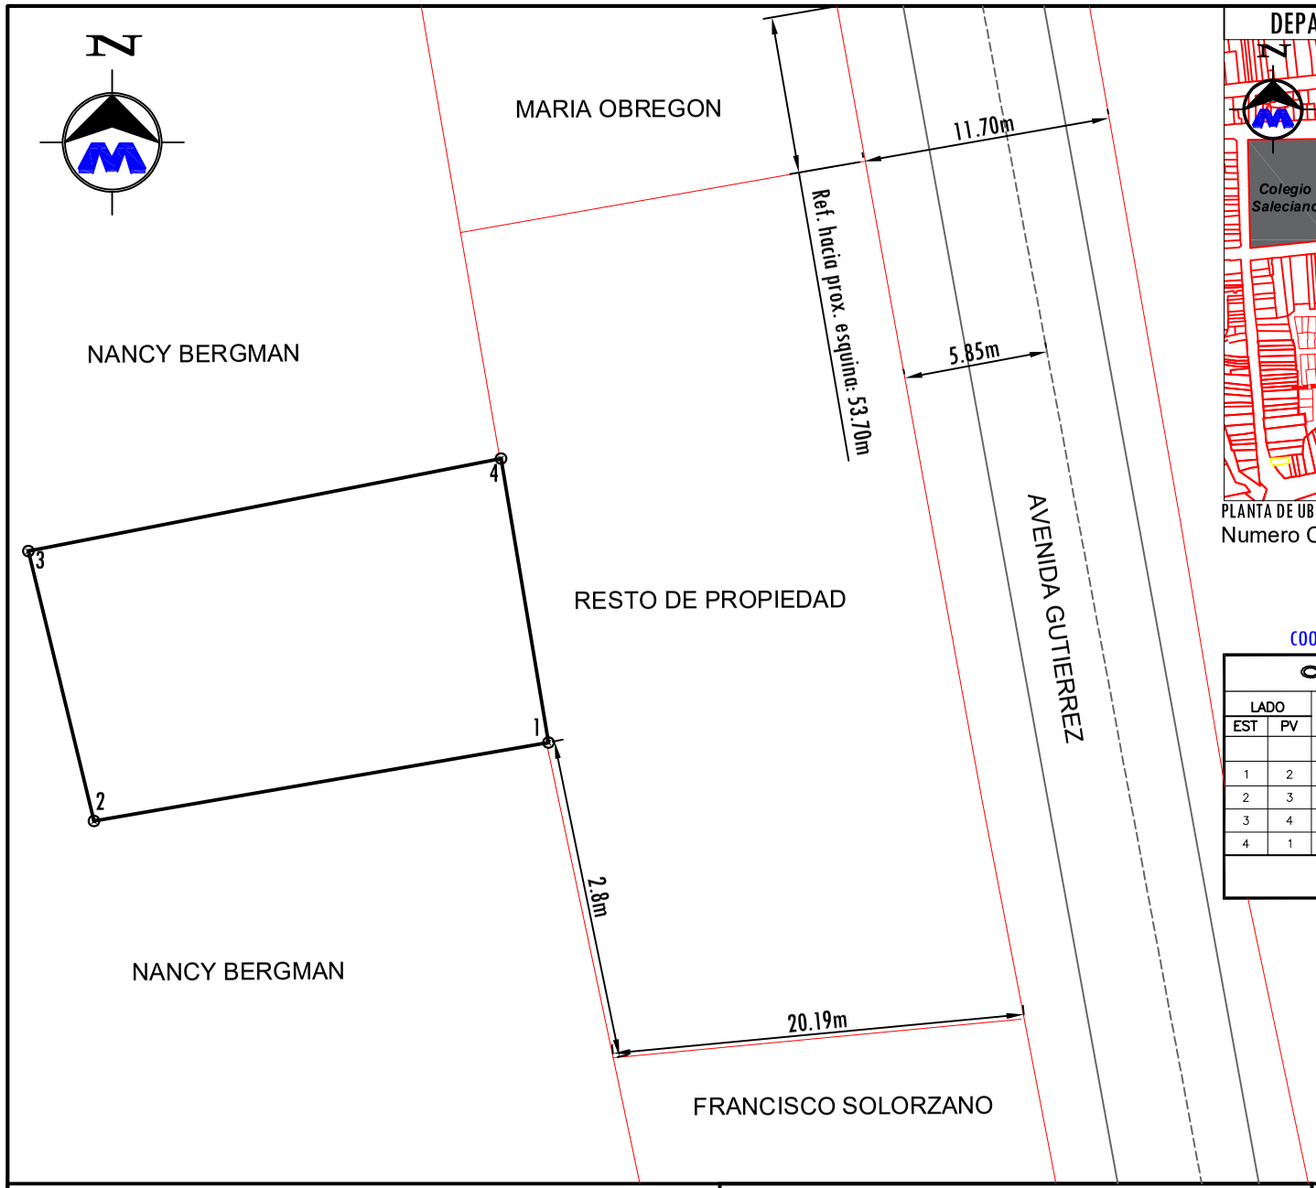

DEPARTAMENTO DE GRANADA MUNICIPIO DE GRANADA

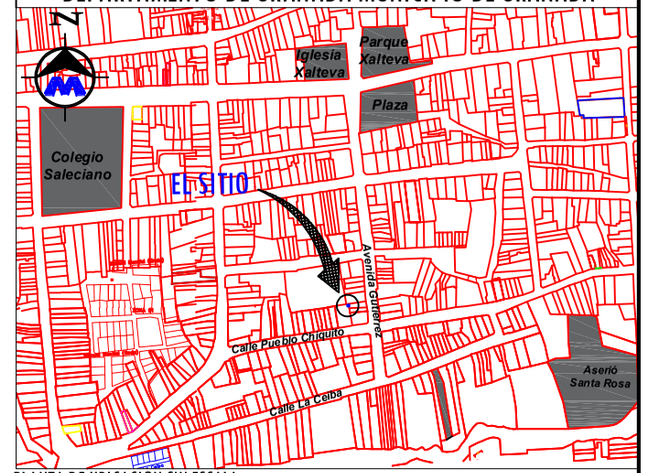

PLANTA DE UBICACION SIN ESCALA

Numero Catastral: 3051-4-05-087-38003

COORDENADAS NO VINCULADAS AL SISTEMA NACIONAL DE COORDENADAS

CUADRO DE CONSTRUCCION

LADO EST	LADO PV	RUMBO	DISTANCIA	V	COORDENADAS Y	COORDENADAS X
				1	1,318,594.1650	613,176.2834
1	2	S 80°11'27.15" W	1.334	2	1,318,593.9378	613,174.9693
2	3	N 13°40'23.44" W	0.804	3	1,318,594.7188	613,174.7793
3	4	N 78°55'44.11" E	1.393	4	1,318,594.9862	613,176.1459
4	1	S 09°30'19.12" E	0.833	1	1,318,594.1650	613,176.2834

SUPERFICIE: 1.114 m2 = 1.58 Vrs2

ESPACIO PARA ESQUELA

Objeto Lev: Desmembración	Número Catastral: 3051-4-05-087-38003	FIRMA:
Propietario: Alma Rosa Perez Mondoy Cédula: 201-050947-0004P	Ubicación: Calle Pueblo Chiquito, de la iglesia de Xalteva 3c y 53.70m al Sur. Municipio de Granada. Dpto Granada.	Ejecuta: Ing.Bosco Javier Morgan Lic. Catastral: BMM 100426 Celular: 8883-7568 SERVICIOS TOPOGRAFICOS
Adquiriente: Richard Philip Puntis Pasaporte: 520807186	Área: 1.14 m² = 1.58 Vrs² — Escala: 1 /50	Fecha: 30 de Junio del 2025