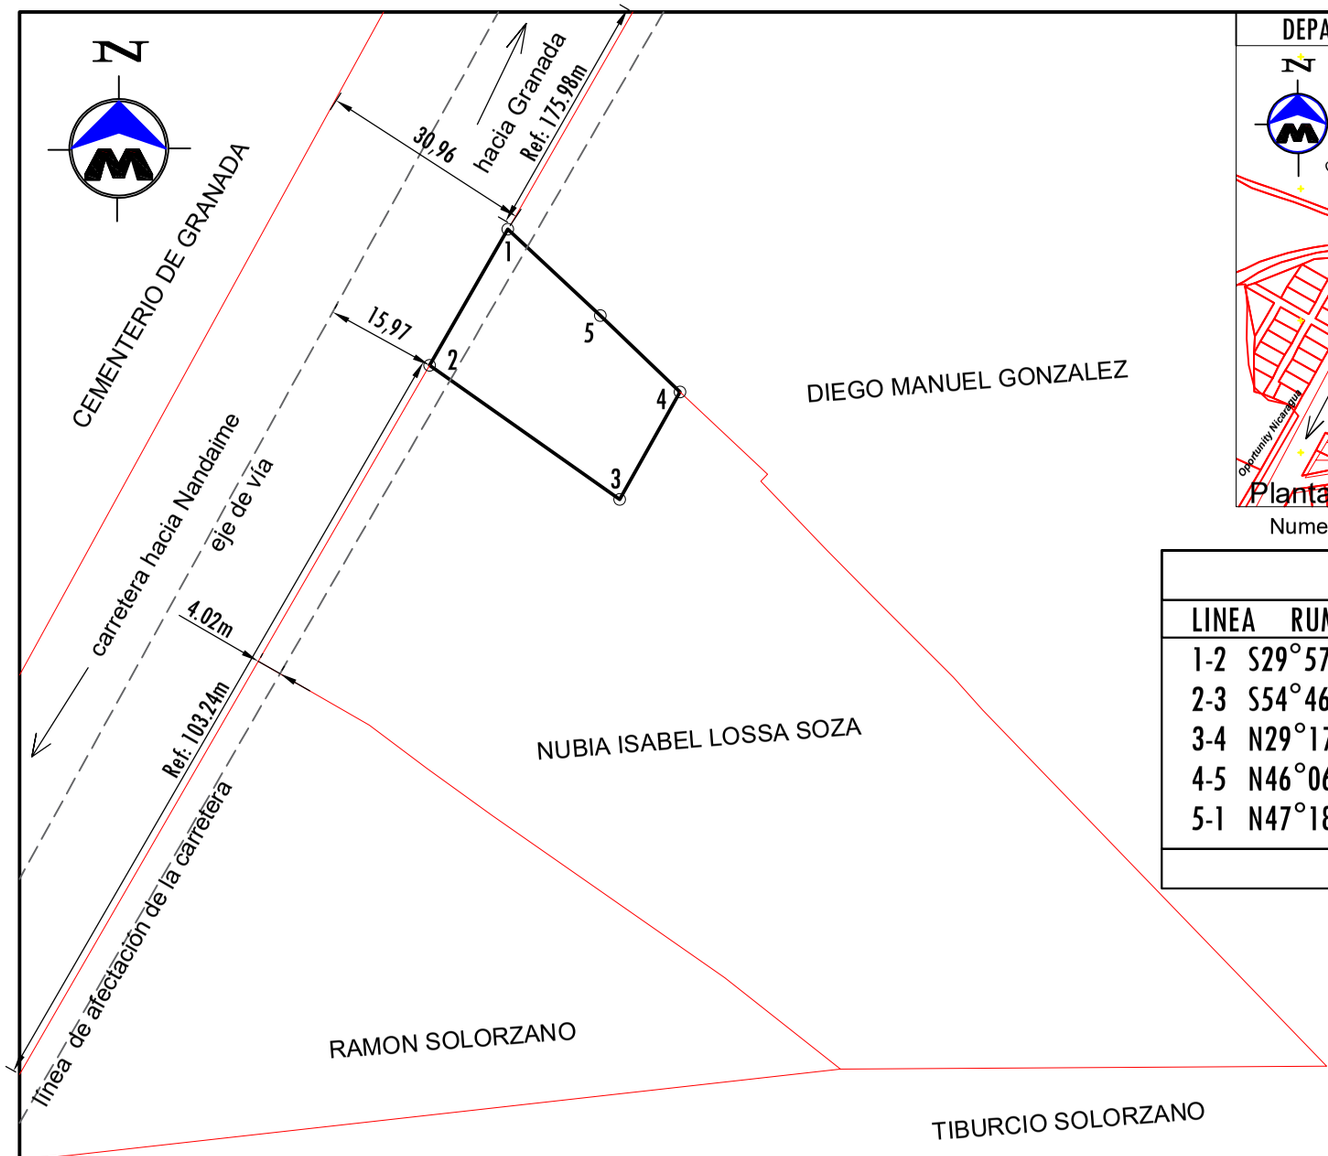

DEPARTAMENTO DE GRANADA MUNICIPIO DE GRANADA

Planta de Ubicacion Sin Escala

Numero: Numero Catastral: 3051-4-05-086-17403

DERROTERO

LINEA	RUMBO	DIST	COORD UTM
1-2	S29°57'52"W	11.30	16P 612732.14, 1318170.61
2-3	S54°46'40"E	16.82	16P 612726.50, 1318160.83
3-4	N29°17'52"E	8.91	16P 612740.24, 1318151.13
4-5	N46°06'20"W	7.96	16P 612744.60, 1318158.90
5-1	N47°18'53"W	9.14	16P 612738.86, 1318164.42

Área:169.3984 m² =240.2772 Vrs²

Objeto Lev: Verificación de Área	Número Catastral: 3051-4-05-086-17403	FIRMA:
Propietario: Ramón Enrique Solorzano Defunción: Tomo: 10005, Folio: 198, Partida: 198	Ubicacion: Costado suroriental del cementerio municipal de Granada, de la primera entrada al reparto El Escudo 103.24m al noreste. Municipio de Granada, Depto. de Granada	Ejecuta: Ing.Bosco Javier Morgan Lic. Catastral: BMM100426 Cel: 8883-7568 Email: ingmorgan73@gmail.com SERVICIOS TOPOGRAFICOS
Solicitante: Nubia Isabel Loza Soza Ced: 443-201057-0000D	Área:169.3984 m² =240.2772 Vrs² — Escala:1 / 500	Fecha: 17 de Junio del 2025

ESPACIO PARA ESQUELA