


## MUNICIPIO DE NANDAIME. DEPARTAMENTO DE GRANADA

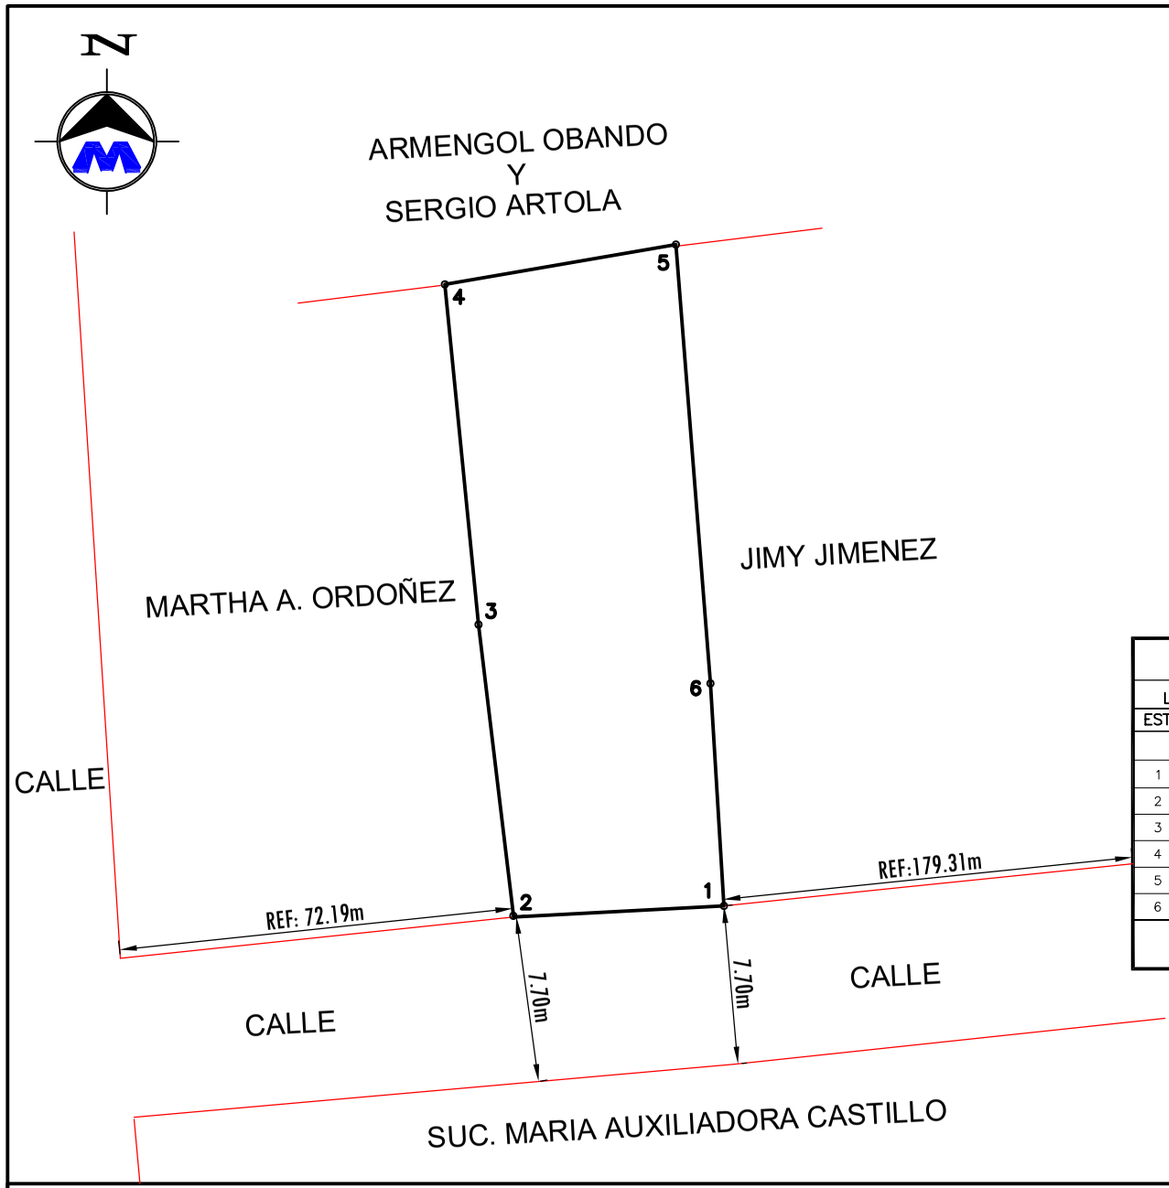


Planta de Ubicacion Sin Escala
Número Catastral: 2951-2-08-083-05701

COORDENADAS NO VINCULADAS A LA RED GEODESICA DE NICARAGUA

### CUADRO DE CONSTRUCCION

| LADO EST | LADO PV | RUMBO | DISTANCIA | V | COORDENADAS Y | COORDENADAS X |
|---|---|---|---|---|---|---|
| | | | | 1 | 1,299,949.2500 | 603,730.8200 |
| 1 | 2 | S 86°59'13.96" W | 7.61 | 2 | 1,299,948.8500 | 603,723.2200 |
| 2 | 3 | N 06°51'04.76" W | 10.65 | 3 | 1,299,959.4200 | 603,721.9500 |
| 3 | 4 | N 05°39'52.09" W | 12.36 | 4 | 1,299,971.7200 | 603,720.7300 |
| 4 | 5 | N 80°13'36.38" E | 8.48 | 5 | 1,299,973.1600 | 603,729.0900 |
| 5 | 6 | S 04°28'03.79" E | 15.92 | 6 | 1,299,957.2900 | 603,730.3300 |
| 6 | 1 | S 03°29'15.34" E | 8.05 | 1 | 1,299,949.2500 | 603,730.8200 |

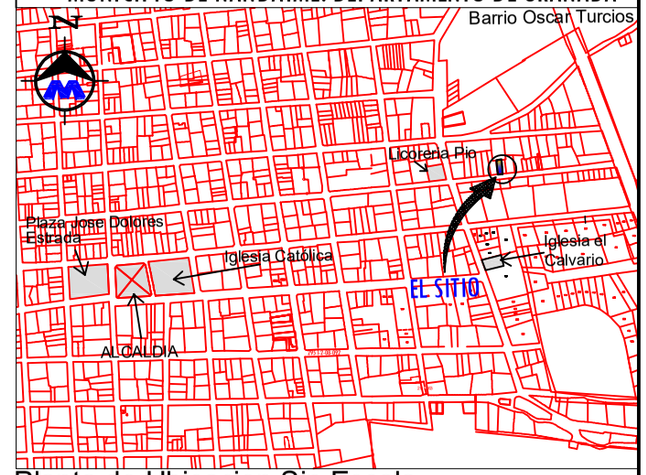**SUPERFICIE: 191.05 m2 = 270.99 Vrs2**

| | | |
|---|---|---|
| Objeto Lev: Mensura Judicial | Número Catastral: 2951-2-08-083-05701 | FIRMA: |
| Propeitarios: Octavio Antonio Marquez Mena<br>Cédula: 401-040805-1013J<br>Joel Humberto Marquez Mena<br>Ced:561-030704-1005E | Ubicación: Barrio Oscar Turcios de la iglesia El Calvario 2c norte 1/2c Este.Municipio de Nandaime. Departamento. Granada. | Ejecuta: Ing.Bosco Javier Morgan<br>Lic. Catastral: BMM100426<br>Cel: 8883-7568 Email: ingmorgan73@gmail.com<br>SERVICIOS TOPOGRAFICOS |
| Factor de Escala:1.418415 | Area: 191.05 m2 = 270.99 vrs2 — Escala: 1 / 250 | Fecha: 17 de Junio del 2025 |

ESPACIO PARA ESQUELA