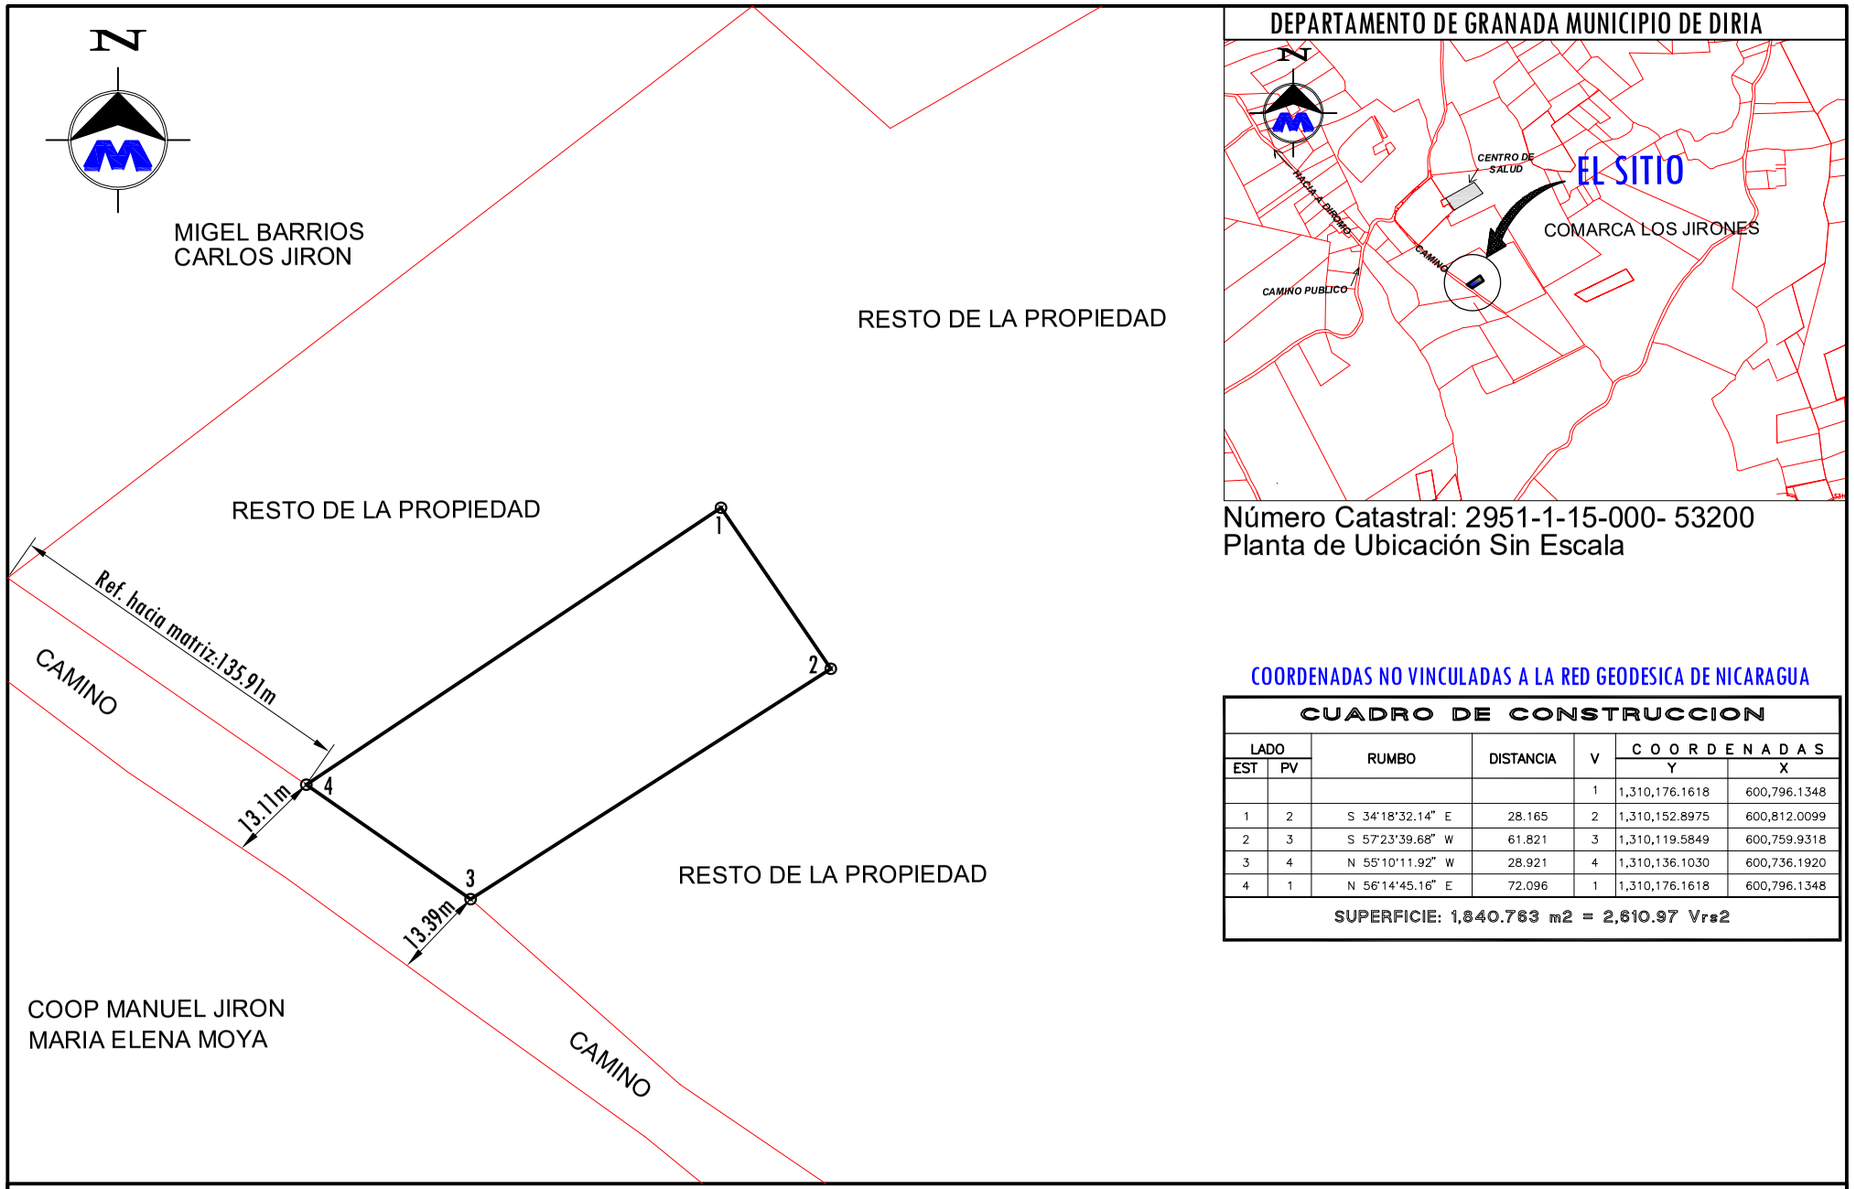

DEPARTAMENTO DE GRANADA MUNICIPIO DE DIRIA

Número Catastral: 2951-1-15-000- 53200
Planta de Ubicación Sin Escala

COORDENADAS NO VINCULADAS A LA RED GEODESICA DE NICARAGUA

CUADRO DE CONSTRUCCION

LADO EST	LADO PV	RUMBO	DISTANCIA	V	COORDENADAS Y	COORDENADAS X
				1	1,310,176.1618	600,796.1348
1	2	S 34°18'32.14" E	28.165	2	1,310,152.8975	600,812.0099
2	3	S 57°23'39.68" W	61.821	3	1,310,119.5849	600,759.9318
3	4	N 55°10'11.92" W	28.921	4	1,310,136.1030	600,736.1920
4	1	N 56°14'45.16" E	72.096	1	1,310,176.1618	600,796.1348

SUPERFICIE: 1,840.763 m2 = 2,610.97 Vrs2

ESPACIO PARA ESQUELA

Objeto Lev: Desmembración	Número Catastral: 2951-1-15-000- 53200	FIRMA:
Enajenante: Rosa Lucia Jaen Moya Ced: 204-060864-0001R	Ubicación: Cmca. Los Jirones, del Centro de salud 250 Vrs al S. Municipio de Diria, Departamento de Granada.	Ejecuta: Ing.Bosco Javier Morgan Lic. Catastral: BMM100426 Cel: 8883-7568 Email: ingmorgan73@gmail.com servicios topograficos
Adquiriente: Lilliam Montenegro Rodriguez Ced: 569-180964-1000H	Área: 1,840.763 m² = 2,610.97 Vrs² — Escala: 1 / 1000	Fecha: 27 de Junio 2025