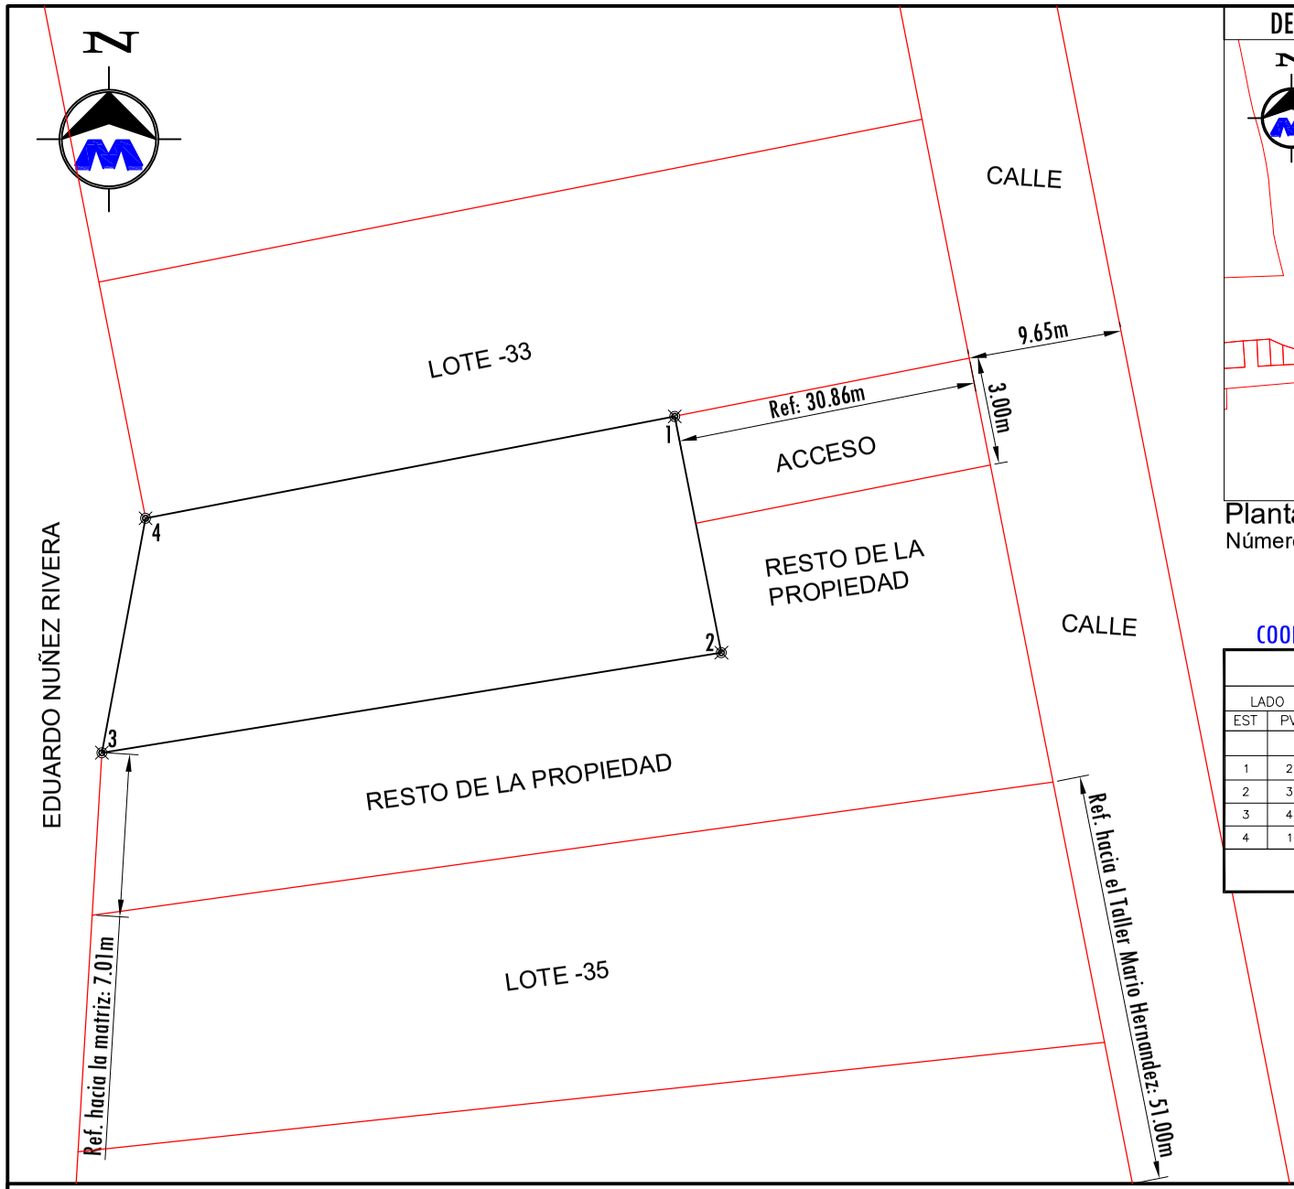

DEPARTAMENTO DE GRANADA MUNICIPIO DE GRANADA

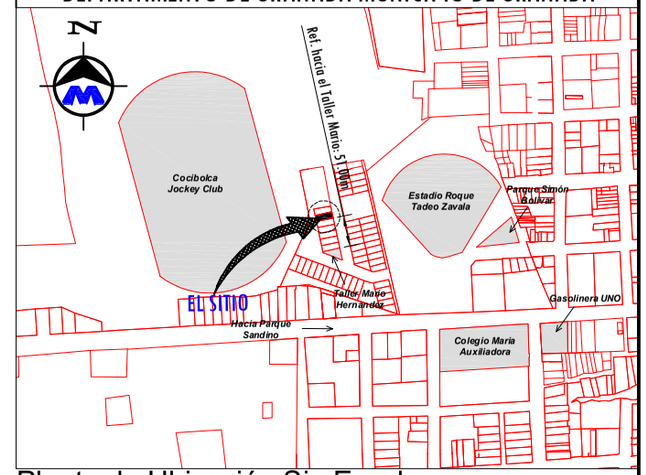

Planta de Ubicación Sin Escala
Número Catastral: 3051-4-05-056-08700

COORDENADAS NO VINCULADAS A LA RED GEODESICA DE NICARAGUA

CUADRO DE CONSTRUCCION

LADO EST	LADO PV	RUMBO	DISTANCIA	V	COORDENADAS Y	COORDENADAS X
				1	1,319,898.0542	612,619.1792
1	2	S 11°10'34.67" E	6.972	2	1,319,891.2145	612,620.5305
2	3	S 80°50'12.17" W	18.141	3	1,319,888.3256	612,602.6208
3	4	N 10°32'12.64" E	6.894	4	1,319,895.1038	612,603.8816
4	1	N 79°04'59.99" E	15.579	1	1,319,898.0542	612,619.1792

SUPERFICIE = 113.186 m2 = 160.54 Vrs2

ESPACIO PARA ESQUELA

Objeto Lev: Donación Parcial	Número Catastral: 3051-4-05-056-08700	FIRMA:
Enajenante: Rosa Aleyda Mendieta Centeno Ced: 203-290973-0002H	Ubicación: Del Taller Mario Hernandez 51.00m al Norte. Municipio de Granada, Departamento de Granada.	Ejecuta: Ing.Bosco Javier Morgan Lic. Catastral: BMM100426 Cel: 8883-7568 Email: ingmorgan73@gmail.com SERVICIOS TOPOGRAFICOS
Adquiriente: José Francisco Zambrana Gorgona, Ced: 201-170549-0002B Candy Fatima Herrera, Pasaporte: 642392597	Área: 113.186 m² = 160.54 Vrs² — Escala: 1 /200	Fecha: 19 de Enero del 2026