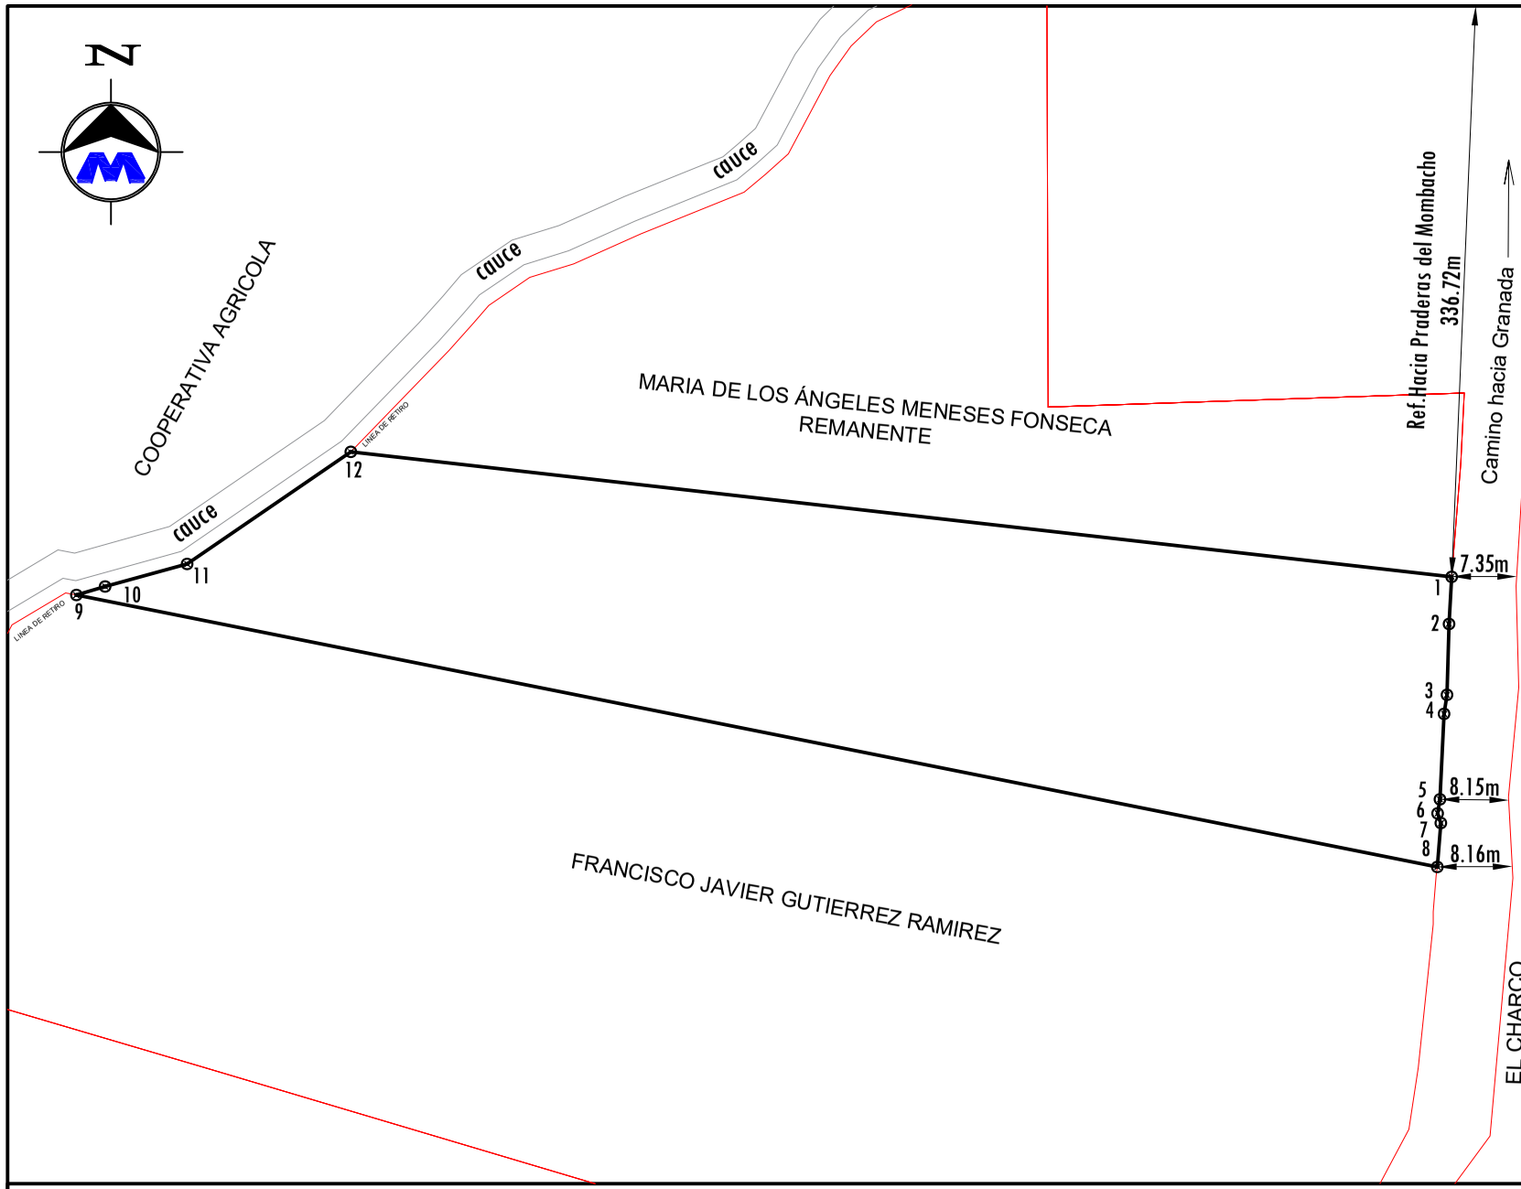

DEPARTAMENTO DE GRANADA MUNICIPIO DE GRANADA

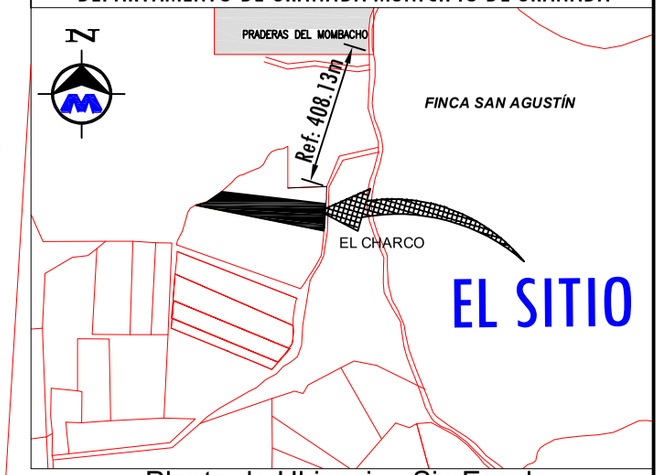

Planta de Ubicacion Sin Escala
Número Catastral:3051-4-09-000-05908

COORDENADAS NO VINCULADAS A LA RED GEODESICA DE NICARAGUA

CUADRO DE CONSTRUCCION

LADO EST	LADO PV	RUMBO	DISTANCIA	V	COORDENADAS Y	COORDENADAS X
				1	1,315,644.9011	613,705.0281
1	2	S 03°17'58.48" W	11.619	2	1,315,633.3010	613,704.3594
2	3	S 01°41'04.74" W	17.452	3	1,315,615.8569	613,703.8463
3	4	S 08°20'05.33" W	4.725	4	1,315,611.1815	613,703.1613
4	5	S 02°45'41.93" W	21.038	5	1,315,590.1676	613,702.1477
5	6	S 09°44'31.75" W	3.481	6	1,315,586.7370	613,701.5587
6	7	S 18°30'44.31" E	2.555	7	1,315,584.3137	613,702.3701
7	8	S 04°34'10.85" W	10.775	8	1,315,573.5731	613,701.5116
8	9	N 78°42'12.79" W	341.107	9	1,315,640.3909	613,367.0133
9	10	N 73°16'35.79" E	7.382	10	1,315,642.5152	613,374.0834
10	11	N 74°42'25.68" E	20.914	11	1,315,648.0313	613,394.2568
11	12	N 55°32'31.72" E	48.756	12	1,315,675.6172	613,434.4579
12	1	S 83°31'23.91" E	272.308	1	1,315,644.9011	613,705.0281

SUPERFICIE = 17,625.090 m2 = 1.76 HECTAREAS = 2.50 MNZ

Objeto Lev: Venta Parcial-Desmembracion	Número Catastral:3051-4-09-000-05908	Fecha: 15 de Enero del 2025	FIRMA:
Propietario: Maria de los Ángeles Meneses Fonseca c.c. Maria de los Ángeles Meneses Fonseca de Caldera CED- 201-120548-0002V	Ubicación:Finca San Agustin, del Residencial Las Praderas del Mombacho 336.72 m al suroeste. Municipio de Granada. Departamento de Granada.	Ejecuta: Ing.Bosco Javier Morgan Lic. Catastral: BMM100426 Cel: 8883-7568 Email: ingmorgan73@gmail.com servicios topograficos	
Adquiere:CORNELIUS HOLZER,PHD Pasaporte: U 7986346	Area:17,625.090 m2 = 1.76 HECTAREAS = 2.50 MNZ	Escala: 1 / 1,700	