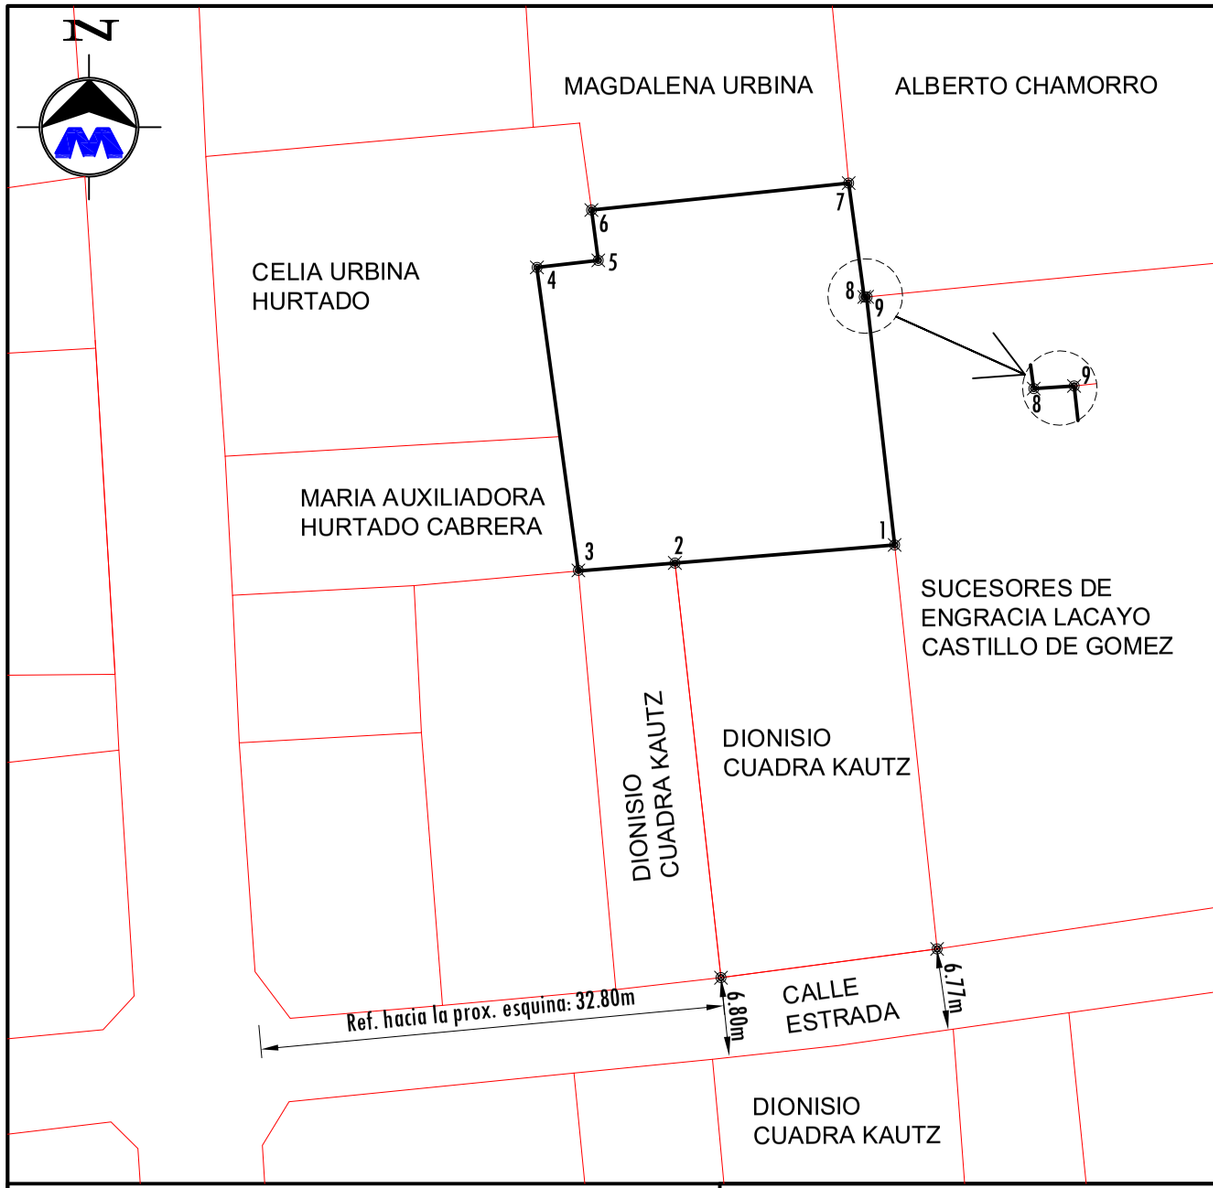

DEPARTAMENTO DE GRANADA MUNICIPIO DE GRANADA

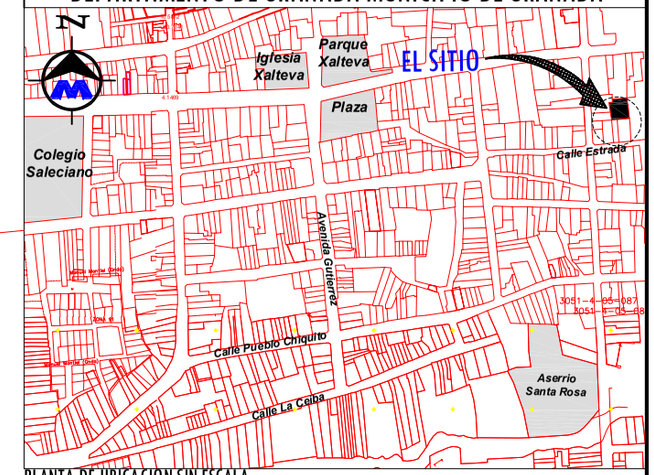

PLANTA DE UBICACION SIN ESCALA

Número Catastral: 3051-4-05-087-37700

COORDENADAS NO VINCULADAS AL SISTEMA NACIONAL DE COORDENADAS

CUADRO DE CONSTRUCCION

LADO EST	LADO PV	RUMBO	DISTANCIA	V	COORDENADAS Y	COORDENADAS X
				1	1,318,841.2021	613,586.5616
1	2	S 85°17'20.24" W	15.939	2	1,318,839.8930	613,570.6765
2	3	S 85°17'20.24" W	7.000	3	1,318,839.3181	613,563.7001
3	4	N 07°46'12.21" W	22.152	4	1,318,861.2662	613,560.7053
4	5	N 83°31'18.30" E	4.469	5	1,318,861.7704	613,565.1456
5	6	N 07°50'11.94" W	3.687	6	1,318,865.4232	613,564.6428
6	7	N 84°02'22.52" E	18.702	7	1,318,867.3651	613,583.2433
7	8	S 07°40'51.65" E	8.318	8	1,318,859.1218	613,584.3550
8	9	N 86°08'35.16" E	0.183	9	1,318,859.1341	613,584.5377
9	1	S 06°26'22.23" E	18.046	1	1,318,841.2021	613,586.5616

SUPERFICIE = 587.771 m2 = 833.70 Vrs2

Objeto Lev: Verificación de área	Número Catastral: 3051-4-05-087-37700		FIRMA:
Propietario: Dionisio Cuadra Kautz Ced: 201-101035-0000S	Ubicación: Iglesia Xalteva 2c al Este, 1c al Sur y 32.80m al Este Municipio de Granada, Departamento de Granada.		Ejecuta: Ing.Bosco Javier Morgan Lic. Catastral: BMM 100426 Celular: 8883-7568 SERVICIOS TOPOGRAFICOS
Factor de escala: 1.418415	Área= 587.771 m2 = 833.70 Vrs2	Escala: 1 /500	Fecha: 26 de Enero del 2026

ESPACIO PARA ESQUELA