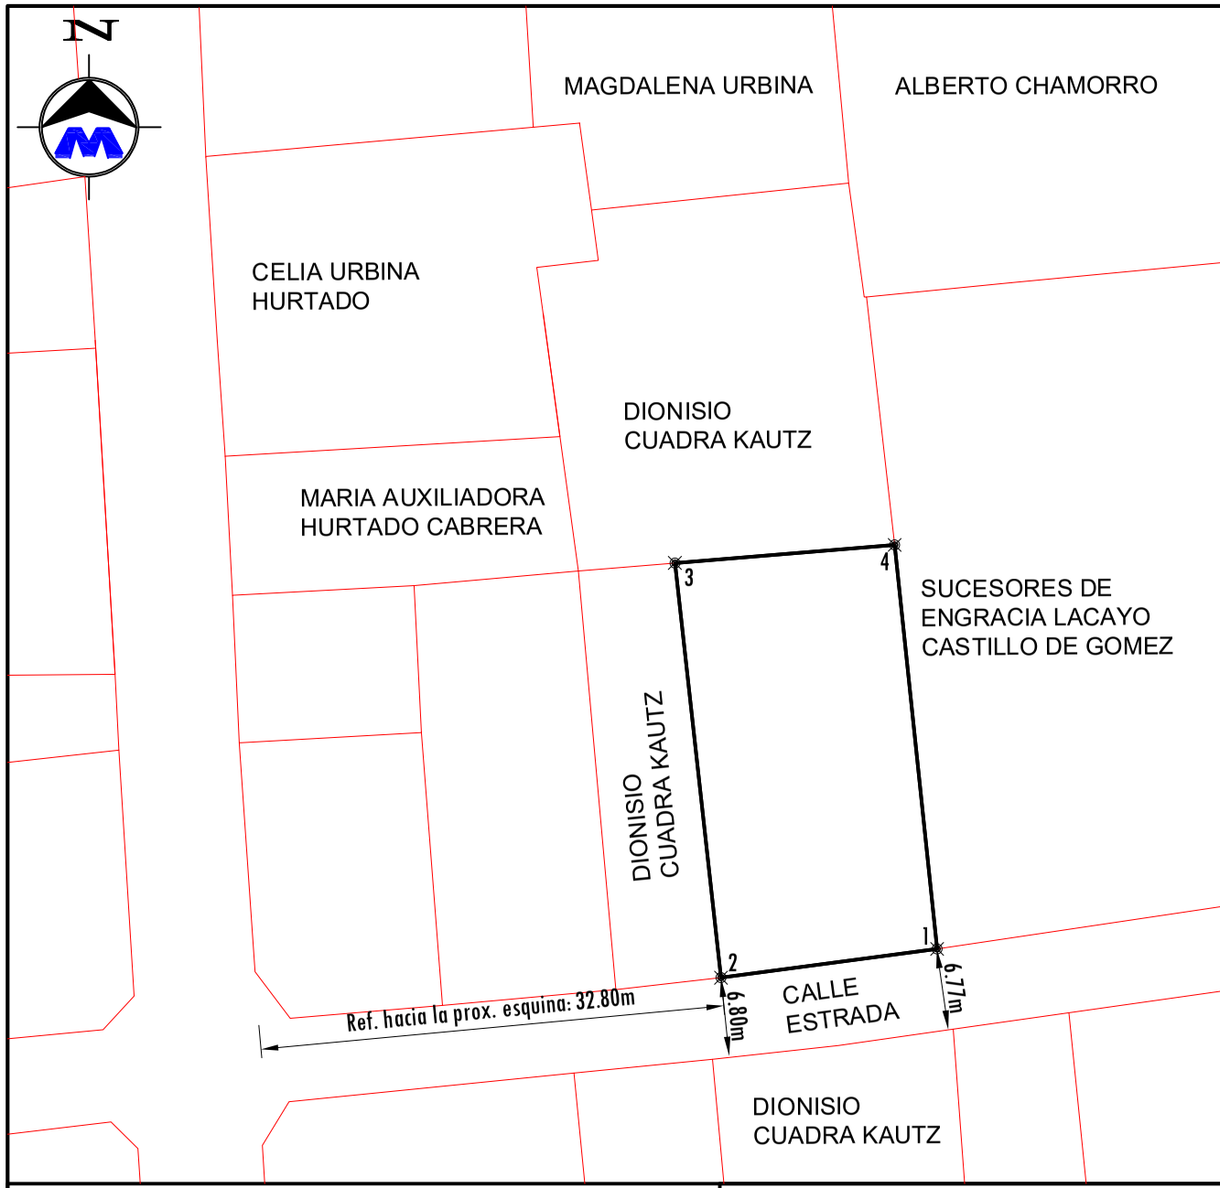

DEPARTAMENTO DE GRANADA MUNICIPIO DE GRANADA

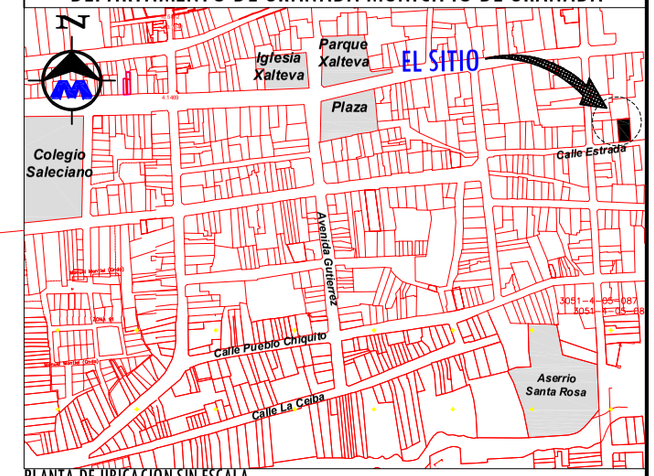

PLANTA DE UBICACION SIN ESCALA

Número Catastral: 3051-4-05-087-37700

COORDENADAS NO VINCULADAS AL SISTEMA NACIONAL DE COORDENADAS

CUADRO DE CONSTRUCCION

LADO EST	LADO PV	RUMBO	DISTANCIA	V	COORDENADAS Y	COORDENADAS X
				1	1,318,811.9776	613,589.6294
1	2	S 82°24'24.34" W	15.753	2	1,318,809.8960	613,574.0142
2	3	N 06°20'56.87" W	30.182	3	1,318,839.8930	613,570.6765
3	4	N 85°17'20.24" E	15.939	4	1,318,841.2021	613,586.5616
4	1	S 05°59'33.50" E	29.385	1	1,318,811.9776	613,589.6294

SUPERFICIE = 471.803 m2 = 669.21 Vrs2

Objeto Lev: Verificación de área	Número Catastral: 3051-4-05-087-37700		FIRMA:
Propietario: Dionisio Cuadra Kautz Ced: 201-101035-0000S	Ubicación: Iglesia Xalteva 2c al Este, 1c al Sur y 32.80m al Este Municipio de Granada, Departamento de Granada.		Ejecuta: Ing.Bosco Javier Morgan Lic. Catastral: BMM 100426 Celular: 8883-7568 SERVICIOS TOPOGRAFICOS
Factor de escala: 1.418415	Área= 471.803 m2 = 669.21 Vrs2	Escala: 1 /500	Fecha: 26 de Enero del 2026

ESPACIO PARA ESQUELA