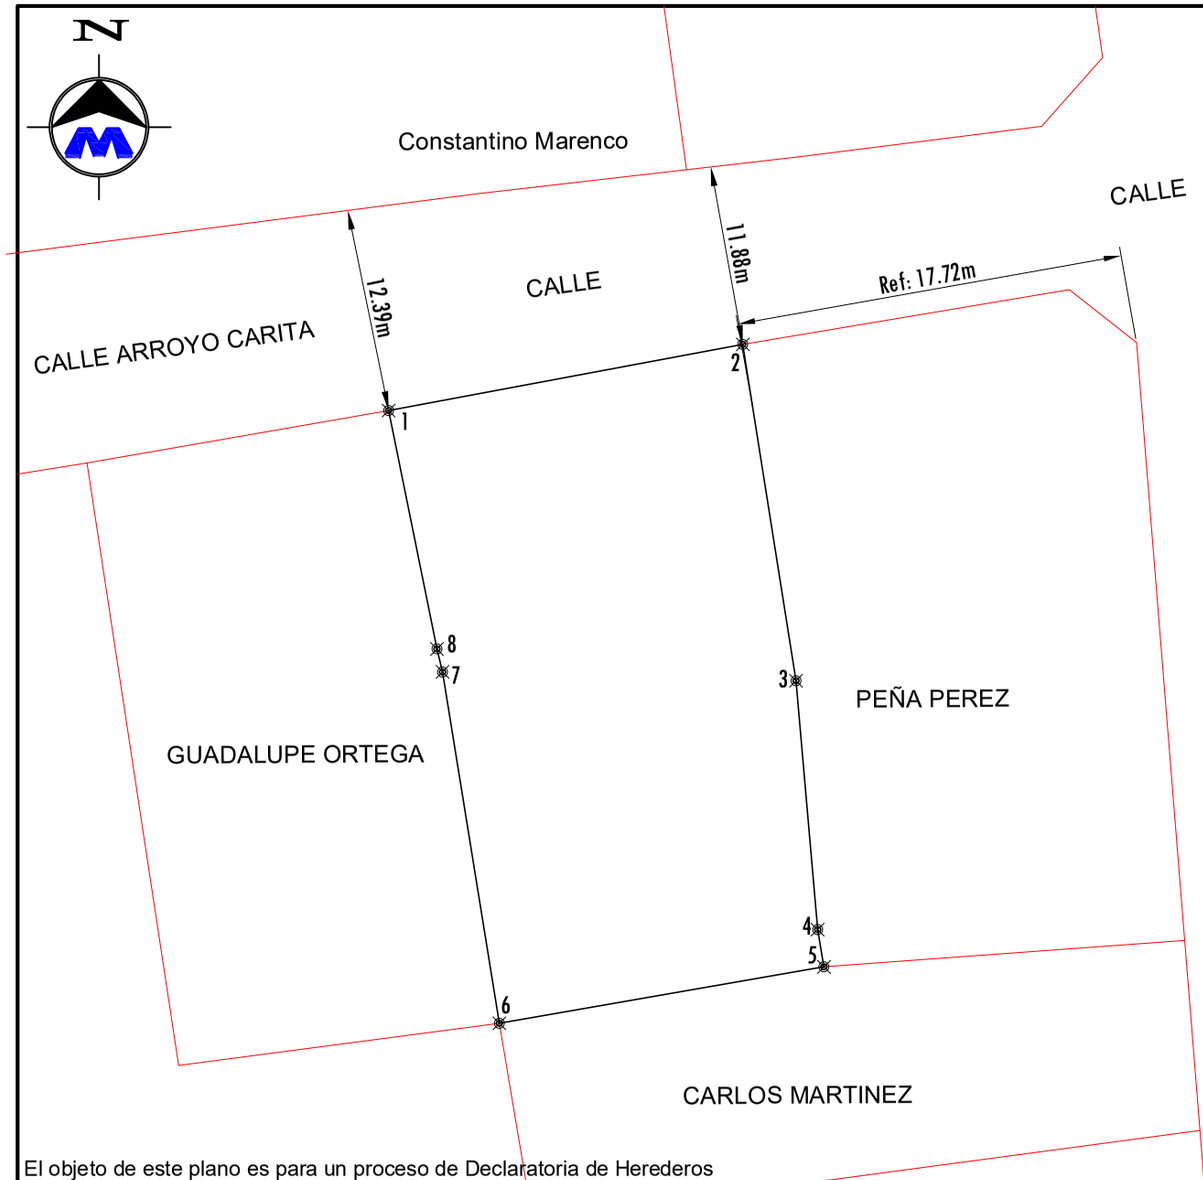

El objeto de este plano es para un proceso de Declaratoria de Herederos

DEPARTAMENTO DE GRANADA MUNICIPIO DE GRANADA

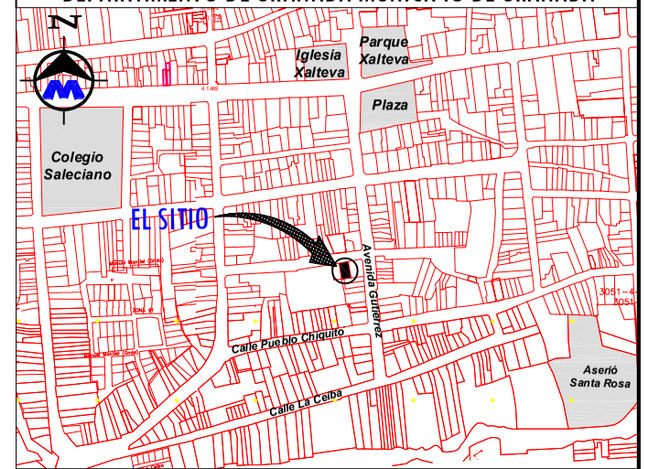

PLANTA DE UBICACIÓN SIN ESCALA

Número Catastral: 3051-4-05-087-01903

COORDENADAS NO VINCULADAS AL SISTEMA NACIONAL DE COORDENADAS

CUADRO DE CONSTRUCCION

LADO EST	LADO PV	RUMBO	DISTANCIA	V	COORDENADAS Y	COORDENADAS X
				1	1,318,648.5261	613,164.1039
1	2	N 79°24'55.43" E	11.719	2	1,318,650.6787	613,175.6232
2	3	S 08°58'53.35" E	11.079	3	1,318,639.7358	613,177.3528
3	4	S 04°56'29.56" E	8.135	4	1,318,631.6315	613,178.0535
4	5	S 09°46'01.28" E	1.229	5	1,318,630.4199	613,178.2620
5	6	S 80°07'51.48" W	10.716	6	1,318,628.5832	613,167.7048
6	7	N 09°11'51.86" W	11.588	7	1,318,640.0227	613,165.8524
7	8	N 13°12'15.83" W	0.765	8	1,318,640.7671	613,165.6778
8	1	N 11°27'59.14" W	7.917	1	1,318,648.5261	613,164.1039

SUPERFICIE = 228.729 m2 =324.43 Vrs2

ESPACIO PARA ESQUELA

Objeto Lev: Verificación de área	Número Catastral: 3051-4-05-087-37700		FIRMA:
Propietario: Miguel Angel Abea Bravo Certificado de defunción Tomo: 82 Folio: 156 Partida: 312 Conocido registralmente como Miguel Angel Abea	Ubicación: Iglesia Xalteva 2c al Sur, 17.78 m al O. Calle Arroyo Carita. Municipio de Granada, Departamento de Granada.		Ejecuta: Ing.Bosco Javier Morgan Lic. Catastral: BMM 100426 Celular: 8883-7568 SERVICIOS TOPOGRAFICOS
Solicitante: Pedro Jose Abea Collado Ced: 201-080444-0005F	Área= 228.729 m² = 324.43 vrs²	Escala: 1 /300	Fecha: 21 de Enero del 2026