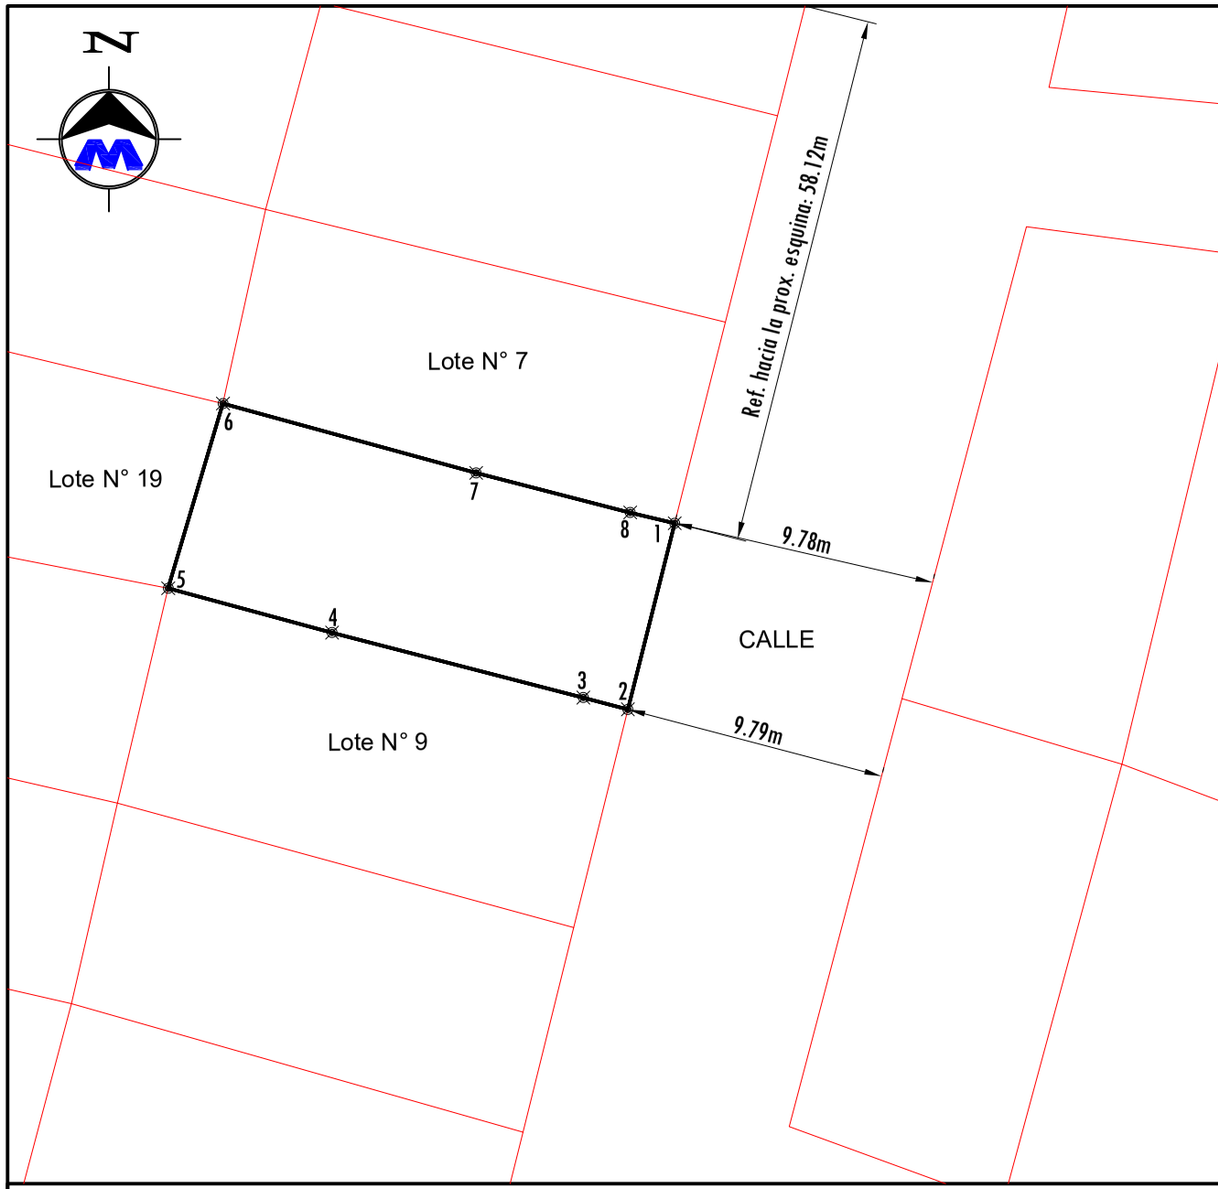

DEPARTAMENTO DE GRANADA MUNICIPIO DE GRANADA

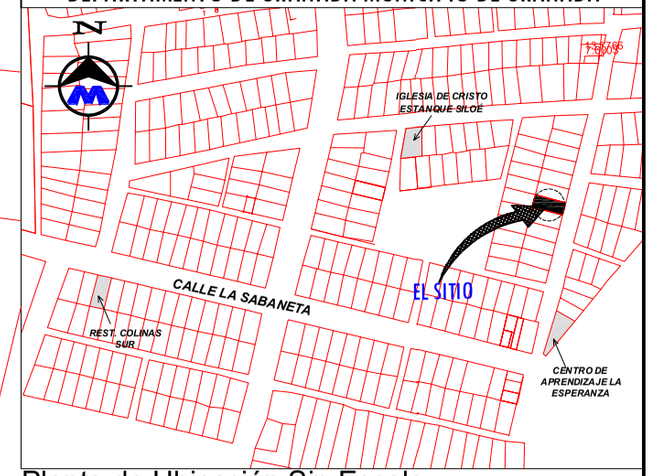

Planta de Ubicación Sin Escala
Número Catastral: 3051-4-05-089-12400

COORDENADAS NO VINCULADAS A LA RED GEODESICA DE NICARAGUA

CUADRO DE CONSTRUCCION

LADO EST	LADO PV	RUMBO	DISTANCIA	V	COORDENADAS Y	COORDENADAS X
				1	1,318,390.1467	614,442.6338
1	2	S 14°08'43.70" W	8.331	2	1,318,382.0686	614,440.5979
2	3	N 75°15'14.51" W	2.001	3	1,318,382.5778	614,438.6630
3	4	N 75°28'55.41" W	11.251	4	1,318,385.3983	614,427.7712
4	5	N 74°52'25.79" W	7.364	5	1,318,387.3200	614,420.6620
5	6	N 16°30'17.83" E	8.364	6	1,318,395.3394	614,423.0382
6	7	S 74°38'59.01" E	11.389	7	1,318,392.3244	614,434.0214
7	8	S 75°35'01.97" E	6.893	8	1,318,390.6082	614,440.6975
8	1	S 76°35'29.72" E	1.991	1	1,318,390.1467	614,442.6338

SUPERFICIE = 169.908 m2 = 241.00 Vrs2

Objeto Lev: Compraventa total	Número Catastral: 3051-4-05-089-12400		FIRMA:
Enajenante: Isabelita del Carmen Arcia Noguera, Ced: 042-120152-0002H Pedro José Sandino Mendoza, Ced: 201-071047-0001W	Ubicación:Rpto Eddy Ruiz, del Restaurante Colinas Sur 3c E, 75 vrs al Norte. Municipio de Granada, Departamento de Granada.		Ejecuta: Ing.Bosco Javier Morgan Lic. Catastral: BMM100426 Cel: 8883-7568 Email: ingmorgan73@gmail.com SERVICIOS TOPOGRAFICOS
Adquiriente: Giovannia Auxiliadora Wellington Alonso, Ced: 201-250681-0002B	Área: 169.908 m2 = 241.00 Vrs2	Escala: 1 /300	Fecha: 21 de Enero del 2026

ESPACIO PARA ESQUELA