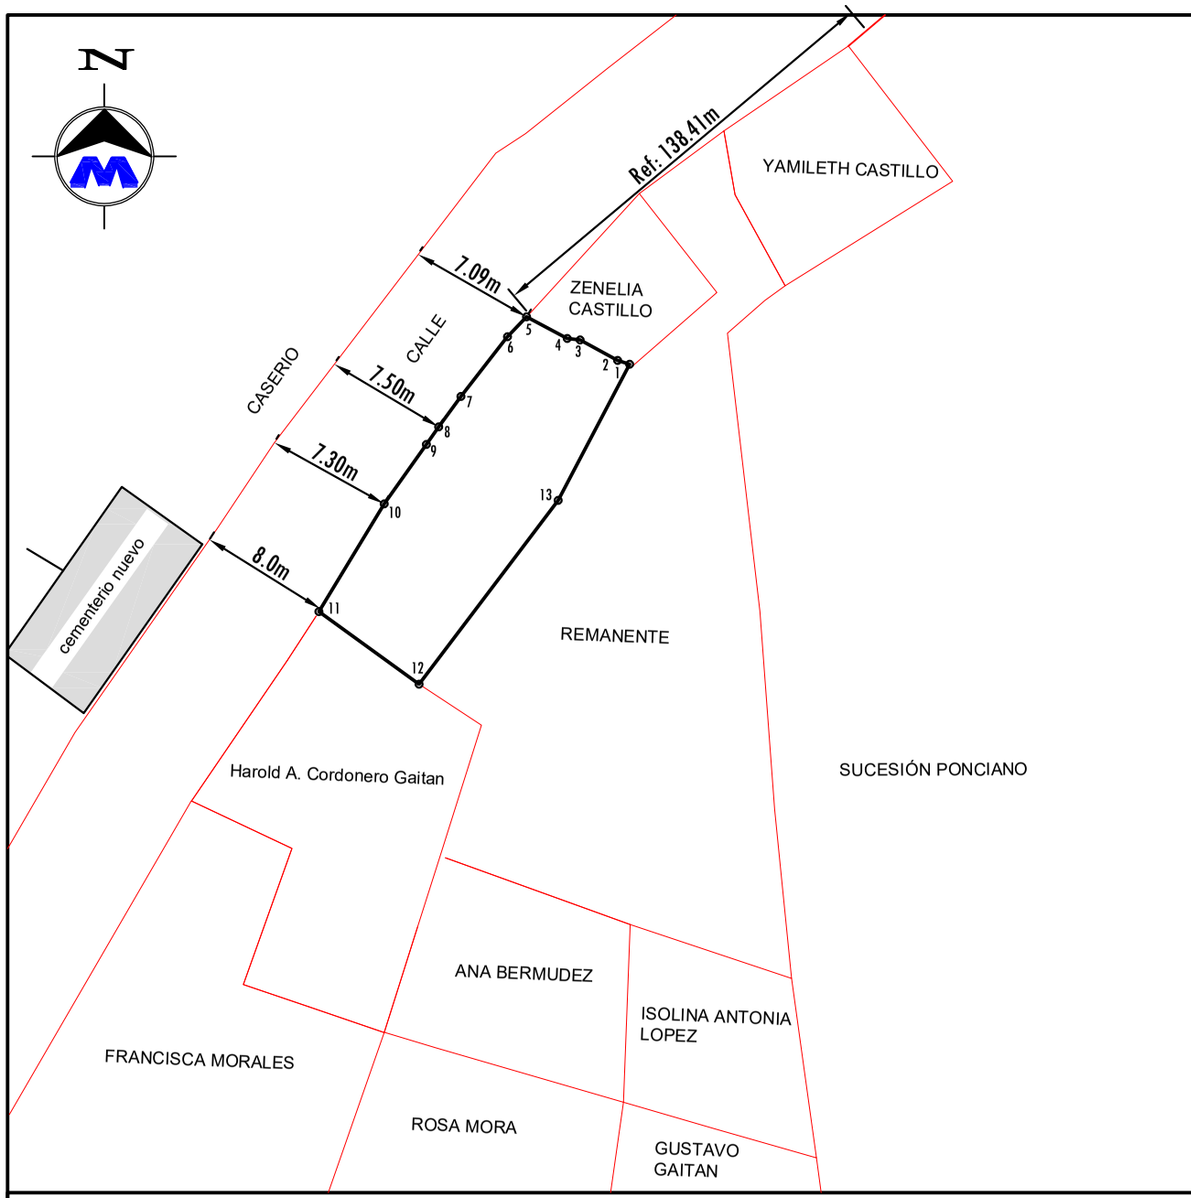

DEPARTAMENTO DE GRANADA MUNICIPIO DE GRANADA

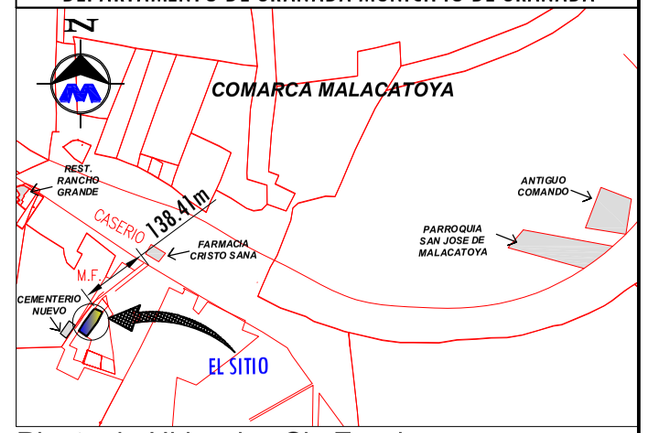

Planta de Ubicacion Sin Escala

Numero Catastral: 3052-3-03-000-02850

COORDENADAS NO VINCULADAS A LA RED GEODESICA DE NICARAGUA

CUADRO DE CONSTRUCCION

LADO EST	LADO PV	RUMBO	DISTANCIA	V	COORDENADAS Y	COORDENADAS X
				1	1,343,094.0944	626,180.8838
1	2	N 71°20'47.25" W	1.807	2	1,343,094.6722	626,179.1722
2	3	N 61°30'52.56" W	6.199	3	1,343,097.6286	626,173.7239
3	4	N 83°19'54.65" W	1.886	4	1,343,097.8476	626,171.8509
4	5	N 61°56'47.43" W	6.624	5	1,343,100.9626	626,166.0056
5	6	S 43°50'36.47" W	4.161	6	1,343,097.9617	626,163.1234
6	7	S 37°49'43.27" W	10.775	7	1,343,089.4512	626,156.5151
7	8	S 36°28'56.63" W	5.466	8	1,343,085.0565	626,153.2654
8	9	S 34°21'21.47" W	3.080	9	1,343,082.5139	626,151.5273
9	10	S 35°25'10.60" W	10.555	10	1,343,073.9122	626,145.4099
10	11	S 31°11'16.61" W	18.234	11	1,343,058.3131	626,135.9672
11	12	S 54°10'51.85" E	17.882	12	1,343,047.8479	626,150.4675
12	13	N 37°05'09.18" E	33.302	13	1,343,074.4138	626,170.5489
13	1	N 27°42'19.39" E	22.229	1	1,343,094.0944	626,180.8838

SUPERFICIE = 1,019.312 m2 = 1,445.80 Vrs2

ESPACIO PARA ESQUELA

Objeto Lev: Venta Parcial - Desmembracion	Número Catastral: 3052-3-03-000-02850	FIRMA:
Enajenante: Isaura del Carmen Castillo Ced: 201-280559-0003W	Ubicación: Del Antiguo Comando 1 1/2c Este y 184.69m al Sur. Frente al Cementerio Nuevo Comarca de Malacatoya. Municipio de Granada. Depto de Granada.	Ejecuta: Ing.Bosco Javier Morgan Lic. Catastral: BMM100426 Cel: 8883-7568 Email: ingmorgan73@gmail.com servicios topograficos
Adquiriente: Ana Lopez Bermudez Ced: 201-240263-0004X	Área: 1,019.312 m2=1,445.80 vrs2 — Escala: 1 / 1000	Fecha: 20 de Enero del 2026