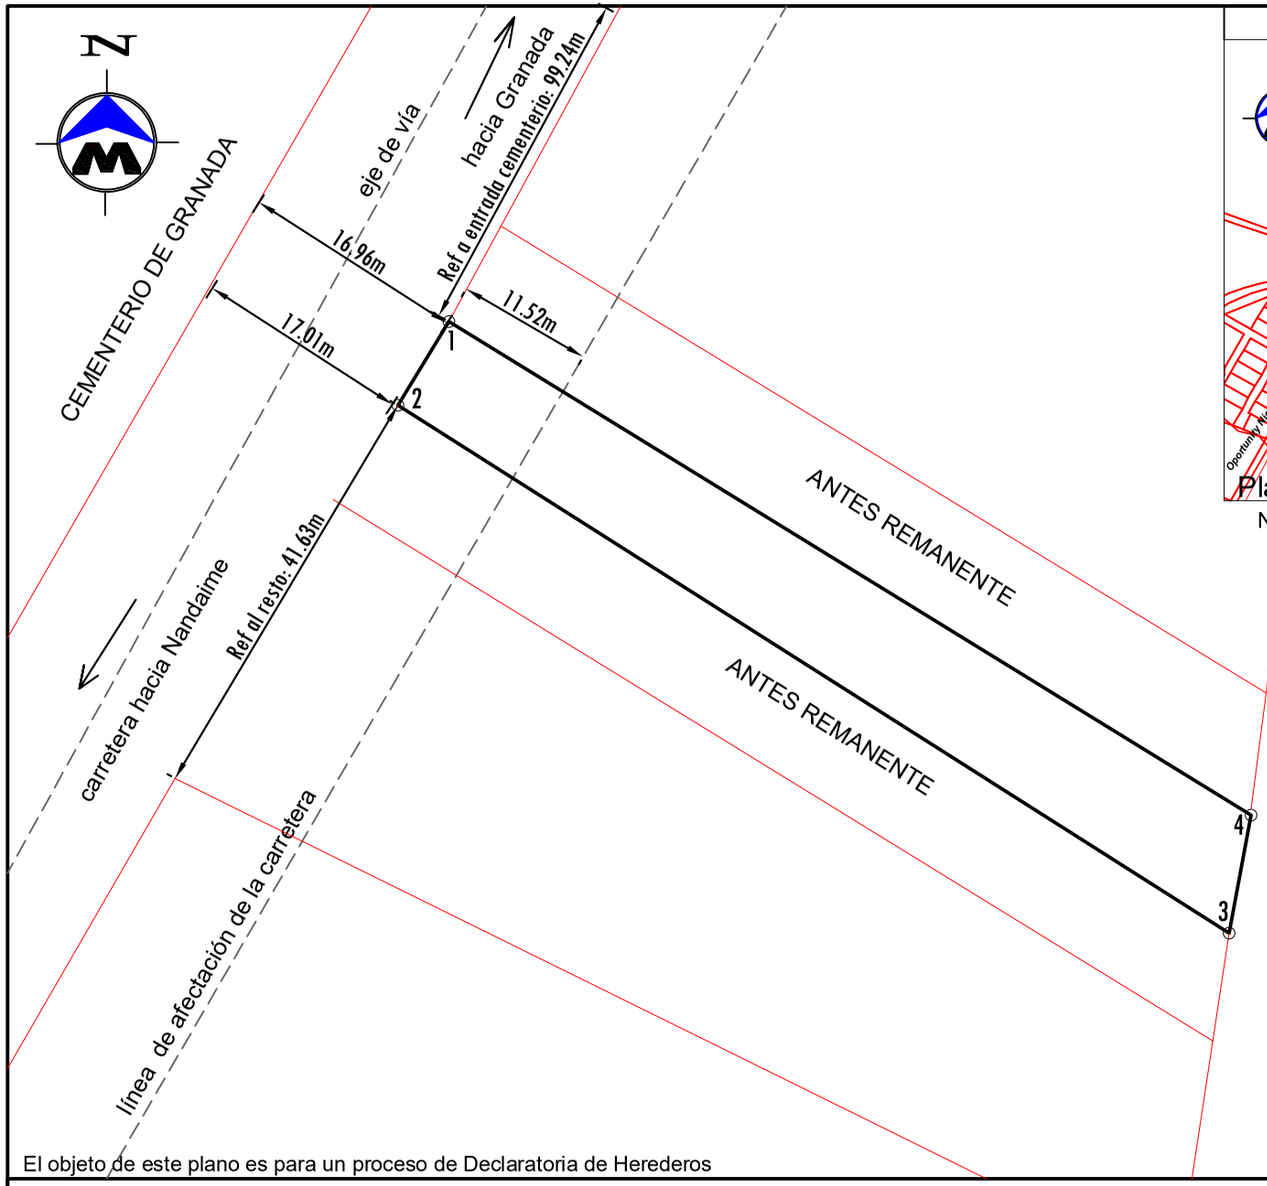

Planta de Ubicacion Sin Escala

Numero: Numero Catastral: 3051-4-05-086-17405

COORDENADAS NO VINCULADAS A LA RED GEODESICA DE NICARAGUA

CUADRO DE CONSTRUCCION

LADO EST	LADO PV	RUMBO	DISTANCIA	V	COORDENADAS Y	COORDENADAS X
				1	1,318,203.7307	612,759.7107
1	2	S 31°24'24.61" W	7.097	2	1,318,197.6732	612,756.0122
2	3	S 57°34'28.71" E	71.186	3	1,318,159.5030	612,816.1000
3	4	N 10°32'26.55" E	8.686	4	1,318,168.0423	612,817.6889
4	1	N 58°23'08.53" W	68.082	1	1,318,203.7307	612,759.7107

SUPERFICIE = 528.474 m2 = 749.60 Vrs2

El objeto de este plano es para un proceso de Declaratoria de Herederos

Objeto Lev: Verificación de Área	Numero: Numero Catastral: 3051-4-05-086-17405		Fecha: 20 de Enero del 2026
Propietario: Maria de Jesus Gonzalez Guadamuz Cedula: 201-130749-1000Q conocida registralmente como Maria de Jesús Gonzalez de Malespin	Ubicacion: De la entrada principal del cementerio municipal de Granada 99.24m al suroeste sobre la carretera Granada - Nandaime Municipio de Granada, Depto. de Granada		Ejecuta: Ing.Bosco Javier Morgan Lic. Catastral: BMM100426 Cel: 8883-7568 Email: ingmorgan73@gmail.com SERVICIOS TOPOGRAFICOS
	Area: 528.474 m2 = 749.60 Vrs2	Escala: 1 / 500	FIRMA:

ESPACIO PARA ESQUELA