


## MUNICIPIO DE NINDIRI. DEPARTAMENTO DE MASAYA

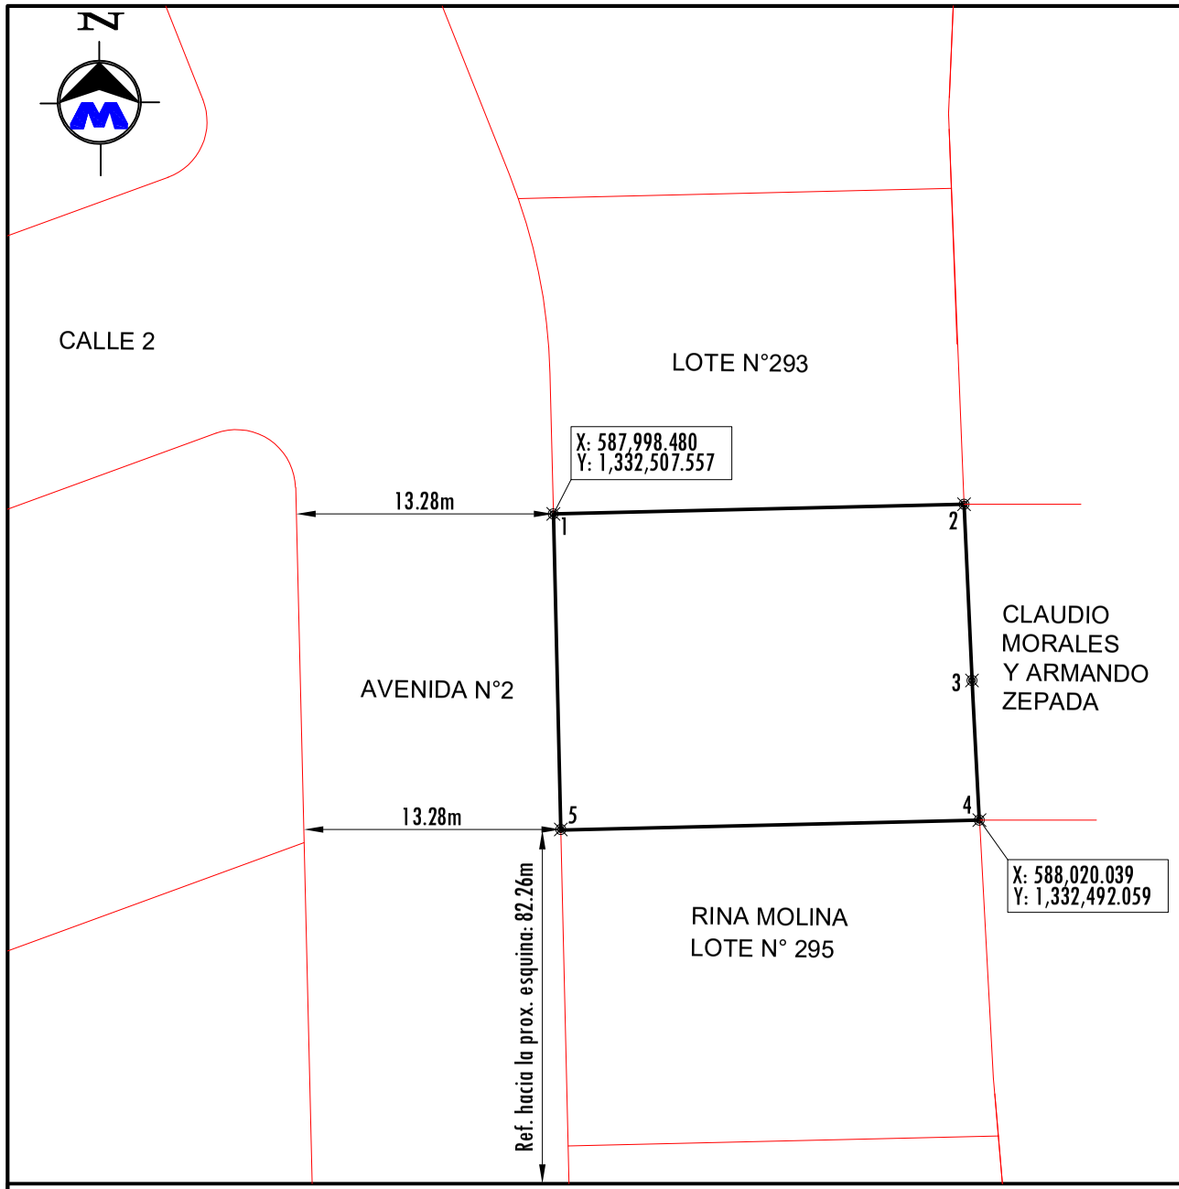


PLANTA DE UBICACION SIN ESCALA

Numero Catastral: 2952-2-09-080-14200

### COORDENADAS NO VINCULADAS A LA RED GEODESICA DE NICARAGUA

**CUADRO DE CONSTRUCCION**
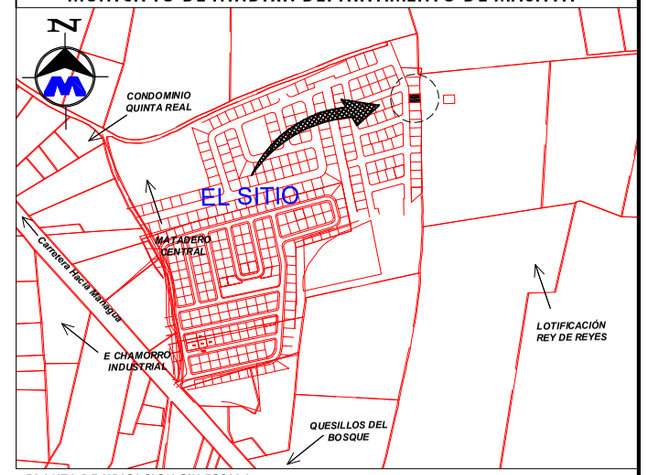
| LADO EST | LADO PV | RUMBO | DISTANCIA | V | COORDENADAS Y | COORDENADAS X |
|---|---|---|---|---|---|---|
| | | | | 1 | 1,332,507.557 | 587,998.480 |
| 1 | 2 | N 88°39'17.87" E | 20.79 | 2 | 1,332,508.045 | 588,019.264 |
| 2 | 3 | S 02°34'30.04" E | 9.73 | 3 | 1,332,498.328 | 588,019.701 |
| 3 | 4 | S 03°05'10.24" E | 6.28 | 4 | 1,332,492.059 | 588,020.039 |
| 4 | 5 | S 88°39'21.69" W | 21.19 | 5 | 1,332,491.562 | 587,998.855 |
| 5 | 1 | N 01°20'34.96" W | 16.00 | 1 | 1,332,507.557 | 587,998.480 |

**SUPERFICIE = 335.555 m2 = 475.96 Vrs2**

| | | | |
|---|---|---|---|
| Objeto: Transcripción por testamento abierto | Número Catastral: 2952-2-09-080-14200 | | FIRMA: |
| Enajenante:<br>Yamilet del Carmen Gaitan Alvarado (q.e.p.d.)<br>Certificado de defunción Tomo:10032 Folio:152 Partida:152 | Ubicación: Del Km 14 Entrada a Veracruz 914m al N-E , Entrada a Urbanización Bosques Campistrano y anexo a Valle Campistrano, Lote 294. Municipio de Nindiri, Departamento de Masaya. | | Ejecuta: Ing.Bosco Javier Morgan<br>Lic. Catastral: BMM100426<br>Cel: 8883-7568 Email: ingmorgan73@gmail.com<br>www.morganconstrucciones.com |
| Adquiriente: Maria del Carmen Alvarado Guzman<br>Ced: 001-040245-0019Q | Área = 335.555 m2 = 475.96 Vrs2 | Escala: 1: 350 | Fecha: 17 de Enero del 2026 |

ESPACIO PARA ESQUELA