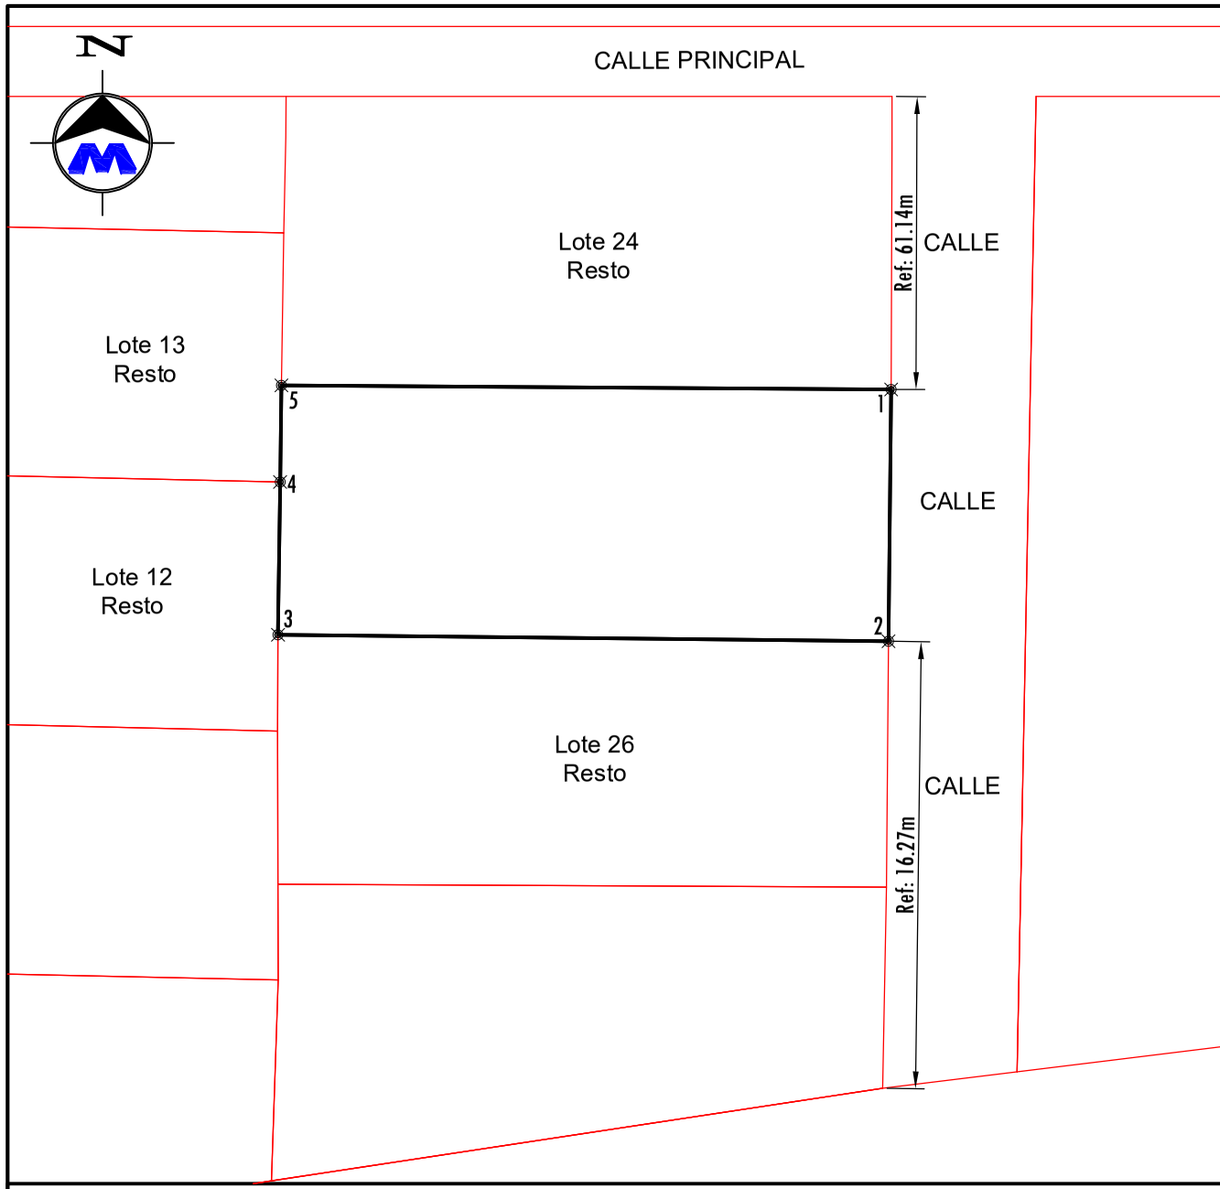

DEPARTAMENTO DE GRANADA MUNICIPIO DE GRANADA

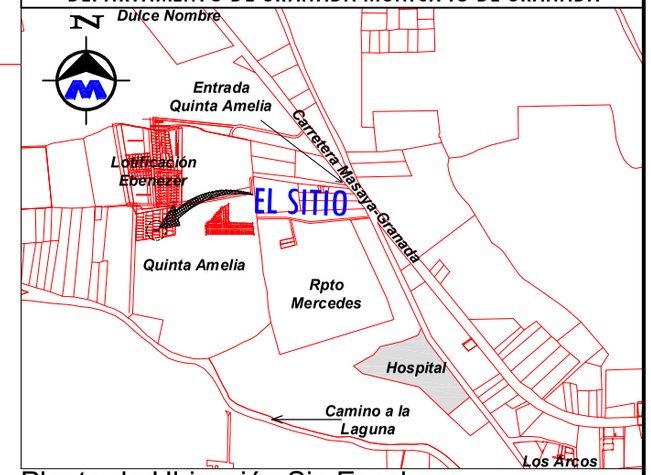

Planta de Ubicación Sin Escala

Número Catastral: 3051-4-05-000-04506

COORDENADAS NO VINCULADAS A LA RED GEODESICA DE NICARAGUA

CUADRO DE CONSTRUCCION

LADO EST	LADO PV	RUMBO	DISTANCIA	V	COORDENADAS Y	COORDENADAS X
				1	1,320,287.1907	610,582.1942
1	2	S 00°36'26.16" W	9.106	2	1,320,278.0848	610,582.0977
2	3	N 89°23'33.84" W	22.061	3	1,320,278.3186	610,560.0381
3	4	N 00°46'57.27" E	5.529	4	1,320,283.8473	610,560.1136
4	5	N 00°49'29.64" E	3.495	5	1,320,287.3424	610,560.1640
5	1	S 89°36'20.46" E	22.031	1	1,320,287.1907	610,582.1942

SUPERFICIE = 199.862 m2 = 283.48 Vrs2

Objeto Lev: Venta Parcial (Desmembración)	Número Catastral: 3051-4-05-000-04506			FIRMA:	SELLO
Enajenante: Francisco Javier Pedreira Pardo Ced: edit	Ubicación: Cmca. La Laguna, costado Sur Rpto Ebenezer, calle por medio 61.14m al Sur, Lote 25. Municipio de Granada Departamento de Granada.			Ejecuta: Ing. Bosco Javier Morgan Lic. Catastral: BMM100426 Cel: 8883-7568 Email: ingmorgan73@gmail.com SERVICIOS TOPOGRAFICOS	
Adquiriente: Milton Javier Zavala Ced: 201-280604-1005R	Área: 199.862 m² = 283.48 Vrs²	Factor de escala: 1.418415	Escala: 1 /250	Fecha: 31 de Octubre del 2025	

ESPACIO PARA ESQUELA