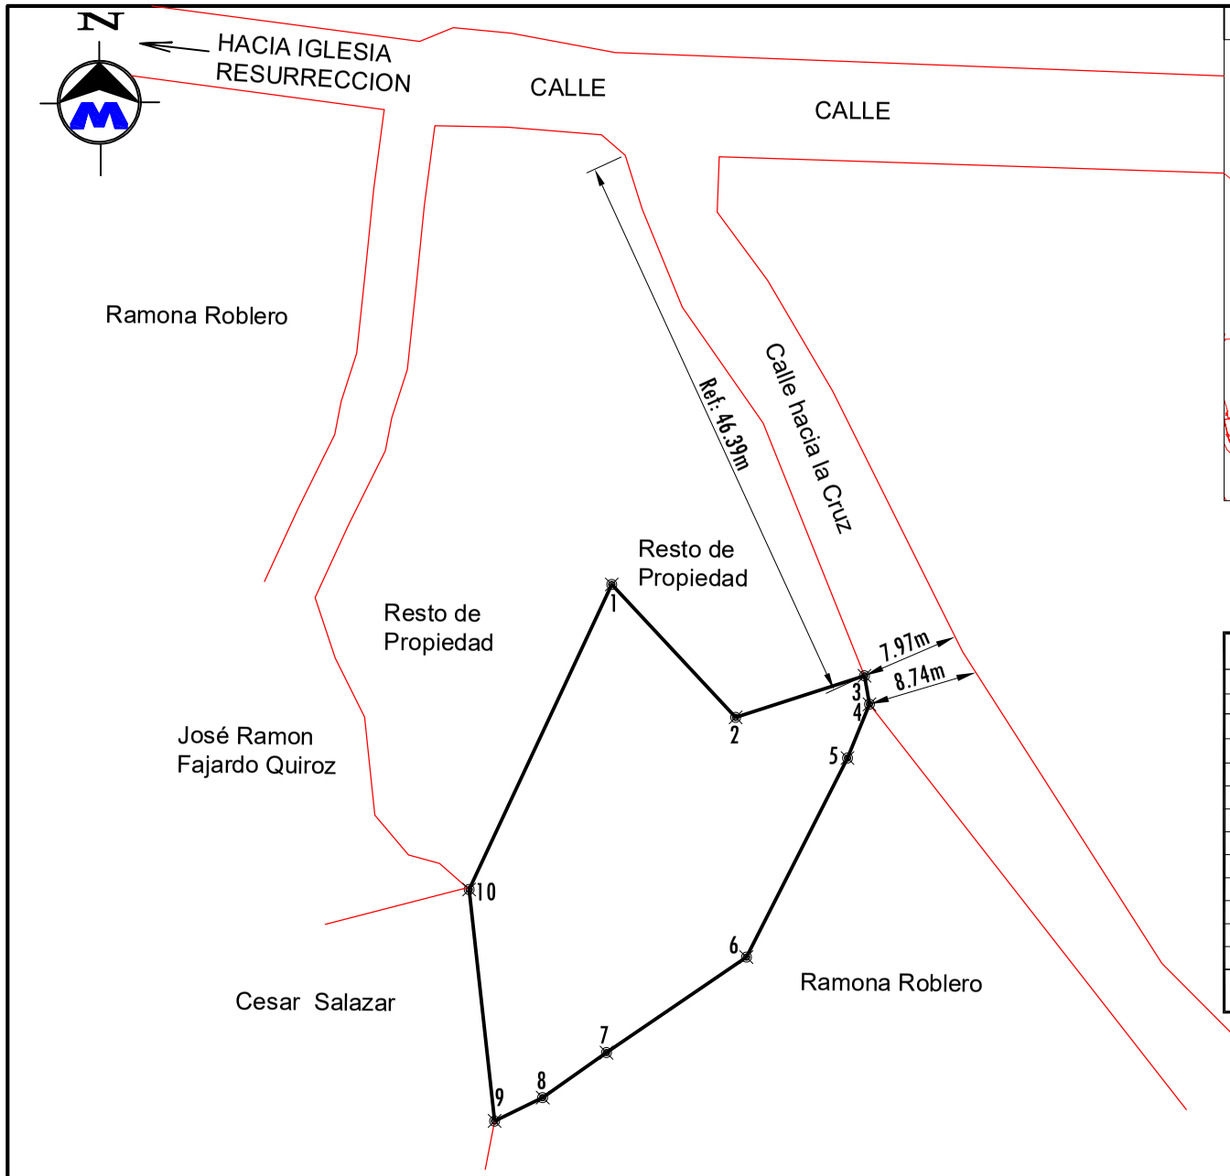

MUNICIPIO DE GRANADA. DEPARTAMENTO DE GRANADA

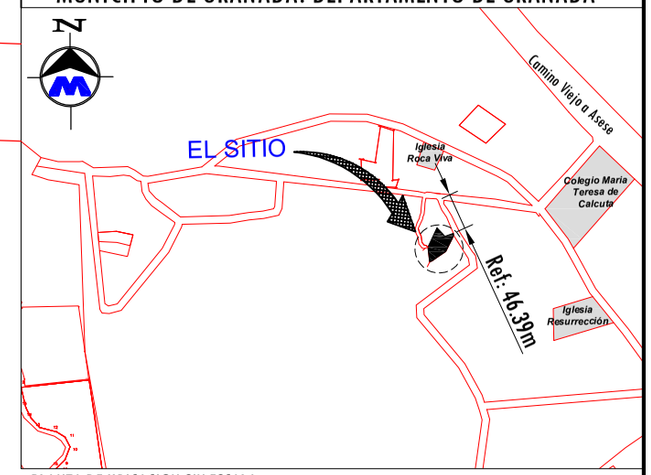

PLANTA DE UBICACION SIN ESCALA
Numero Catastral: 3051-4-09-000-MF

COORDENADAS NO VINCULADAS A LA RED GEODESICA DE NICARAGUA

CUADRO DE CONSTRUCCION

LADO EST	LADO PV	RUMBO	DISTANCIA	V	COORDENADAS Y	COORDENADAS X
				1	1,316,545.4586	614,628.0253
1	2	S 42°56'49.13" E	14.708	2	1,316,534.6927	614,638.0461
2	3	N 72°03'43.72" E	10.963	3	1,316,538.0690	614,648.4758
3	4	S 10°08'26.36" E	2.352	4	1,316,535.7533	614,648.8900
4	5	S 22°22'01.09" W	4.706	5	1,316,531.4018	614,647.0993
5	6	S 26°54'59.77" W	18.076	6	1,316,515.2840	614,638.9165
6	7	S 55°35'47.13" W	13.714	7	1,316,507.5355	614,627.6016
7	8	S 54°52'50.52" W	6.316	8	1,316,503.9019	614,622.4352
8	9	S 64°05'26.75" W	4.335	9	1,316,502.0077	614,618.5358
9	10	N 06°16'02.07" W	18.851	10	1,316,520.7463	614,616.4778
10	1	N 25°02'44.15" E	27.277	1	1,316,545.4586	614,628.0253

SUPERFICIE = 733.850 m2 = 1, 040.90 Vrs2

Objeto: Desmembración- Venta Parcial	Número Catastral: 3051-4-09-000-MF		FIRMA:
Enajenante: Entima Gertrudis Mora, Ced: 201-220452-0007U	Ubicación: Bo. Posintepe, Iglesia Resurrección 1c al N-O, 1c al O, 46.3m al Sur. Municipio de Granada, Departamento de Granada.		Ejecuta: Ing.Bosco Javier Morgan Lic. Catastral: BMM100426 Cel: 8883-7568 Email: ingmorgan73@gmail.com www.morganconstrucciones.com
Adquiriente: Oscar Danilo Sanchez Davila, Ced: 521-070398-0000N Disia Claribel Ramos Vivas, Ced: 201-260803-1009K	Área = 733.850 m2 = 1, 040.90 Vrs2	Escala: 1: 700	Fecha: 6 de Enero del 2026

ESPACIO PARA ESQUELA