


## DEPARTAMENTO DE GRANADA MUNICIPIO DE GRANADA

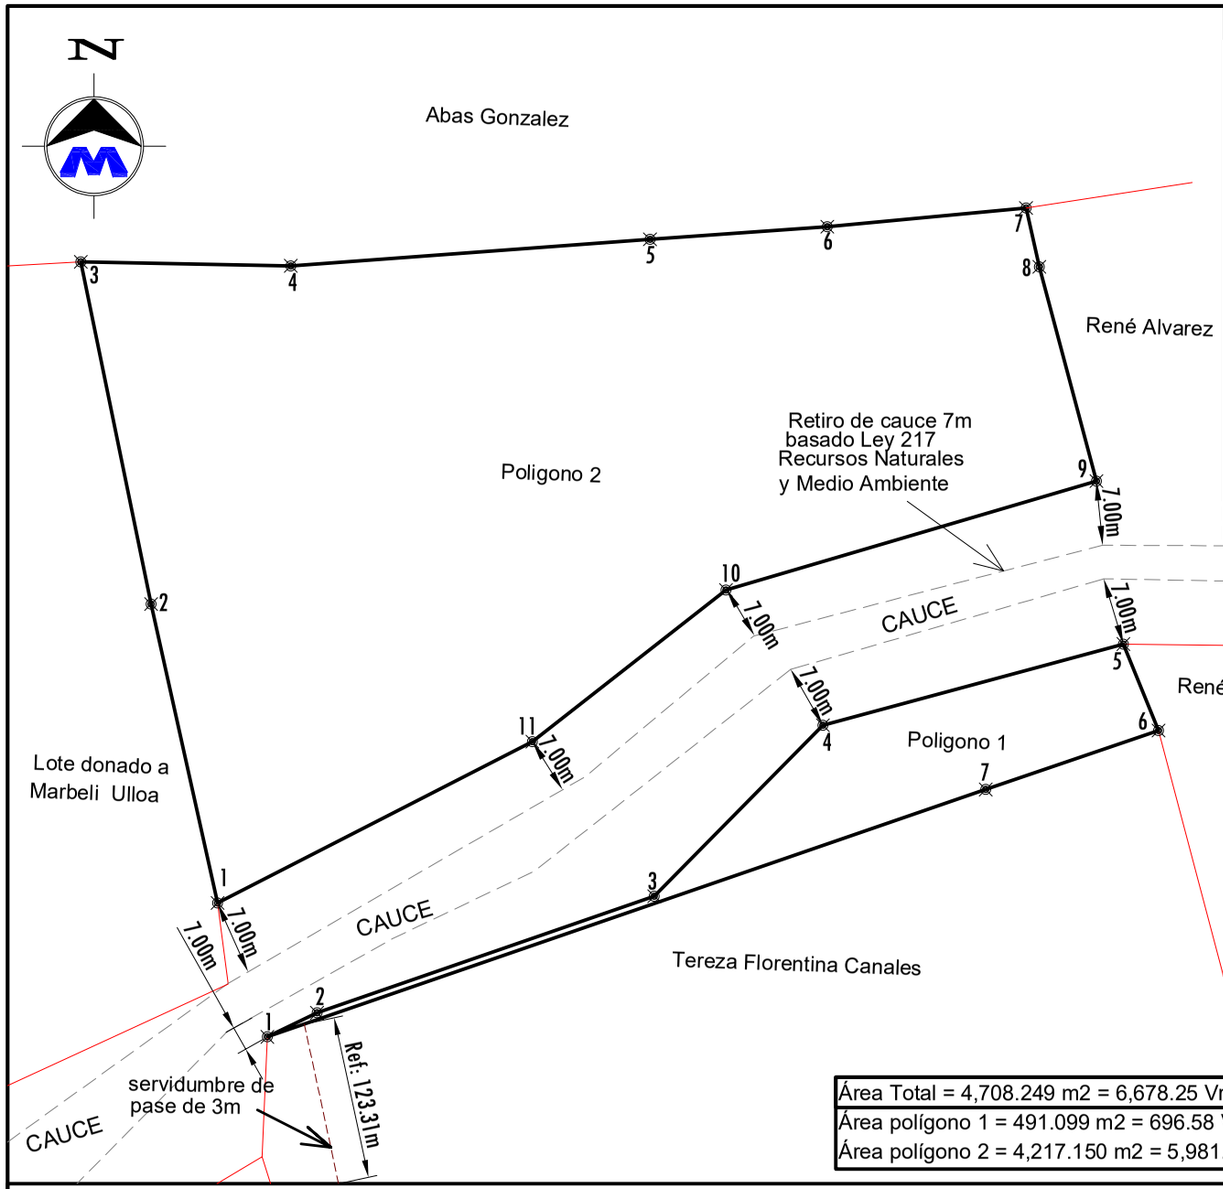


PLANTA DE UBICACIÓN SIN ESCALA
Número Catastral: 2951-1-08-000-23203

COORDENADAS NO VINCULADAS AL SISTEMA NACIONAL DE COORDENADAS

**CUADRO DE CONSTRUCCION POLIGONO "1"**

| LADO EST | LADO PV | RUMBO | DISTANCIA | V | COORDENADAS Y | COORDENADAS X |
|---|---|---|---|---|---|---|
| | | | | 1 | 1,321,152.2703 | 607,466.5443 |
| 1 | 2 | N 64°09'55.55" E | 5.578 | 2 | 1,321,154.7010 | 607,471.5648 |
| 2 | 3 | N 70°54'55.47" E | 36.122 | 3 | 1,321,166.5117 | 607,505.7018 |
| 3 | 4 | N 44°35'22.26" E | 24.315 | 4 | 1,321,183.8277 | 607,522.7714 |
| 4 | 5 | N 74°52'21.63" E | 31.489 | 5 | 1,321,192.0451 | 607,553.1691 |
| 5 | 6 | S 22°06'15.22" E | 9.458 | 6 | 1,321,183.2823 | 607,556.7280 |
| 6 | 7 | S 71°09'57.43" W | 18.483 | 7 | 1,321,177.3154 | 607,539.2346 |
| 7 | 1 | S 70°59'19.71" W | 76.884 | 1 | 1,321,152.2703 | 607,466.5443 |

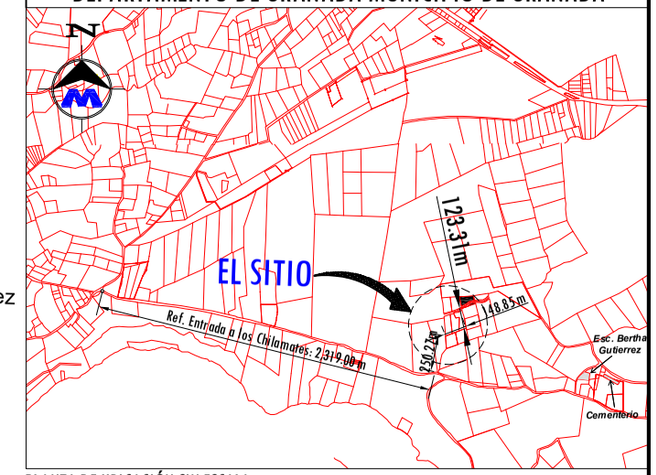**SUPERFICIE = 491.099 m2 = 696.58 Vrs2**

COORDENADAS NO VINCULADAS AL SISTEMA NACIONAL DE COORDENADAS

**CUADRO DE CONSTRUCCION POLIGONO 2**

| LADO EST | LADO PV | RUMBO | DISTANCIA | V | COORDENADAS Y | COORDENADAS X |
|---|---|---|---|---|---|---|
| | | | | 1 | 1,321,165.8197 | 607,461.4940 |
| 1 | 2 | N 12°29'58.57" W | 31.004 | 2 | 1,321,196.0887 | 607,454.7838 |
| 2 | 3 | N 11°37'02.35" W | 35.376 | 3 | 1,321,230.7397 | 607,447.6600 |
| 3 | 4 | S 88°55'17.33" E | 21.258 | 4 | 1,321,230.3396 | 607,468.9142 |
| 4 | 5 | N 85°46'18.83" E | 36.447 | 5 | 1,321,233.0268 | 607,505.2623 |
| 5 | 6 | N 85°58'18.88" E | 17.977 | 6 | 1,321,234.2896 | 607,523.1948 |
| 6 | 7 | N 84°34'36.56" E | 20.212 | 7 | 1,321,236.1998 | 607,543.3159 |
| 7 | 8 | S 12°44'06.12" E | 6.119 | 8 | 1,321,230.2314 | 607,544.6648 |
| 8 | 9 | S 14°55'25.28" E | 22.443 | 9 | 1,321,208.5450 | 607,550.4447 |
| 9 | 10 | S 73°35'58.44" W | 39.080 | 10 | 1,321,197.5108 | 607,512.9547 |
| 10 | 11 | S 51°54'54.68" W | 24.882 | 11 | 1,321,182.1627 | 607,493.3700 |
| 11 | 1 | S 62°51'19.80" W | 35.821 | 1 | 1,321,165.8197 | 607,461.4940 |

**SUPERFICIE = 4,217.150 m2 = 5,981.67 Vrs2**

| |
|---|
| Área Total = 4,708.249 m2 = 6,678.25 Vrs2 |
| Área polígono 1 = 491.099 m2 = 696.58 Vrs2 |
| Área polígono 2 = 4,217.150 m2 = 5,981.67 Vrs2 |

| | | | | |
|---|---|---|---|---|
| Objeto Lev: Verificación de área | Número Catastral: 2951-1-08-000-23203 | | FIRMA: | SELLO |
| Propietario: Julio René Alvarez Ayala<br>edit.<br>edit. | Ubicación: Entrada a Los Chilamate carretera Granada-Masaya 2,319 m SO, 250.27 m al NE, 148.85 m al E, 123.31 m al N. Comarca la Laguna #2. Lote A. Municipio de Granada. Departamento de Granada. | | Ejecuta: Ing.Bosco Javier Morgan<br>Lic. Catastral: BMM100426<br>SERVICIOS TOPOGRAFICOS | |
| Solicitante: edit.<br>Cedula: edit | Área = Indicada | Escala: 1 / 700 | Fecha: 08 de Enero del 2026 | |

ESPACIO PARA ESQUELA