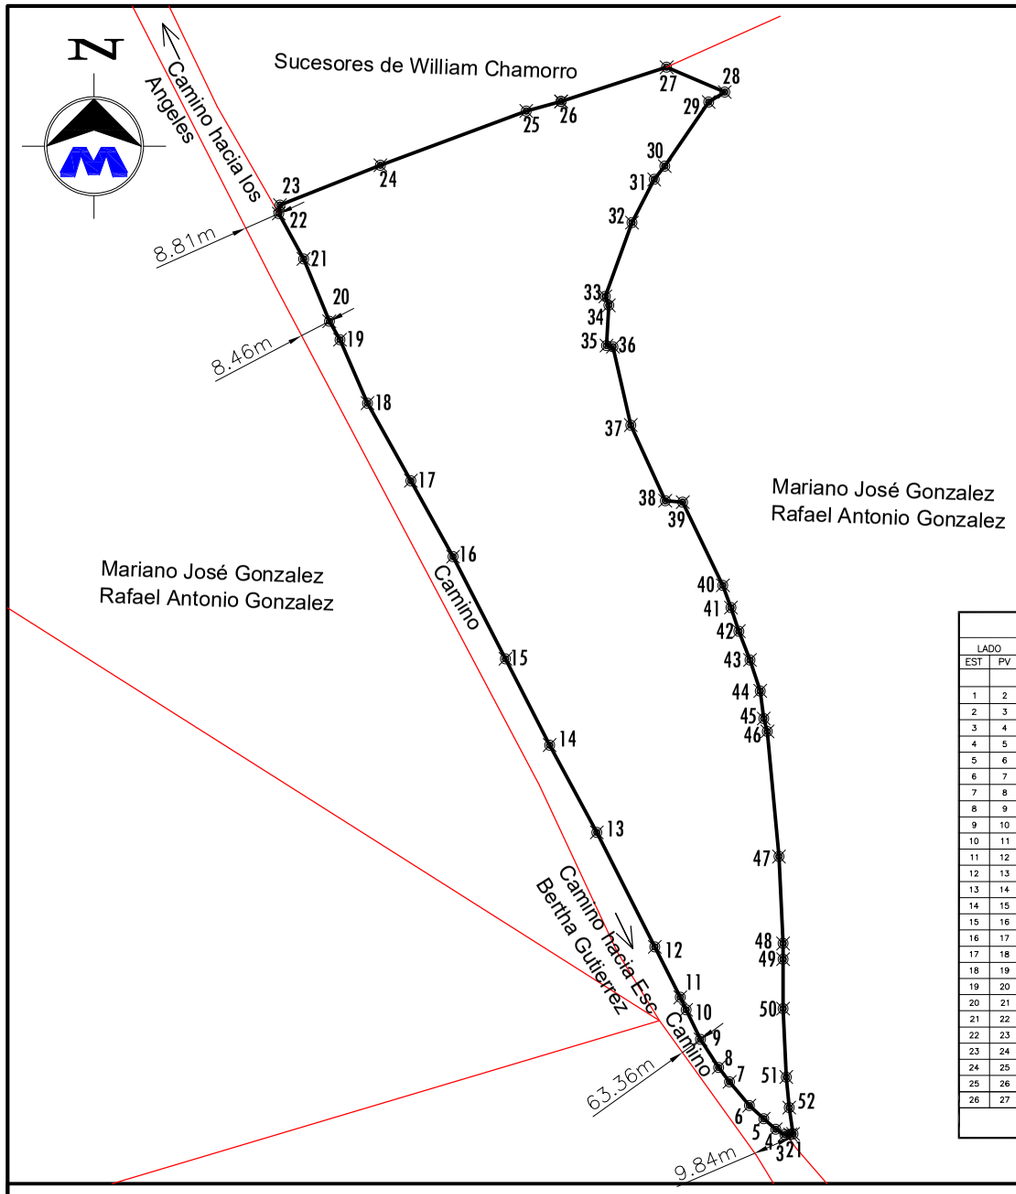

DEPARTAMENTO DE GRANADA MUNICIPIO DE GRANADA

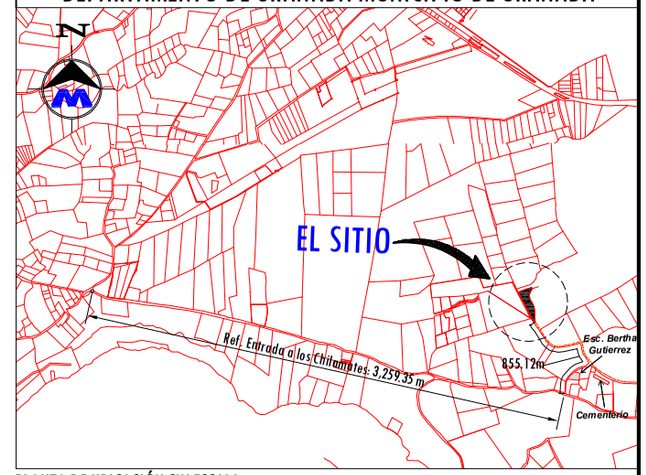

PLANTA DE UBICACIÓN SIN ESCALA
Número Catastral: 2951-1-08-000-24401

COORDENADAS NO VINCULADAS AL SISTEMA NACIONAL DE COORDENADAS

CUADRO DE CONSTRUCCION

LADO EST	LADO PV	RUMBO	DISTANCIA	V	COORDENADAS Y	COORDENADAS X	LADO EST	LADO PV	RUMBO	DISTANCIA	V	COORDENADAS Y	COORDENADAS X
				1	1,321,058.8387	608,024.8024	27	28	S 66°56'46.02" E	13.715	28	1,321,284.9358	608,009.9859
1	2	S 77°16'11.94" W	0.687	2	1,321,058.6872	608,024.1321	28	29	S 58°37'05.02" W	4.107	29	1,321,282.7969	608,006.4794
2	3	N 88°05'30.94" W	1.132	3	1,321,058.7249	608,023.0006	29	30	S 34°24'21.15" W	16.895	30	1,321,268.8579	607,996.9330
3	4	N 59°31'09.30" W	2.263	4	1,321,059.8728	608,021.0504	30	31	S 37°53'11.17" W	3.653	31	1,321,265.9748	607,994.6897
4	5	N 49°47'55.21" W	3.472	5	1,321,062.1137	608,018.3988	31	32	S 27°21'55.95" W	10.552	32	1,321,256.6034	607,989.8392
5	6	N 47°29'12.62" W	4.225	6	1,321,064.9684	608,015.2848	32	33	S 19°48'23.83" W	17.003	33	1,321,240.6059	607,984.0776
6	7	N 39°21'59.36" W	6.715	7	1,321,070.1598	608,011.0257	33	34	S 20°42'45.48" E	2.083	34	1,321,238.6576	607,984.8143
7	8	N 37°34'21.05" W	3.925	8	1,321,073.2709	608,008.6322	34	35	S 03°12'10.13" W	8.752	35	1,321,229.9193	607,984.3253
8	9	N 32°51'19.07" W	7.225	9	1,321,079.3399	608,004.7127	35	36	S 78°45'56.64" E	1.424	36	1,321,229.6419	607,985.7216
9	10	N 25°59'54.51" W	7.151	10	1,321,085.7672	608,001.5781	36	37	S 12°47'53.38" E	17.407	37	1,321,212.6673	607,989.5776
10	11	N 25°04'18.39" W	2.988	11	1,321,088.4732	608,000.3121	37	38	S 24°29'43.83" E	18.031	38	1,321,196.2590	607,997.0538
11	12	N 26°43'56.84" W	12.243	12	1,321,099.4076	607,994.8049	38	39	S 84°50'03.16" E	3.823	39	1,321,195.9148	608,000.8608
12	13	N 26°52'00.33" W	27.877	13	1,321,124.2757	607,982.2068	39	40	S 25°46'21.08" E	20.005	40	1,321,177.9000	608,009.5588
13	14	N 28°17'44.59" W	21.527	14	1,321,143.2307	607,972.0024	40	41	S 20°03'37.28" E	5.160	41	1,321,173.0527	608,011.3289
14	15	N 27°08'37.52" W	21.030	15	1,321,161.9444	607,962.4081	41	42	S 18°14'57.63" E	5.380	42	1,321,167.9429	608,013.0138
15	16	N 27°10'29.62" W	24.904	16	1,321,184.0991	607,951.0344	42	43	S 21°22'25.56" E	6.697	43	1,321,161.7062	608,015.4546
16	17	N 29°03'46.70" W	18.873	17	1,321,200.5954	607,941.8666	43	44	S 18°08'02.36" E	7.077	44	1,321,154.9811	608,017.6571
17	18	N 29°08'38.62" W	19.277	18	1,321,217.4314	607,932.4788	44	45	S 07°11'41.11" E	6.025	45	1,321,149.0033	608,018.4117
18	19	N 23°32'32.51" W	14.993	19	1,321,231.1761	607,926.4904	45	46	S 15°58'25.63" E	2.913	46	1,321,146.2026	608,019.2134
19	20	N 29°35'11.67" W	4.641	20	1,321,235.2117	607,924.1991	46	47	S 05°17'41.63" E	27.289	47	1,321,119.0302	608,021.7317
20	21	N 22°29'31.71" W	14.606	21	1,321,248.7065	607,918.6115	47	48	S 02°38'50.40" E	18.884	48	1,321,100.1661	608,022.6039
21	22	N 28°38'41.58" W	11.241	22	1,321,258.5714	607,913.2230	48	49	S 00°20'02.86" E	3.422	49	1,321,096.7445	608,022.6239
22	23	N 08°18'50.24" E	1.849	23	1,321,260.4014	607,913.4904	49	50	S 00°02'31.12" E	10.733	50	1,321,086.0114	608,022.6317
23	24	N 68°18'36.80" E	23.437	24	1,321,269.0634	607,935.2684	50	51	S 02°41'32.52" E	14.839	51	1,321,071.1884	608,023.3288
24	25	N 69°35'59.12" E	33.757	25	1,321,280.8302	607,966.9080	51	52	S 05°24'42.59" E	6.650	52	1,321,064.5678	608,023.9560
25	26	N 74°43'12.09" E	7.816	26	1,321,282.8899	607,974.4474	52	1	S 08°24'12.93" E	5.791	1	1,321,058.8387	608,024.8024
26	27	N 72°04'07.42" E	24.089	27	1,321,290.3064	607,997.3665							

SUPERFICIE = 10,475.696 m2 = 14,858.88 Vrs2

Objeto Lev: Verificación de área	Número Catastral: 2951-1-08-000-24401	FIRMA:	SELLO
Propietario: Julio Rene Alvarez Ayala edit. edit.	Ubicación: Entrada a Los Chilamate carretera Granada-Masaya 2,319 m SO, 855.12 m al N. Comarca la Laguna #2. Municipio de Granada. Departamento de Granada.	Ejecuta: Ing.Bosco Javier Morgan Lic. Catastral: BMM100426 SERVICIOS TOPOGRAFICOS	
Solicitante: edit. Cedula: edit	Área = 10,475.696 m2 = 14,858.88 Vrs2 — Escala: 1 / 750	Fecha: 08 de Enero del 2026	

ESPACIO PARA ESQUELA