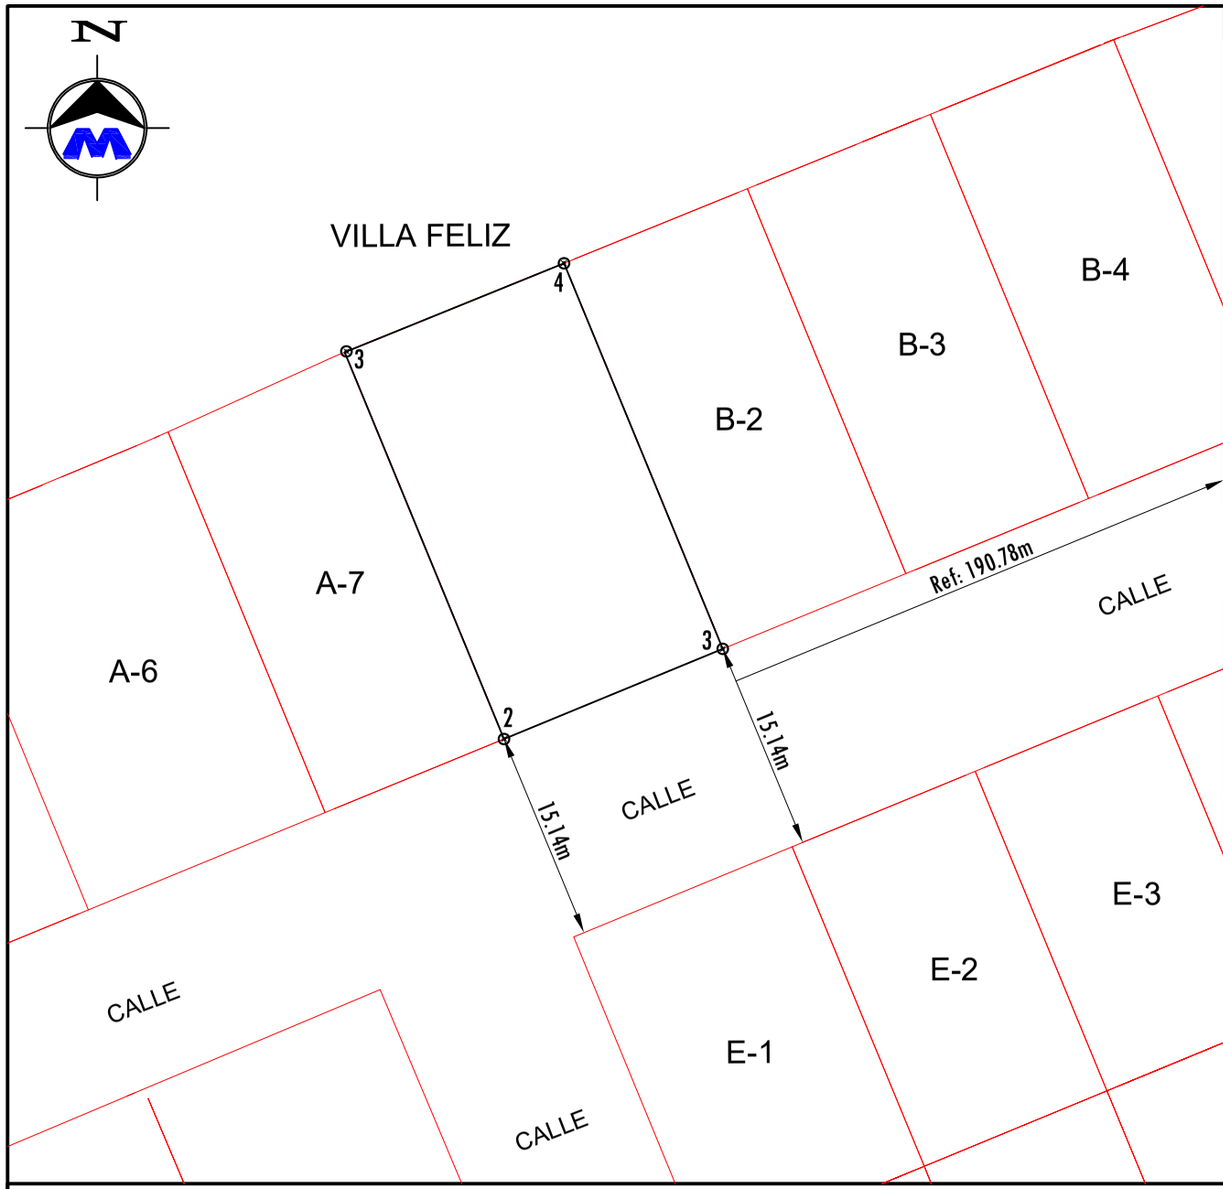

DEPARTAMENTO DE GRANADA MUNICIPIO DE GRANADA

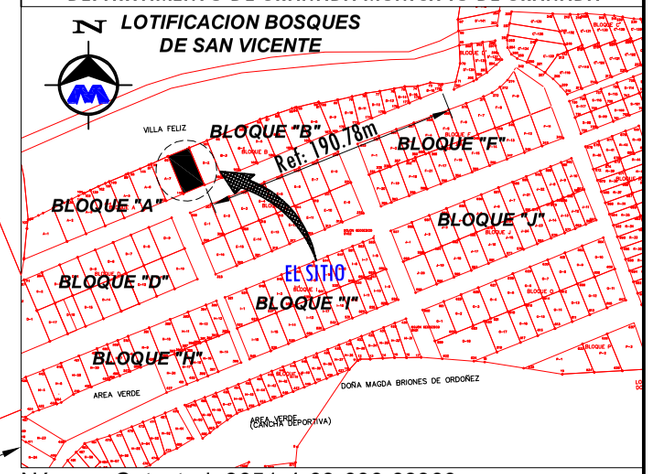

Número Catastral: 3051-4-09-000-03900
Planta de Ubicación Sin Escala

COORDENADAS NO VINCULADAS A LA RED GEODESICA DE NICARAGUA

CUADRO DE CONSTRUCCION

LADO EST	LADO PV	RUMBO	DISTANCIA	V	COORDENADAS Y	COORDENADAS X
				1	1,317,480.3069	612,895.8209
1	2	S 67°37'51.87" W	17.097	2	1,317,473.8003	612,880.0104
2	3	N 22°22'08.39" W	30.243	3	1,317,501.7672	612,868.5010
3	4	N 67°53'18.34" E	17.097	4	1,317,508.2028	612,884.3408
4	1	S 22°22'07.88" E	30.166	1	1,317,480.3069	612,895.8209

SUPERFICIE = 516.401 m2 = 732.47 Vrs2

ESPACIO PARA ESQUELA

Objeto Lev: Venta Total	Número Catastral: 3051-4-09-000-03900	FIRMA:
Enajenante:Melvyn Alejandro Arostegui Maldonado Cédula: 201-050476-0009E	Ubicacion: Lotificacion Bosques San Vicente lote # 1 Bloque B. Municipio de Granada, Departamento de Granada.	Ejecuta: Ing.Bosco Javier Morgan Lic. Catastral: BMM100426 Cel: 8883-7568 Email: ingmorgan73@gmail.com SERVICIOS TOPOGRAFICOS
Enajenante:Yuri Elieth Brown Gonzalez Cédula: 201-091086-0009X	Área: 516.401 m2 = 732.47 Vrs2 — Escala: 1 / 500	Fecha: 19 de Enero del 2026