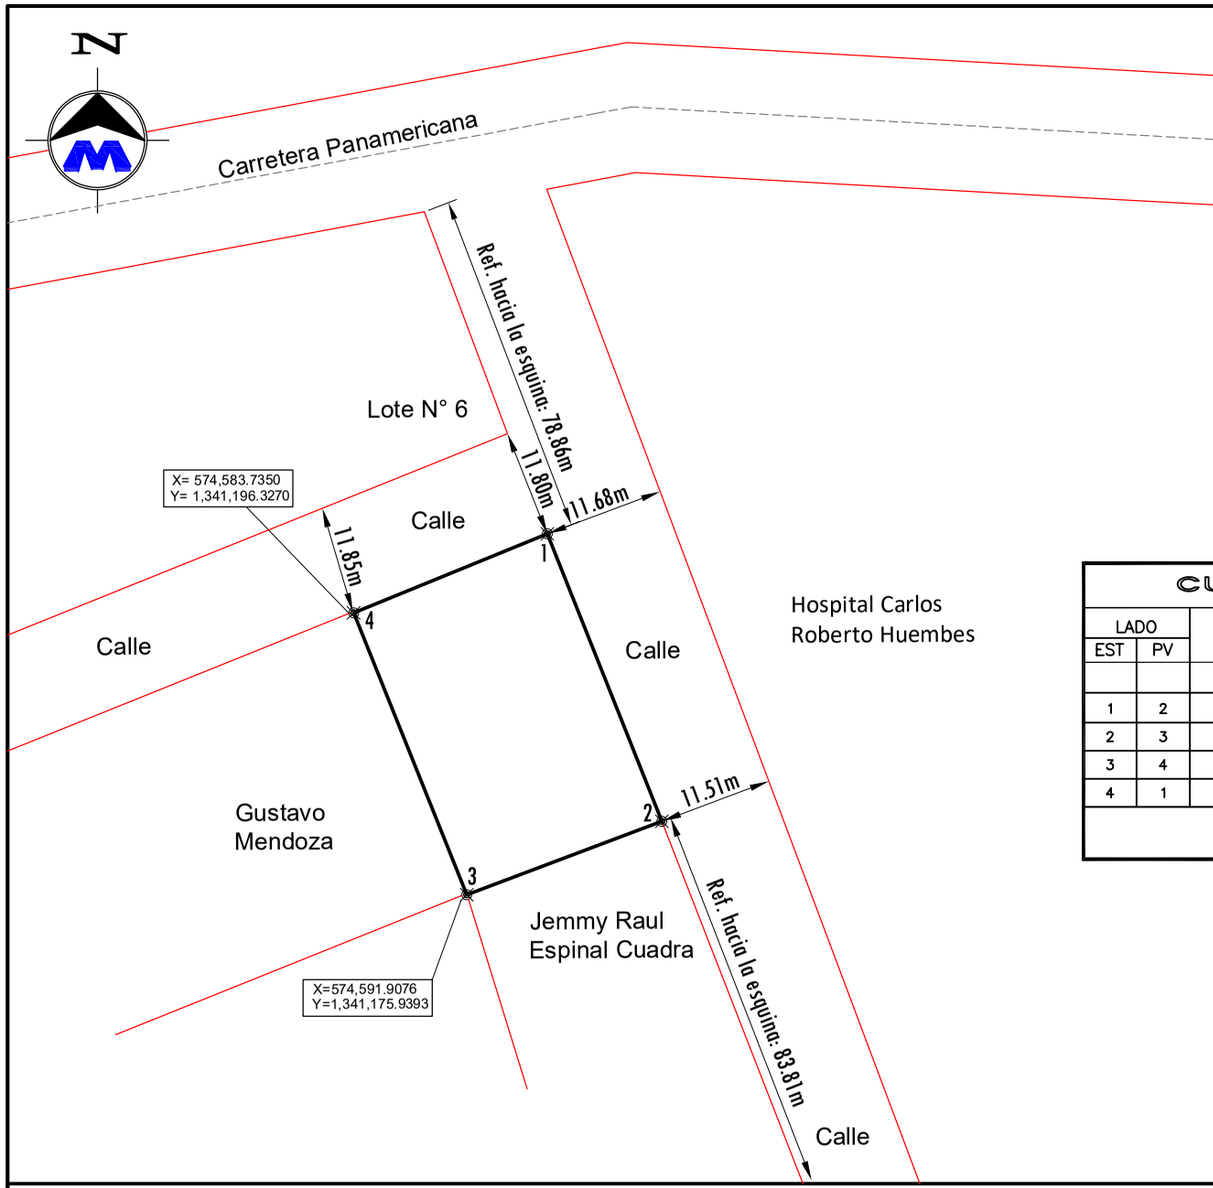

DEPARTAMENTO DE MANAGUA MUNICIPIO DE CIUDAD SANDINO

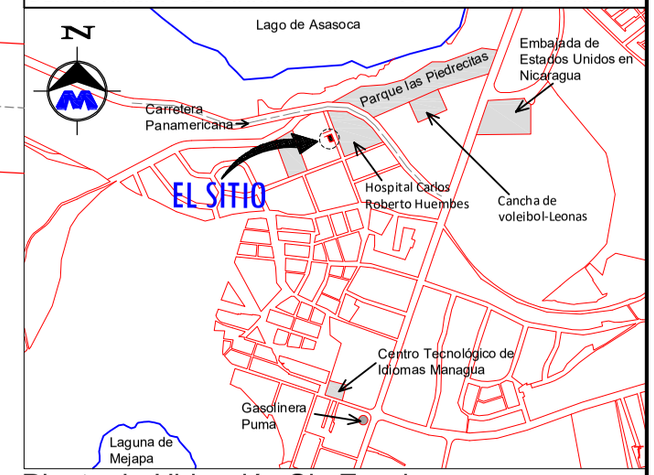

Planta de Ubicación Sin Escala

Número Catastral: 53744151992123

CUADRO DE CONSTRUCCION

LADO EST	LADO PV	RUMBO	DISTANCIA	V	COORDENADAS Y	COORDENADAS X
				1	1,341,202.0290	574,597.7310
1	2	S 21°42'04.90" E	22.438	2	1,341,181.1810	574,606.0280
2	3	S 69°38'03.75" W	15.062	3	1,341,175.9393	574,591.9076
3	4	N 21°50'37.63" W	21.965	4	1,341,196.3270	574,583.7350
4	1	N 67°50'02.09" E	15.113	1	1,341,202.0290	574,597.7310

SUPERFICIE = 334.910 m2

Objeto Lev: Rectificacion de Area	Número Catastral: 53744151992123	FIRMA:	SELLO
Enajenante: Chung Ming Lee Ced. de Residencia: 280520140270	Ubicación: Residencial Las Piedrecitas, costado Oeste del Hospital Carlos Roberto Huembes. Municipio de Ciudad Sandino, Departamento de Managua.	Ejecuta: Ing. Bosco Javier Morgan Mercado Lic. Catastral: BMM100426 Cel: 8883-7568 Email: ingmorgan73@gmail.com SERVICIOS TOPOGRAFICOS	
Adquiriente: Fernando Josué Davila Espinoza Cédula: 001-131102-1038K	Factor de escala: 1.418415 — Escala: 1 /500	Fecha: 19 de diciembre del 2025	

ESPACIO PARA ESQUELA