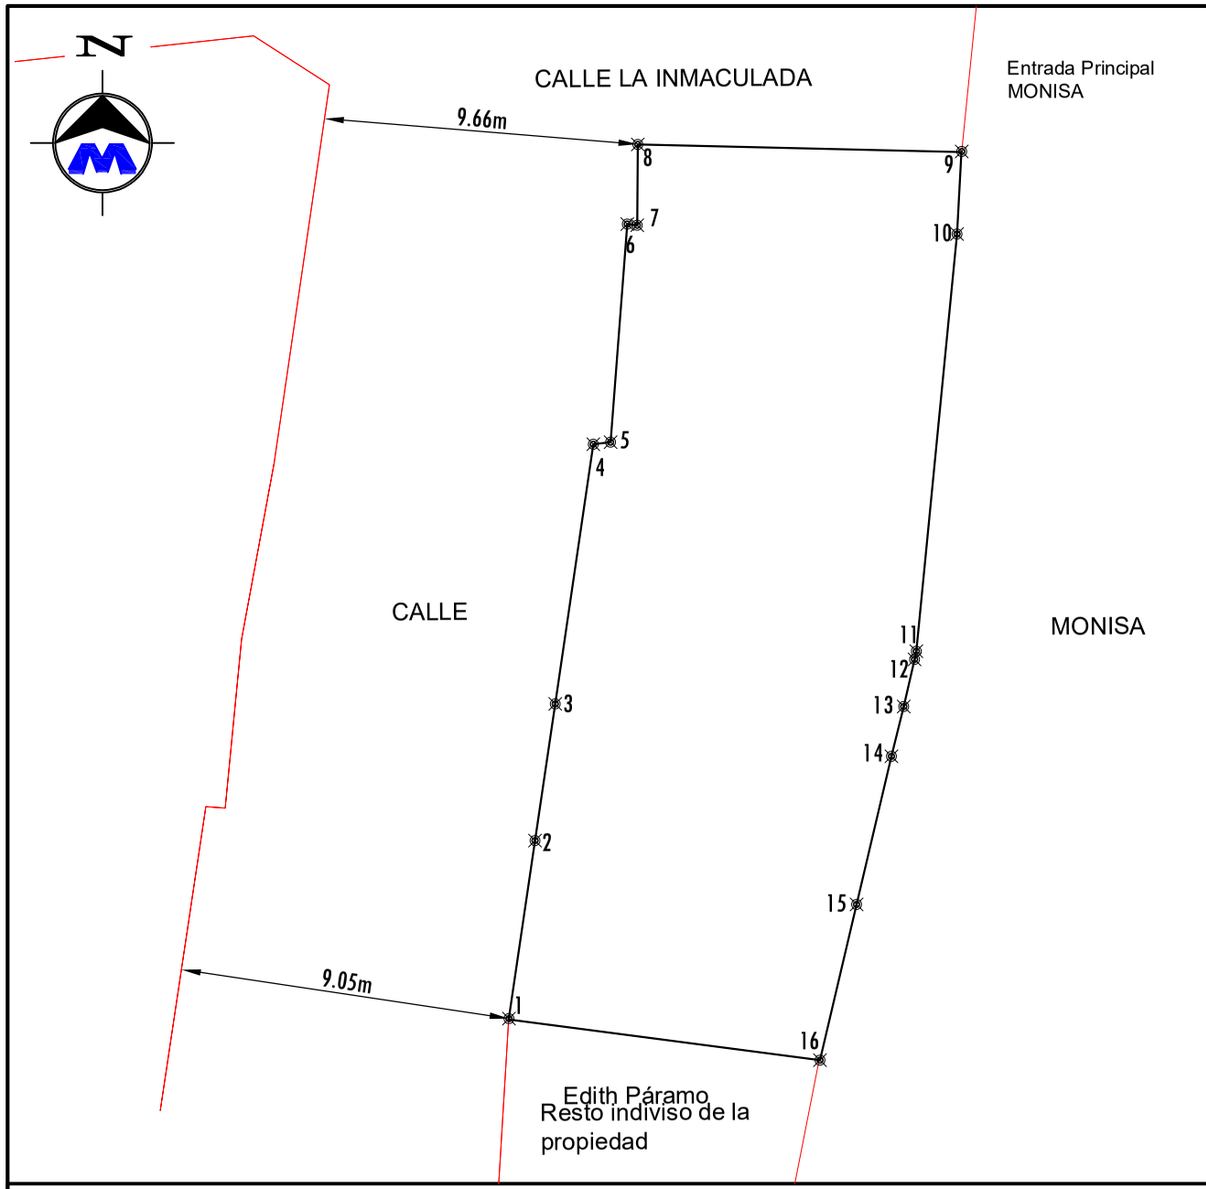

DEPARTAMENTO DE GRANADA MUNICIPIO DE GRANADA

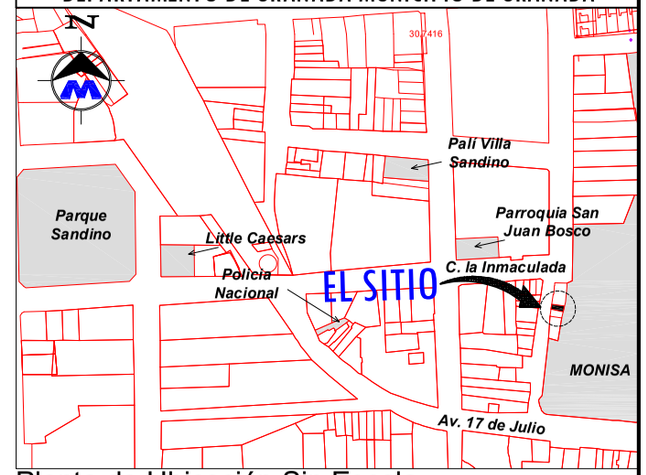

Planta de Ubicación Sin Escala

Número Catastral: 3051-4-05-058-04503

COORDENADAS NO VINCULADAS A LA RED GEODESICA DE NICARAGUA

CUADRO DE CONSTRUCCION

LADO EST	LADO PV	RUMBO	DISTANCIA	V	COORDENADAS Y	COORDENADAS X
				1	1,319,764.6600	614,059.6008
1	2	N 08°21'59.06" E	5.225	2	1,319,769.8296	614,060.3611
2	3	N 08°21'59.06" E	4.000	3	1,319,773.7870	614,060.9431
3	4	N 08°21'59.06" E	7.593	4	1,319,781.2988	614,062.0478
4	5	N 83°17'29.27" E	0.500	5	1,319,781.3572	614,062.5444
5	6	N 04°21'29.49" E	6.330	6	1,319,787.6686	614,063.0254
6	7	S 82°26'03.67" E	0.292	7	1,319,787.6301	614,063.3149
7	8	N 00°23'42.70" E	2.337	8	1,319,789.9670	614,063.3310
8	9	S 88°41'27.35" E	9.364	9	1,319,789.7531	614,072.6921
9	10	S 03°07'46.03" W	2.382	10	1,319,787.3746	614,072.5620
10	11	S 05°33'48.59" W	12.124	11	1,319,775.3080	614,071.3867
11	12	S 12°25'00.09" W	0.238	12	1,319,775.0752	614,071.3354
12	13	S 12°53'03.49" W	1.402	13	1,319,773.7082	614,071.0227
13	14	S 13°56'58.86" W	1.484	14	1,319,772.2676	614,070.6649
14	15	S 13°13'14.35" W	4.400	15	1,319,767.9843	614,069.6586
15	16	S 13°13'14.35" W	4.630	16	1,319,763.4772	614,068.5998
16	1	N 82°30'45.29" W	9.076	1	1,319,764.6600	614,059.6008

SUPERFICIE = 250.537 m2 = 355.57 Vrs2

Objeto Lev: Desmembración por Indivisión	Número Catastral: 3051-4-05-058-04503		FIRMA:	SELLO
Propietario: Javier Hernandez Ruiz Ced: 201-191069-0003F	Ubicación:Barrio San Juan Bosco, contiguo a la entrada principal de Monisa, Costado Oeste. Municipio de Granada Departamento de Granada.		Ejecuta: Ing. Bosco Javier Morgan Lic. Catastral: BMM100426 Cel: 8883-7568 Email: ingmorgan73@gmail.com SERVICIOS TOPOGRAFICOS	
Factor de escala: 1.418415	Área: 250.537 m2 = 355.57 Vrs2	Escala:1 /150	Fecha: 13 de Febrero del 2026	

ESPACIO PARA ESQUELA