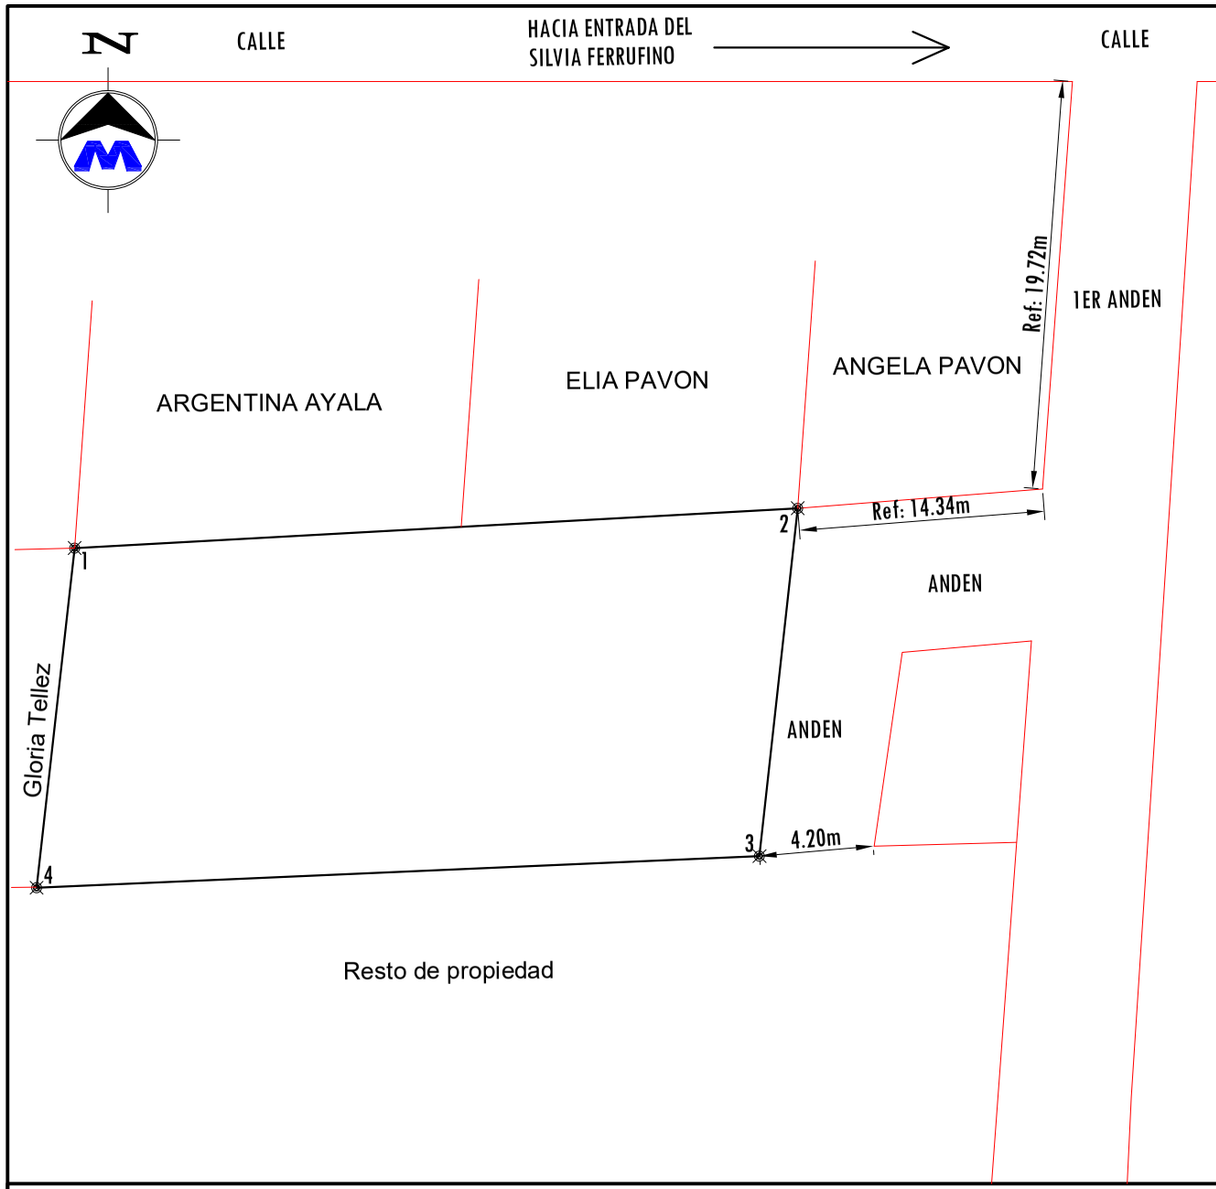

DEPARTAMENTO DE GRANADA MUNICIPIO DE GRANADA

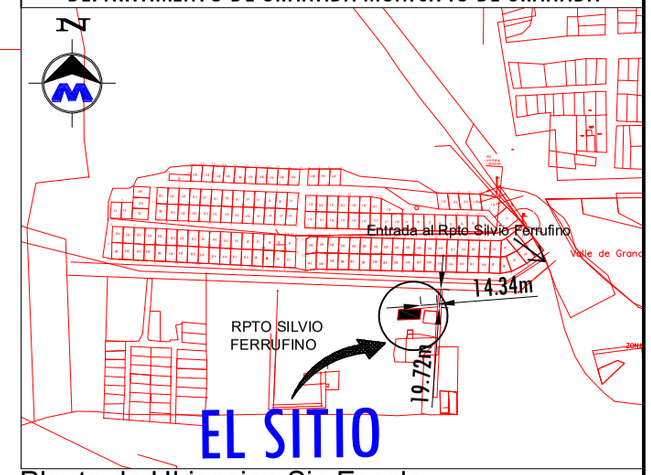

Planta de Ubicacion Sin Escala
Número Catastra: 3051-4-05-000-(02616)

COORDENADAS NO VINCULADAS A LA RED GEODESICA DE NICARAGUA

CUADRO DE CONSTRUCCION

LADO EST	LADO PV	RUMBO	DISTANCIA	V	COORDENADAS Y	COORDENADAS X
				1	1,319,090.4008	611,882.4583
1	2	N 86°50'53.51" E	20.941	2	1,319,091.5521	611,903.3675
2	3	S 06°16'35.59" W	10.123	3	1,319,081.4894	611,902.2608
3	4	S 87°29'41.19" W	20.918	4	1,319,080.5750	611,881.3624
4	1	N 06°21'49.83" E	9.887	1	1,319,090.4008	611,882.4583

SUPERFICIE = 206.735 m2 = 293.24 Vrs2

Objeto Lev: Venta Parcial - Desmembración	Número Catastral: 3051-4-05-000-(02616)	Fecha: 11 de Febrero del 2026	FIRMA:
Enajenante: Luis Emilio Pabon Arias Cédula: 203-210626-0001A	Ubicación: Rpto Silvio Ferrufino, de la entrada principal 1er anden, 19.72 m al Sur, 14.34 m al Oeste. Municipio de Granada, Departamento de Granada	Ejecuta: Ing.Bosco Javier Morgan Lic. Catastral: BMM100426 Cel: 8883-7568 Email: ingmorgan73@gmail.com servicios topograficos	
Adquiriente: Ana Maria Poveda Rudea Cédula: 201-050679-0003U	Área: 206.735 m2 = 293.24 Vrs2	Escala: 1 / 200	

ESPACIO PARA ESQUELA