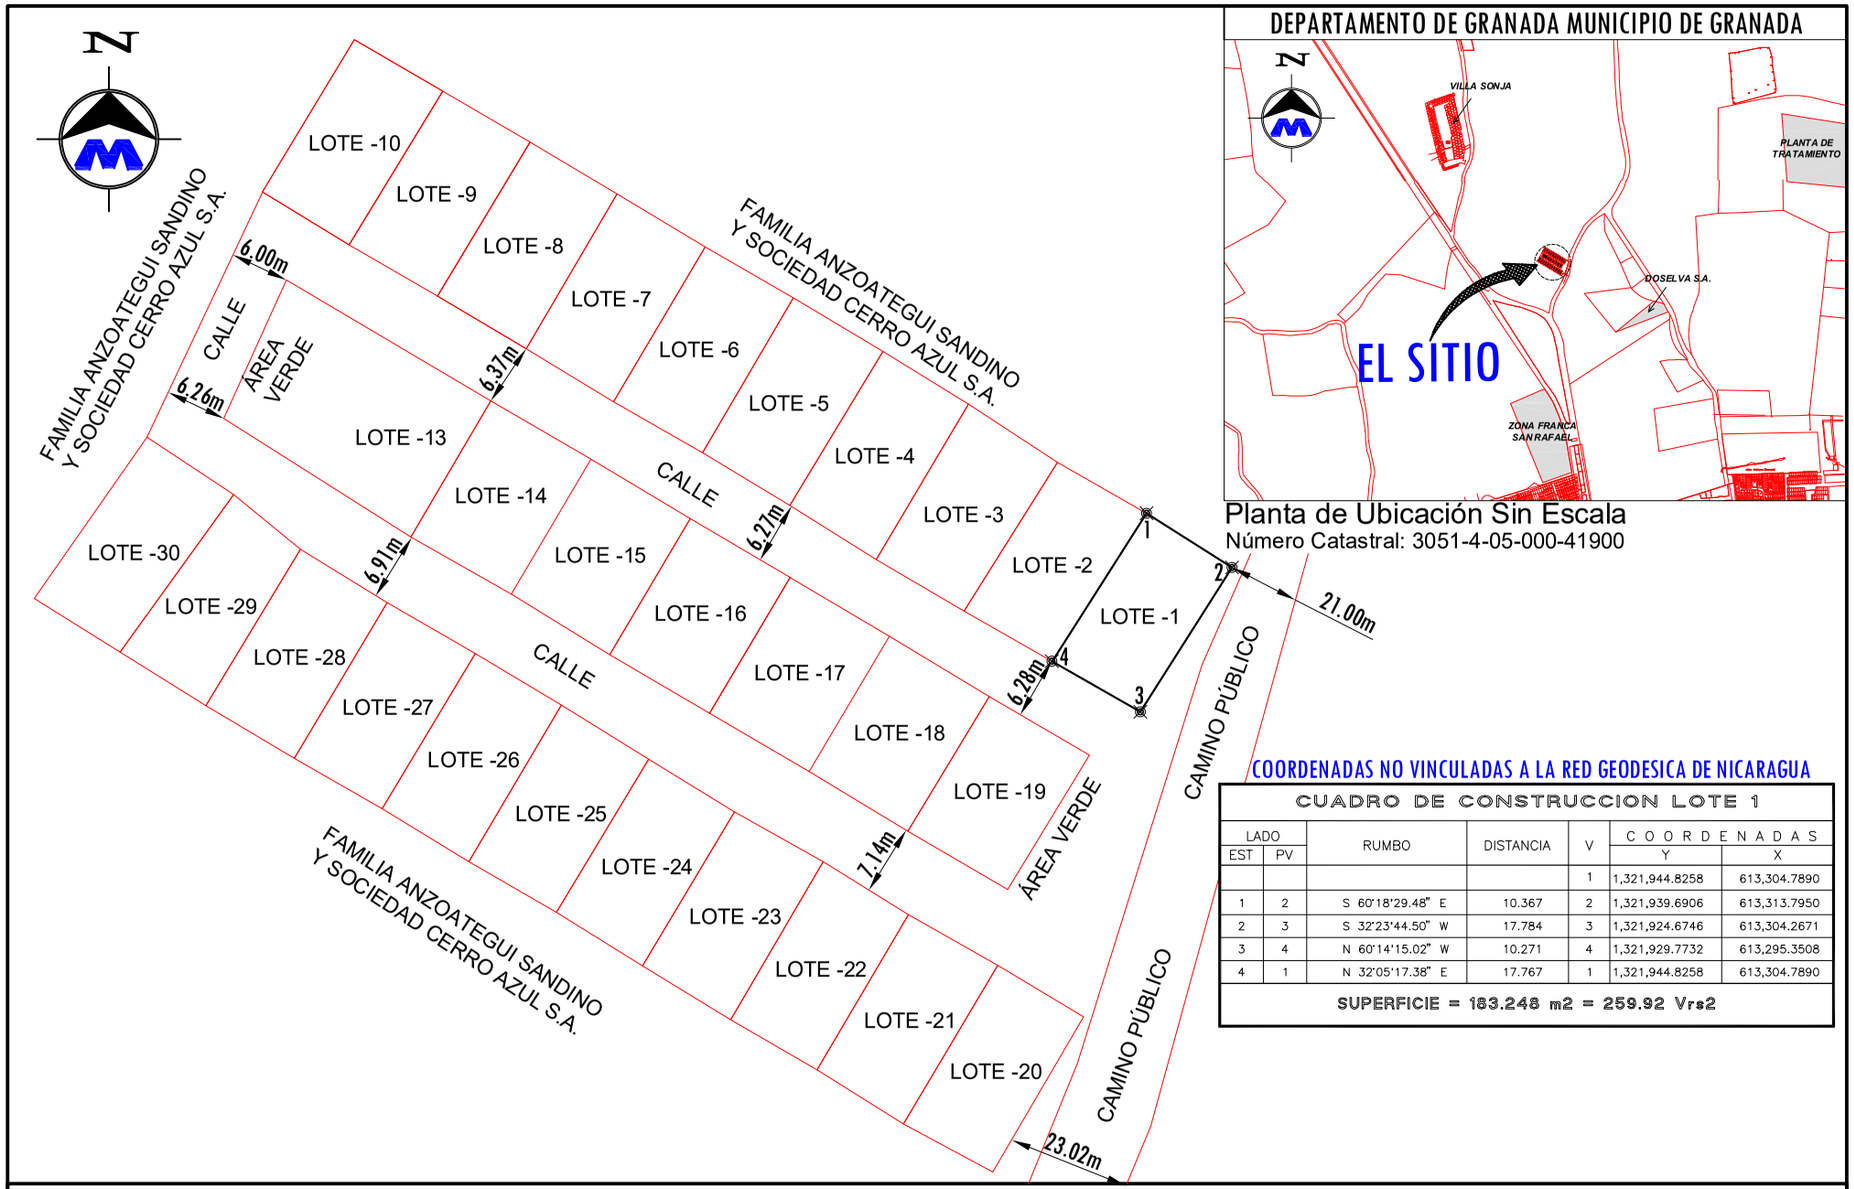

DEPARTAMENTO DE GRANADA MUNICIPIO DE GRANADA

Planta de Ubicación Sin Escala
Número Catastral: 3051-4-05-000-41900

COORDENADAS NO VINCULADAS A LA RED GEODESICA DE NICARAGUA

CUADRO DE CONSTRUCCION LOTE 1

LADO EST	LADO PV	RUMBO	DISTANCIA	V	COORDENADAS Y	COORDENADAS X
				1	1,321,944.8258	613,304.7890
1	2	S 60°18'29.48" E	10.367	2	1,321,939.6906	613,313.7950
2	3	S 32°23'44.50" W	17.784	3	1,321,924.6746	613,304.2671
3	4	N 60°14'15.02" W	10.271	4	1,321,929.7732	613,295.3508
4	1	N 32°05'17.38" E	17.767	1	1,321,944.8258	613,304.7890

SUPERFICIE = 183.248 m2 = 259.92 Vrs2

Objeto Lev: Donación de una parte Indivisa	Número Catastral: 3051-4-05-000-41900		FIRMA:
Enajenante: COOPERTATIVA SERVICIOS Y MANUALIDADES LOS ANGELES R.L. N° RUC: J0810000298664	Ubicación: Antigua Finca Obregon, Camino a los Malacos. Lote-1 Municipio de Granada, Departamento de Granada.		Ejecuta: Ing.Bosco Javier Morgan Lic. Catastral: BMM100426 Cel: 8883-7568 Email: ingmorgan73@gmail.com SERVICIOS TOPOGRAFICOS
Adquiriente: Brenda Aracel Arauz Urbina; Ced: 201-250482-0003J	Área: 183.248 m2 = 259.92 Vrs2	Escala: 1 /700	Fecha: 9 de febrero del 2026

ESPACIO PARA ESQUELA