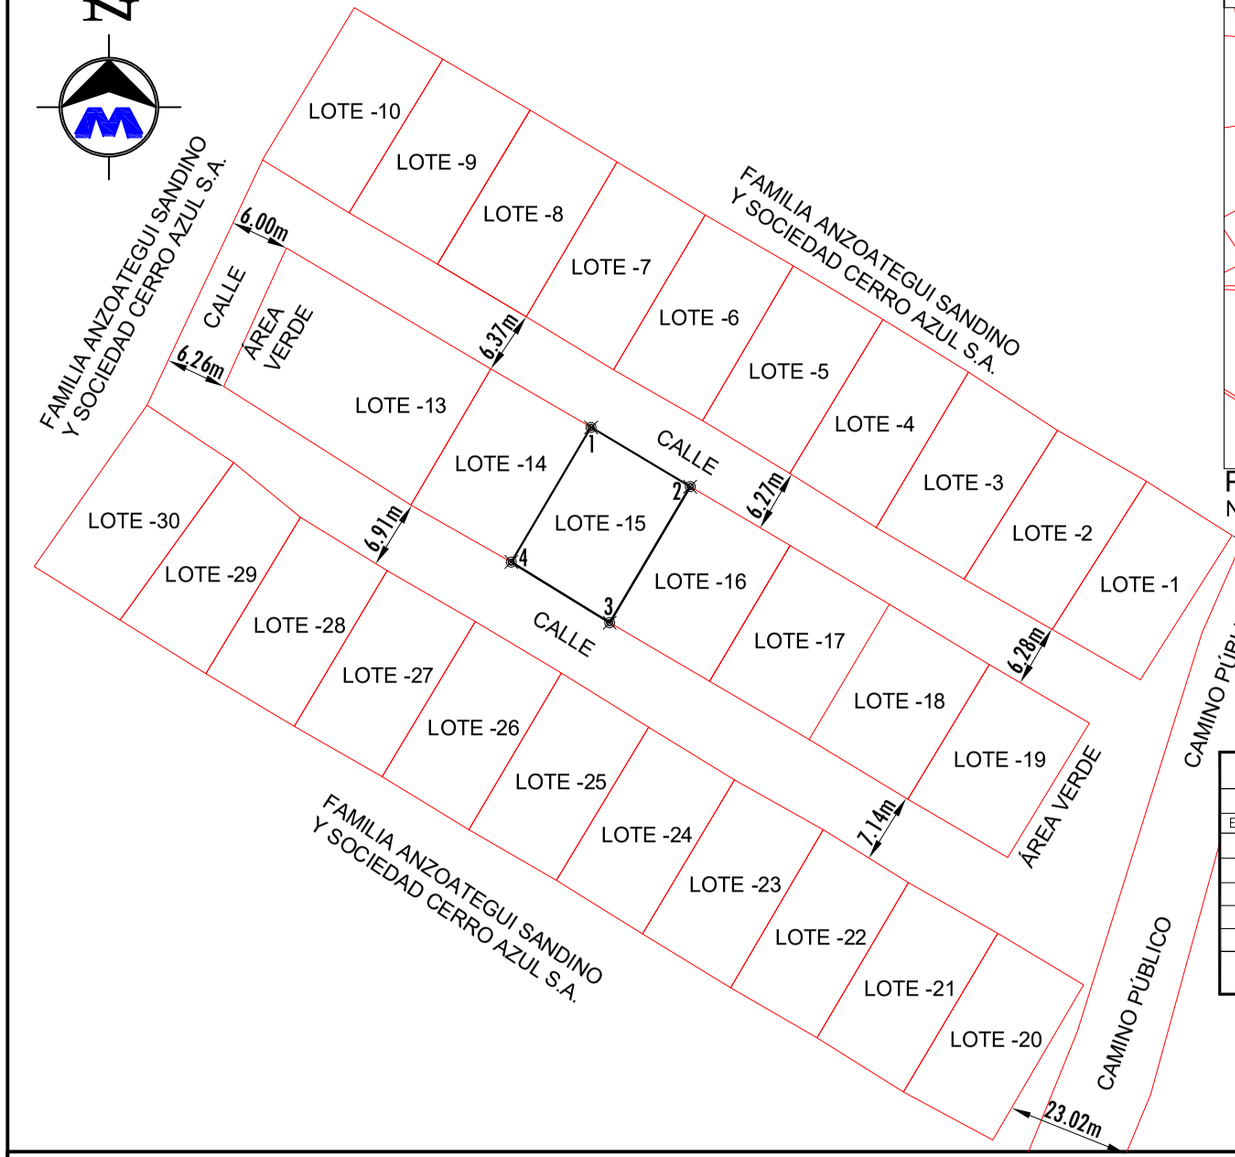

DEPARTAMENTO DE GRANADA MUNICIPIO DE GRANADA

Planta de Ubicación Sin Escala
Número Catastral: 3051-4-05-000-41900

COORDENADAS NO VINCULADAS A LA RED GEODESICA DE NICARAGUA

CUADRO DE CONSTRUCCION LOTE 15

LADO EST	LADO PV	RUMBO	DISTANCIA	V	COORDENADAS Y	COORDENADAS X
				1	1,321,950.2542	613,248.6567
1	2	S 59°02'47.51" E	11.714	2	1,321,944.2293	613,258.7023
2	3	S 30°33'01.28" W	15.995	3	1,321,930.4549	613,250.5722
3	4	N 58°16'59.74" W	11.706	4	1,321,936.6090	613,240.6143
4	1	N 30°30'53.67" E	15.839	1	1,321,950.2542	613,248.6567

SUPERFICIE = 186.364 m2 = 264.34 Vrs2

Objeto Lev: Donación de una parte Indivisa	Número Catastral: 3051-4-05-000-41900		FIRMA:
Enajenante: COOPERTATIVA SERVICIOS Y MANUALIDADES LOS ANGELES R.L. N° RUC: J0810000298664	Ubicación: Antigua Finca Obregon, Camino a los Malacos. Lote-15 Municipio de Granada, Departamento de Granada.		Ejecuta: Ing.Bosco Javier Morgan Lic. Catastral: BMM100426 Cel: 8883-7568 Email: ingmorgan73@gmail.com SERVICIOS TOPOGRAFICOS
Adquiriente: Hayzel Massiel Tellez Sanchez; Ced: 201-251192-0005C	Área: 186.364 m2 = 264.34 Vrs2	Escala: 1 /700	Fecha: 9 de febrero del 2026

ESPACIO PARA ESQUELA