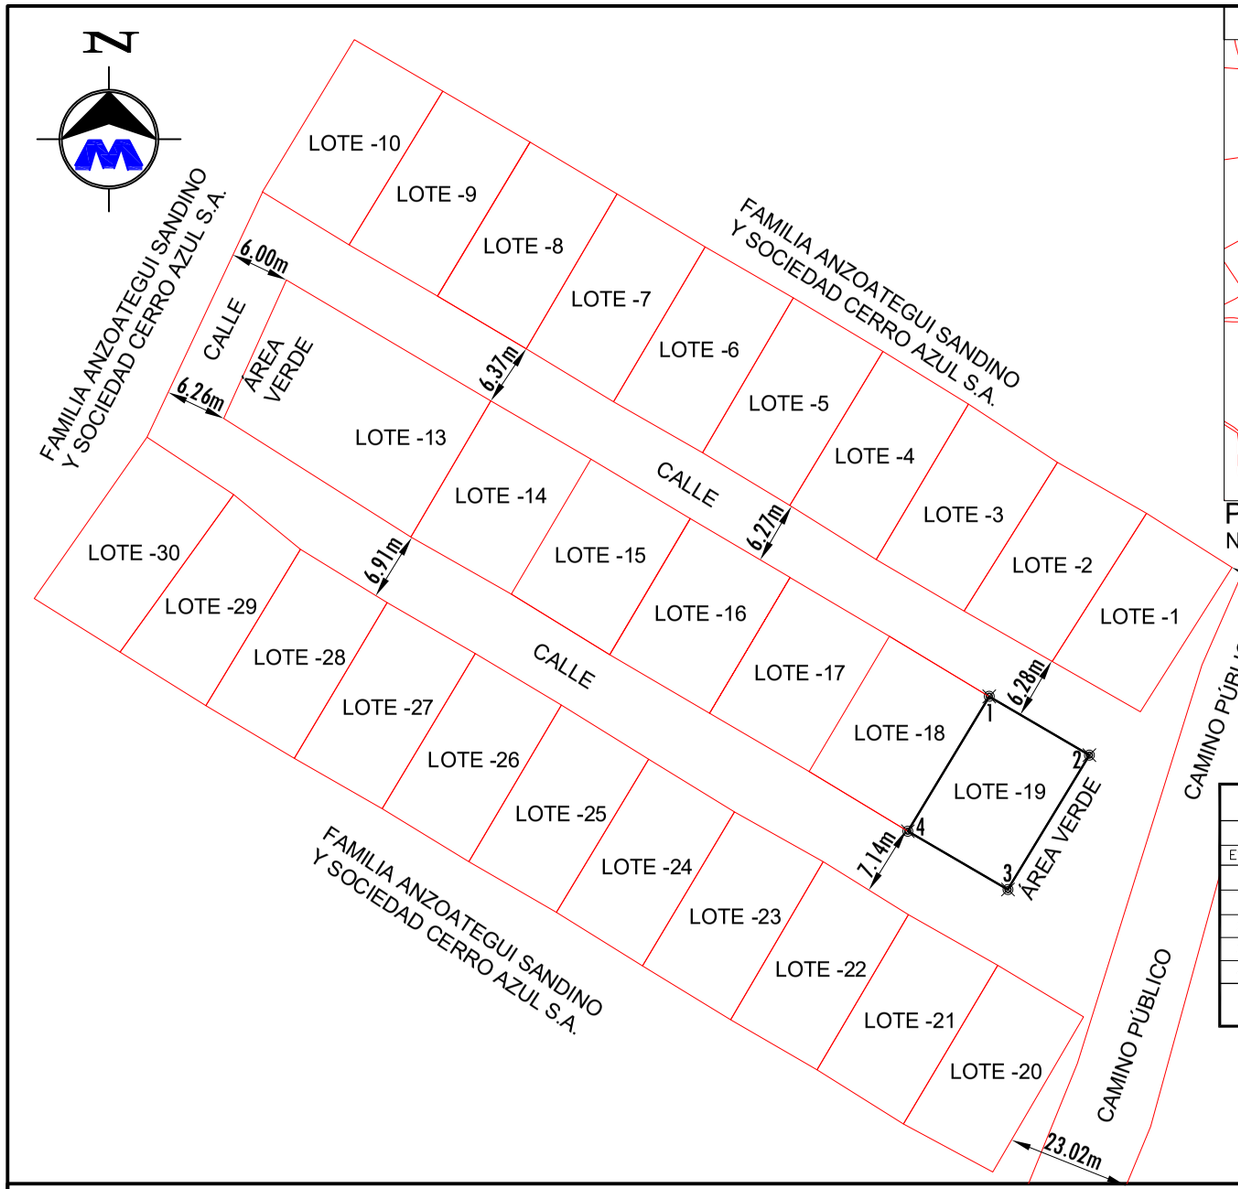

DEPARTAMENTO DE GRANADA MUNICIPIO DE GRANADA

Planta de Ubicación Sin Escala
Número Catastral: 3051-4-05-000-41900

COORDENADAS NO VINCULADAS A LA RED GEODESICA DE NICARAGUA

CUADRO DE CONSTRUCCION LOTE 19

LADO EST	LADO PV	RUMBO	DISTANCIA	V	COORDENADAS Y	COORDENADAS X
				1	1,321,926.2291	613,288.9765
1	2	S 59°40'39.91" E	11.748	2	1,321,920.2980	613,299.1173
2	3	S 31°16'34.89" W	15.919	3	1,321,906.6920	613,290.8525
3	4	N 59°49'50.46" W	11.713	4	1,321,912.5787	613,280.7258
4	1	N 31°09'00.46" E	15.950	1	1,321,926.2291	613,288.9765

SUPERFICIE = 186.899 m2 = 265.10 Vrs2

Objeto Lev: Donación de una parte Indivisa	Número Catastral: 3051-4-05-000-41900		FIRMA:
Enajenante: COOPERTATIVA SERVICIOS Y MANUALIDADES LOS ANGELES R.L. N° RUC: J0810000298664	Ubicación: Antigua Finca Obregon, Camino a los Malacos. Lote-19 Municipio de Granada, Departamento de Granada.		Ejecuta: Ing.Bosco Javier Morgan Lic. Catastral: BMM100426 Cel: 8883-7568 Email: ingmorgan73@gmail.com SERVICIOS TOPOGRAFICOS
Adquiriente: Graciela Judith Martinez Hondoy; Ced: 201-220190-0003P	Área: 186.899 m2 = 265.10 Vrs2	Escala: 1 /700	Fecha: 9 de febrero del 2026

ESPACIO PARA ESQUELA