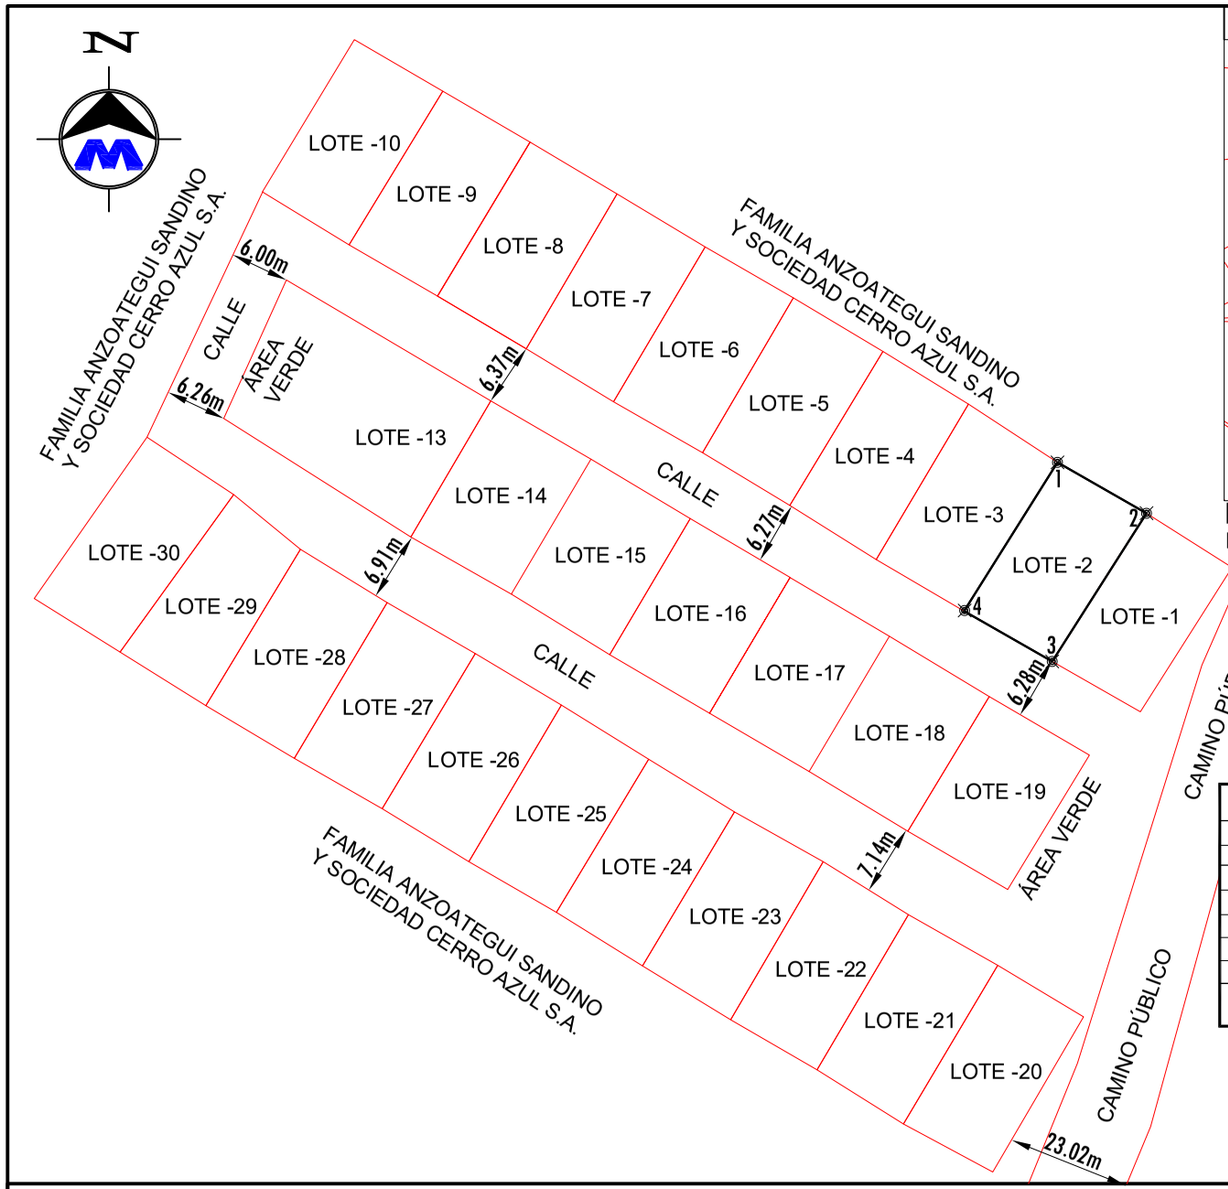

DEPARTAMENTO DE GRANADA MUNICIPIO DE GRANADA

Planta de Ubicación Sin Escala
Número Catastral: 3051-4-05-000-41900

COORDENADAS NO VINCULADAS A LA RED GEODESICA DE NICARAGUA

CUADRO DE CONSTRUCCION LOTE 2

LADO EST	LADO PV	RUMBO	DISTANCIA	V	COORDENADAS Y	COORDENADAS X
				1	1,321,949.9244	613,295.8727
1	2	S 60°18'29.48" E	10.367	2	1,321,944.7892	613,304.8787
2	3	S 32°23'44.50" W	17.784	3	1,321,929.7732	613,295.3508
3	4	N 60°14'15.02" W	10.271	4	1,321,934.8719	613,286.4346
4	1	N 32°05'17.38" E	17.767	1	1,321,949.9244	613,295.8727

SUPERFICIE = 183.248 m2 = 259.92 Vrs2

Objeto Lev: Donación de una parte Indivisa	Número Catastral: 3051-4-05-000-41900	FIRMA:
Enajenante: COOPERTATIVA SERVICIOS Y MANUALIDADES LOS ANGELES R.L. N° RUC: J0810000298664	Ubicación: Antigua Finca Obregon, Camino a los Malacos. Lote-2 Municipio de Granada, Departamento de Granada.	Ejecuta: Ing.Bosco Javier Morgan Lic. Catastral: BMM100426 Cel: 8883-7568 Email: ingmorgan73@gmail.com SERVICIOS TOPOGRAFICOS
Adquiriente: Marcos Arlen Gaitan Urbina; Ced: 201-250494-0012D	Área: 183.248 m2 = 259.92 Vrs2 — Escala: 1 /700	Fecha: 9 de febrero del 2026

ESPACIO PARA ESQUELA