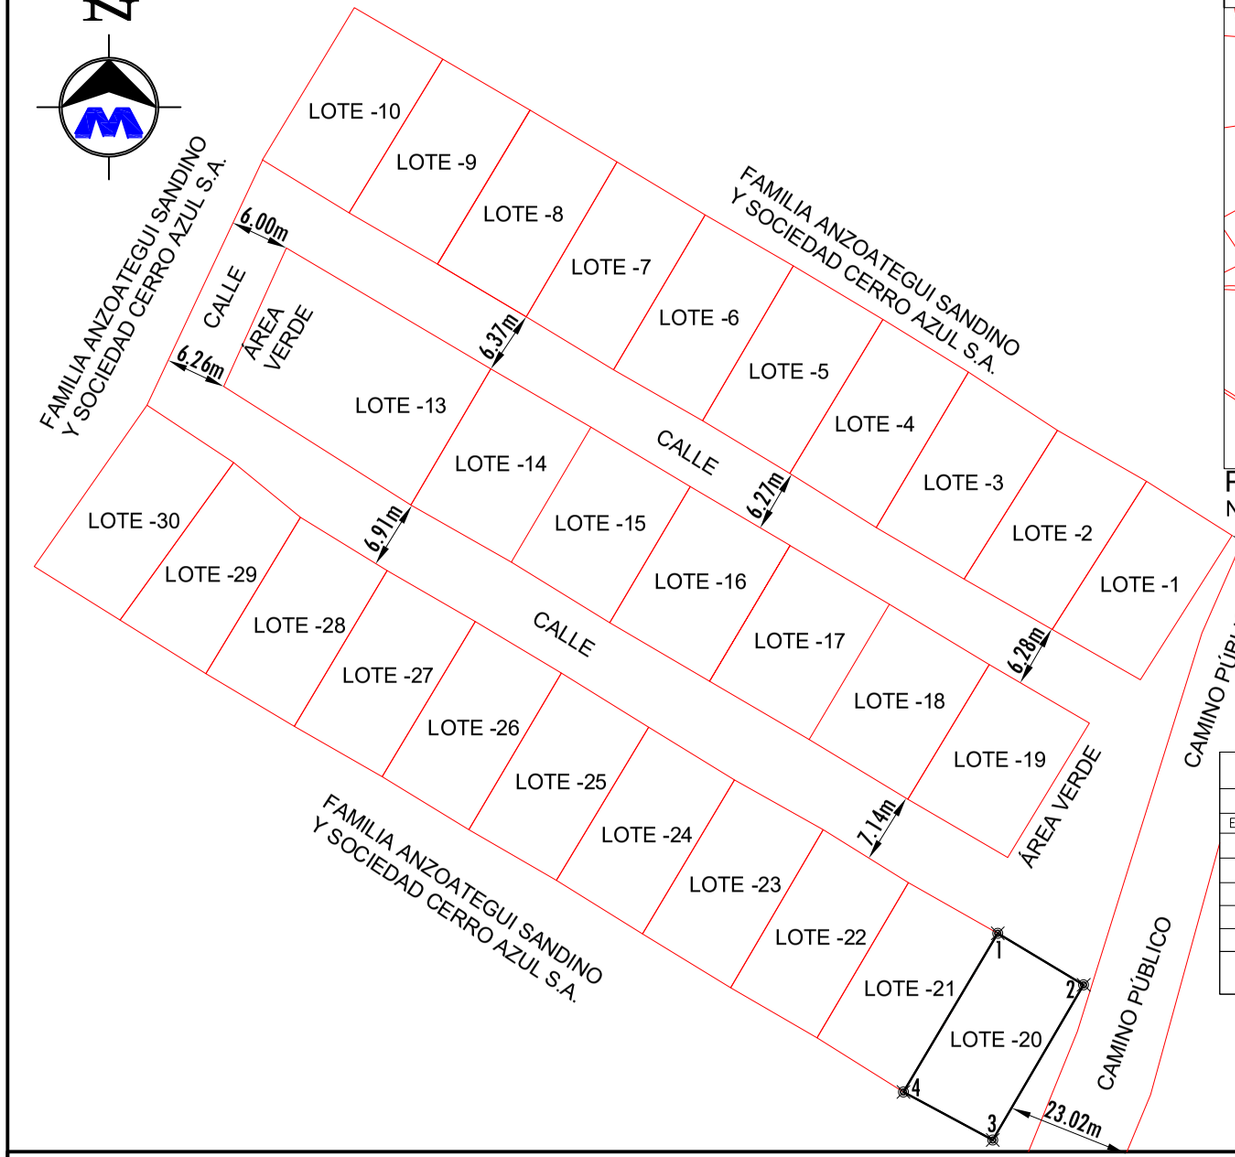

DEPARTAMENTO DE GRANADA MUNICIPIO DE GRANADA

Planta de Ubicación Sin Escala
Número Catastral: 3051-4-05-000-41900

COORDENADAS NO VINCULADAS A LA RED GEODESICA DE NICARAGUA

CUADRO DE CONSTRUCCION LOTE 20

LADO EST	LADO PV	RUMBO	DISTANCIA	V	COORDENADAS Y	COORDENADAS X
				1	1,321,898.9997	613,289.8387
1	2	S 59°05'12.92" E	10.133	2	1,321,893.7940	613,298.5323
2	3	S 30°23'12.60" W	18.200	3	1,321,878.0945	613,289.3263
3	4	N 61°42'53.85" W	10.248	4	1,321,882.9508	613,280.3015
4	1	N 30°43'16.46" E	18.669	1	1,321,898.9997	613,289.8387

SUPERFICIE = 187.780 m2 = 266.35 Vrs2

Objeto Lev: Donación de una parte Indivisa	Número Catastral: 3051-4-05-000-41900		FIRMA:
Enajenante: COOPERTATIVA SERVICIOS Y MANUALIDADES LOS ANGELES R.L. N° RUC: J0810000298664	Ubicación: Antigua Finca Obregon, Camino a los Malacos. Lote-20 Municipio de Granada, Departamento de Granada.		Ejecuta: Ing.Bosco Javier Morgan Lic. Catastral: BMM100426 Cel: 8883-7568 Email: ingmorgan73@gmail.com SERVICIOS TOPOGRAFICOS
Adquiriente: Sara Esther Hondoy Arguello; Ced: 201-031171-0000N	Área: 187.780 m2 = 266.35 Vrs2	Escala: 1 /700	Fecha: 9 de febrero del 2026

ESPACIO PARA ESQUELA