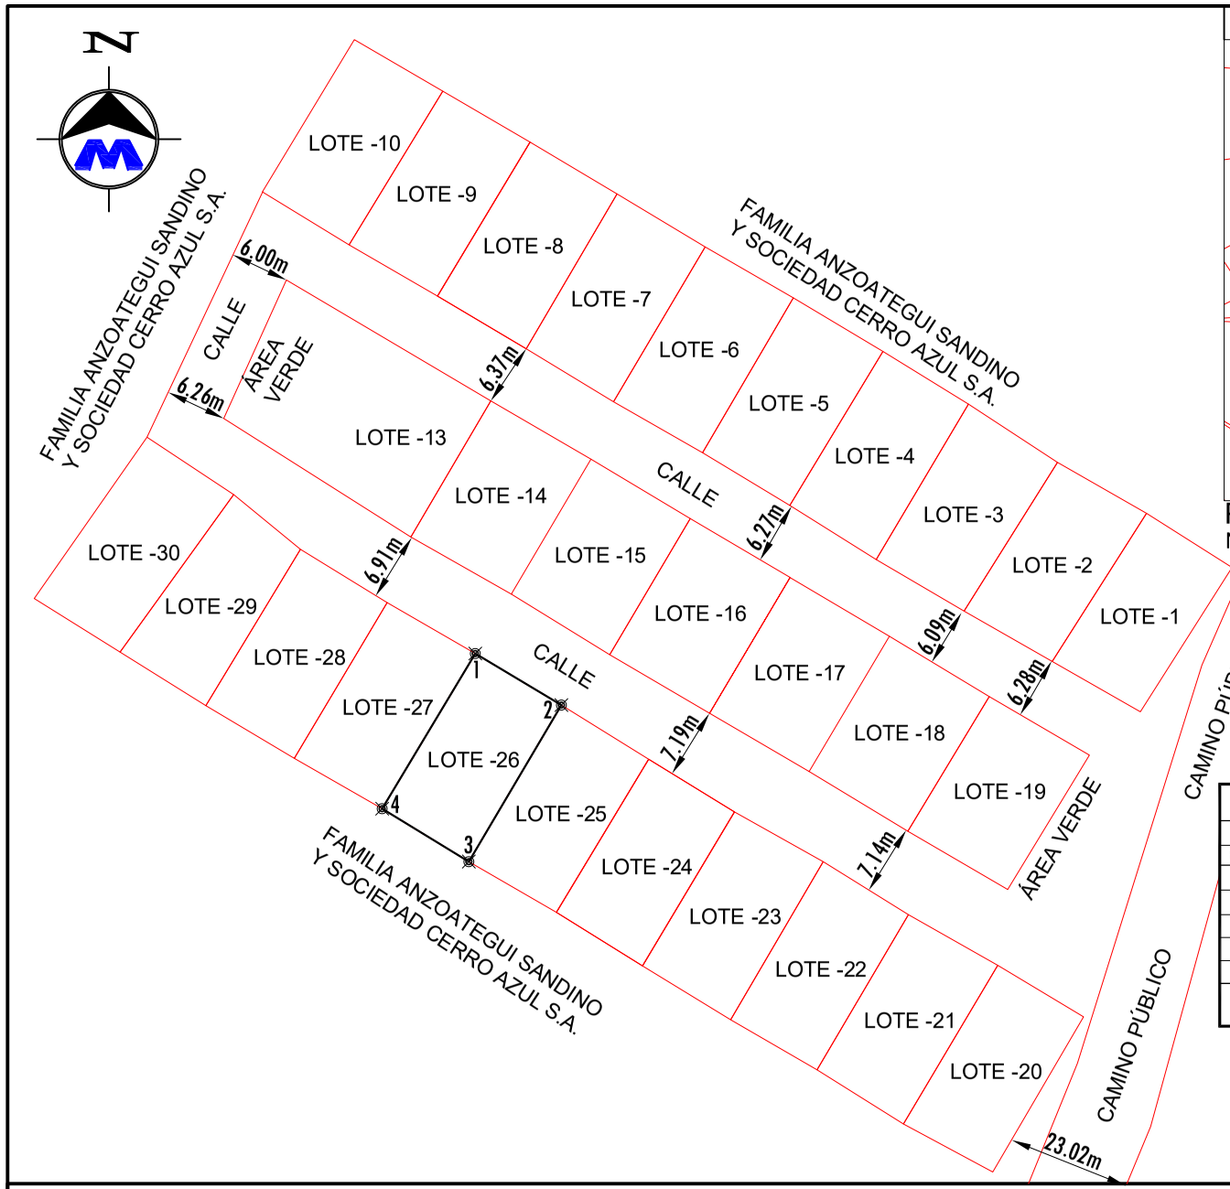

DEPARTAMENTO DE GRANADA MUNICIPIO DE GRANADA

Planta de Ubicación Sin Escala
Número Catastral: 3051-4-05-000-41900

COORDENADAS NO VINCULADAS A LA RED GEODESICA DE NICARAGUA

CUADRO DE CONSTRUCCION LOTE 26

LADO EST	LADO PV	RUMBO	DISTANCIA	V	COORDENADAS Y	COORDENADAS X
				1	1,321,930.5850	613,236.9542
1	2	S 59°03'40.03" E	10.171	2	1,321,925.3558	613,245.6781
2	3	S 30°35'51.63" W	18.400	3	1,321,909.5180	613,236.3125
3	4	N 58°32'25.52" W	10.274	4	1,321,914.8799	613,227.5487
4	1	N 30°55'00.28" E	18.306	1	1,321,930.5850	613,236.9542

SUPERFICIE = 187.604 m2 =266.10 Vrs2

Objeto Lev: Donación de una parte Indivisa	Número Catastral: 3051-4-05-000-41900		FIRMA:
Enajenante: COOPERTATIVA SERVICIOS Y MANUALIDADES LOS ANGELES R.L. N° RUC: J0810000298664	Ubicación: Antigua Finca Obregon, Camino a los Malacos. Lote-26 Municipio de Granada, Departamento de Granada.		Ejecuta: Ing.Bosco Javier Morgan Lic. Catastral: BMM100426 Cel: 8883-7568 Email: ingmorgan73@gmail.com SERVICIOS TOPOGRAFICOS
Adquiriente: Maria Dolores Jimenez Ramirez; Ced: 201-120576-0008A	Área: 187.604 m2 =266.10 Vrs2	Escala: 1 /700	Fecha: 9 de febrero del 2026

ESPACIO PARA ESQUELA