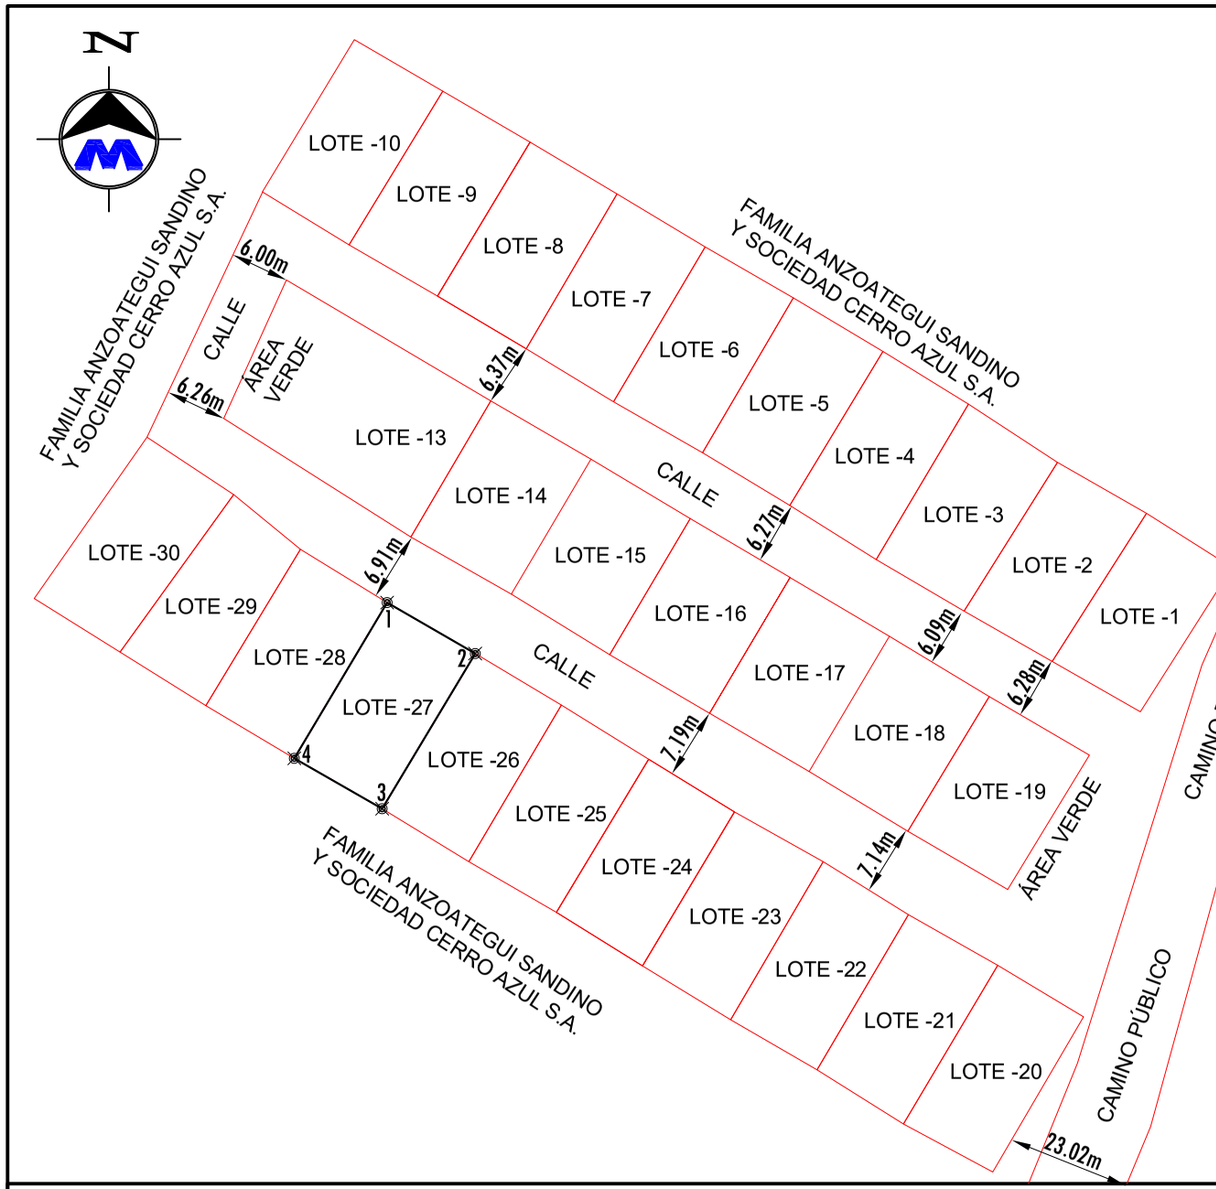

DEPARTAMENTO DE GRANADA MUNICIPIO DE GRANADA

Planta de Ubicación Sin Escala
Número Catastral: 3051-4-05-000-41900

COORDENADAS NO VINCULADAS A LA RED GEODESICA DE NICARAGUA

CUADRO DE CONSTRUCCION LOTE 27

LADO EST	LADO PV	RUMBO	DISTANCIA	V	COORDENADAS Y	COORDENADAS X
				1	1,321,935.7289	613,228.0426
1	2	S 60°00'20.41" E	10.290	2	1,321,930.5850	613,236.9542
2	3	S 30°55'00.28" W	18.306	3	1,321,914.8799	613,227.5487
3	4	N 60°13'14.17" W	10.261	4	1,321,919.9763	613,218.6426
4	1	N 30°49'32.64" E	18.344	1	1,321,935.7289	613,228.0426

SUPERFICIE = 188.270 m2 = 267.04 Vrs2

ESPACIO PARA ESQUELA

Objeto Lev: Donación de una parte Indivisa	Número Catastral: 3051-4-05-000-41900	FIRMA:
Enajenante: COOPERTATIVA SERVICIOS Y MANUALIDADES LOS ANGELES R.L. N° RUC: J0810000298664	Ubicación: Antigua Finca Obregon, Camino a los Malacos. Lote-27 Municipio de Granada, Departamento de Granada.	Ejecuta: Ing.Bosco Javier Morgan Lic. Catastral: BMM100426 Cel: 8883-7568 Email: ingmorgan73@gmail.com SERVICIOS TOPOGRAFICOS
Adquiriente: Alejandro Antonio Balladarez Troz; Ced: 201-080983-0009F	Área: 188.270 m2 = 267.04 Vrs2 — Escala: 1 /700	Fecha: 9 de febrero del 2026