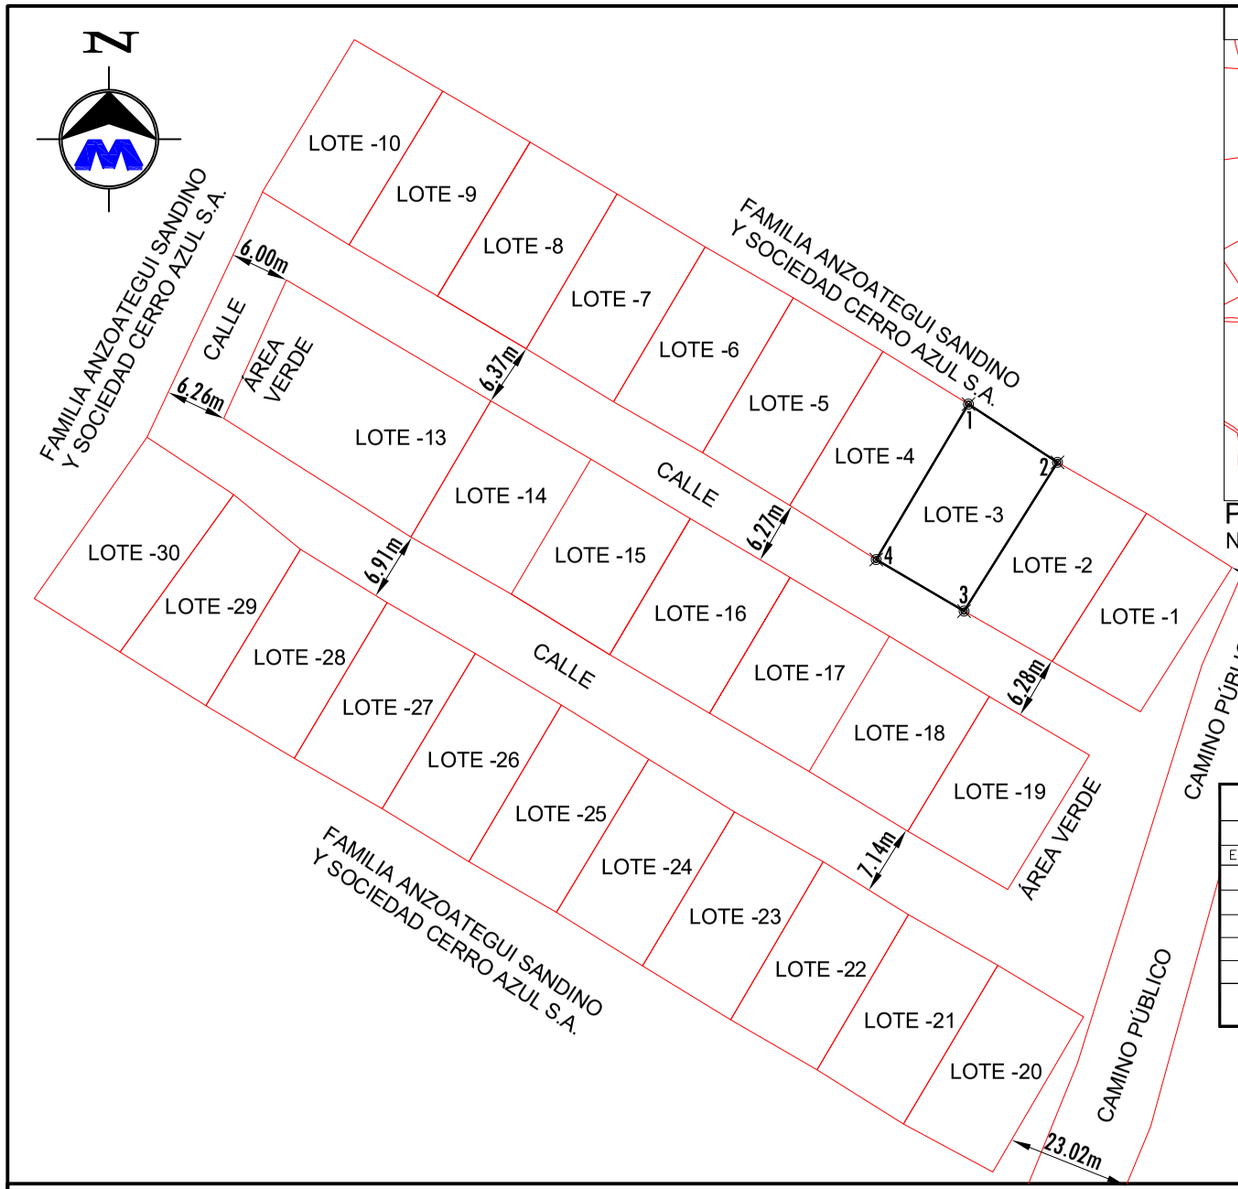


## DEPARTAMENTO DE GRANADA MUNICIPIO DE GRANADA

Planta de Ubicación Sin Escala
Número Catastral: 3051-4-05-000-41900

COORDENADAS NO VINCULADAS A LA RED GEODESICA DE NICARAGUA

**CUADRO DE CONSTRUCCION LOTE 3**

| LADO EST | LADO PV | RUMBO | DISTANCIA | V | COORDENADAS Y | COORDENADAS X |
|---|---|---|---|---|---|---|
| | | | | 1 | 1,321,955.8413 | 613,286.8807 |
| 1 | 2 | S 56°39'17.22" E | 10.764 | 2 | 1,321,949.9244 | 613,295.8727 |
| 2 | 3 | S 32°05'17.38" W | 17.767 | 3 | 1,321,934.8719 | 613,286.4346 |
| 3 | 4 | N 59°40'42.00" W | 10.319 | 4 | 1,321,940.0816 | 613,277.5269 |
| 4 | 1 | N 30°41'24.95" E | 18.326 | 1 | 1,321,955.8413 | 613,286.8807 |

**SUPERFICIE = 190.155 m2 = 269.72 Vrs2**

| | | | |
|---|---|---|---|
| Objeto Lev: Donación de una parte Indivisa | Número Catastral: 3051-4-05-000-41900 | | FIRMA: |
| Enajenante: COOPERTATIVA SERVICIOS Y MANUALIDADES LOS ANGELES R.L. N° RUC: J0810000298664 | Ubicación: Antigua Finca Obregon, Camino a los Malacos. Lote-3 Municipio de Granada, Departamento de Granada. | | Ejecuta: Ing.Bosco Javier Morgan<br>Lic. Catastral: BMM100426<br>Cel: 8883-7568 Email: ingmorgan73@gmail.com<br>SERVICIOS TOPOGRAFICOS |
| Adquiriente: | Área: 190.155 m2 = 269.72 Vrs2 | Escala: 1 /700 | Fecha: 9 de febrero del 2026 |

ESPACIO PARA ESQUELA