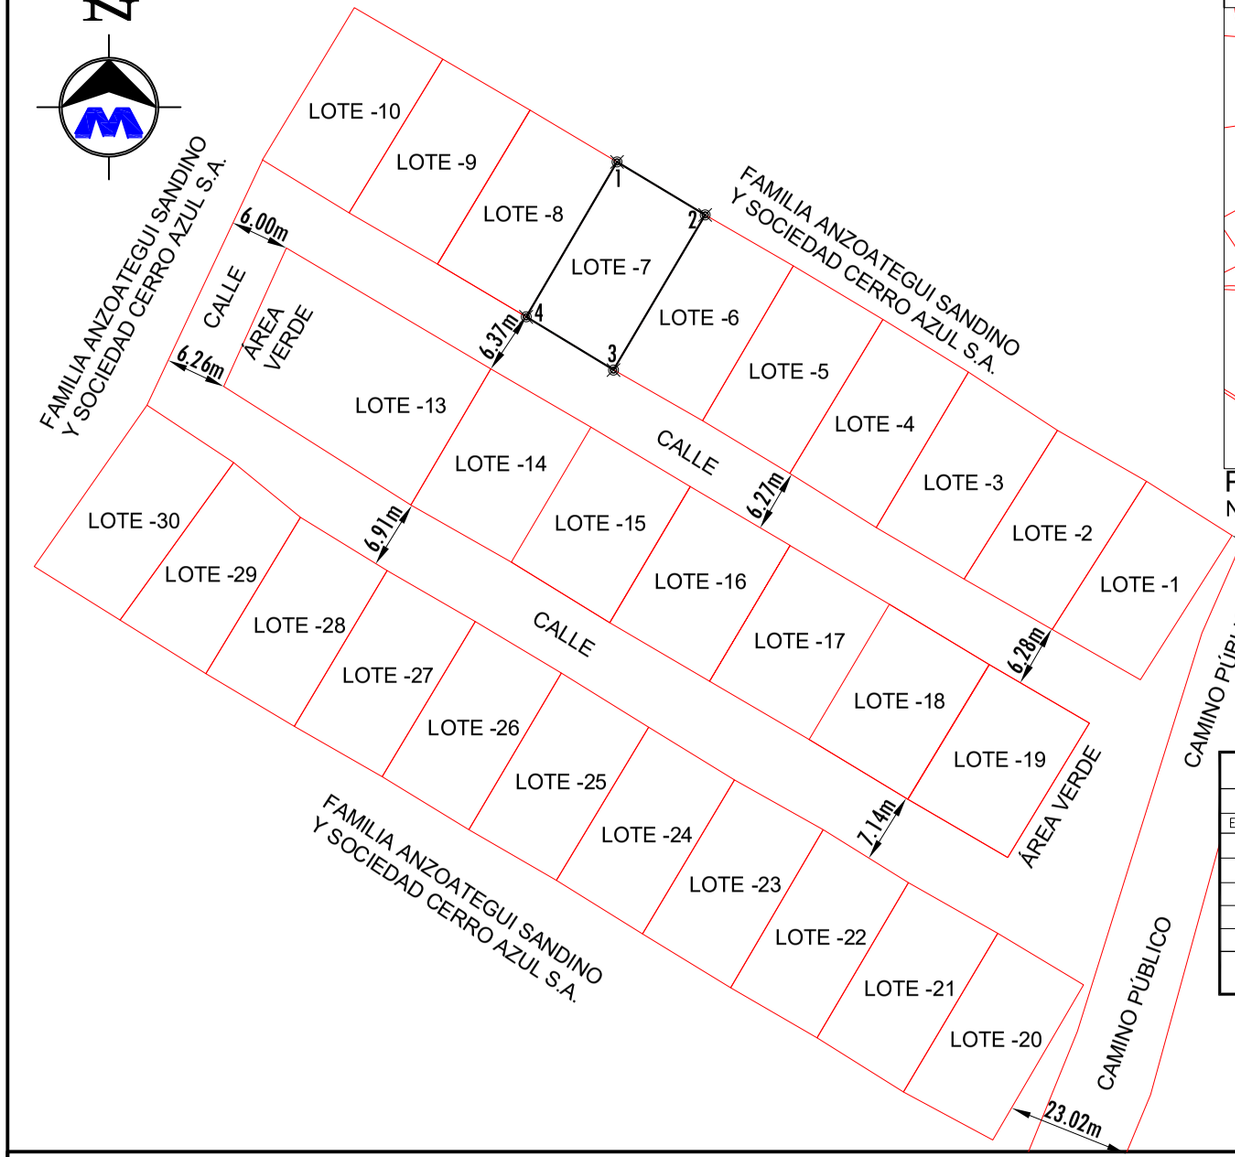

DEPARTAMENTO DE GRANADA MUNICIPIO DE GRANADA

Planta de Ubicación Sin Escala
Número Catastral: 3051-4-05-000-41900

COORDENADAS NO VINCULADAS A LA RED GEODESICA DE NICARAGUA

CUADRO DE CONSTRUCCION LOTE 7

LADO EST	LADO PV	RUMBO	DISTANCIA	V	COORDENADAS Y	COORDENADAS X
				1	1,321,977.1004	613,251.3017
1	2	S 59°02'21.64" E	10.422	2	1,321,971.7390	613,260.2384
2	3	S 30°39'01.57" W	18.209	3	1,321,956.0742	613,250.9557
3	4	N 58°50'59.42" W	10.338	4	1,321,961.4218	613,242.1084
4	1	N 30°23'08.57" E	18.175	1	1,321,977.1004	613,251.3017

SUPERFICIE = 188.817 m2 = 267.82 Vrs2

Objeto Lev: Donación de una parte Indivisa	Número Catastral: 3051-4-05-000-41900		FIRMA:
Enajenante: COOPERTATIVA SERVICIOS Y MANUALIDADES LOS ANGELES R.L. N° RUC: J0810000298664	Ubicación: Antigua Finca Obregon, Camino a los Malacos. Lote-7 Municipio de Granada, Departamento de Granada.		Ejecuta: Ing.Bosco Javier Morgan Lic. Catastral: BMM100426 Cel: 8883-7568 Email: ingmorgan73@gmail.com SERVICIOS TOPOGRAFICOS
Adquiriente: Jonathan Javier Vallecillo Ruiz; Ced: 201-190201-1003K	Área: 188.817 m2 = 267.82 Vrs2	Escala: 1 /700	Fecha: 9 de febrero del 2026

ESPACIO PARA ESQUELA