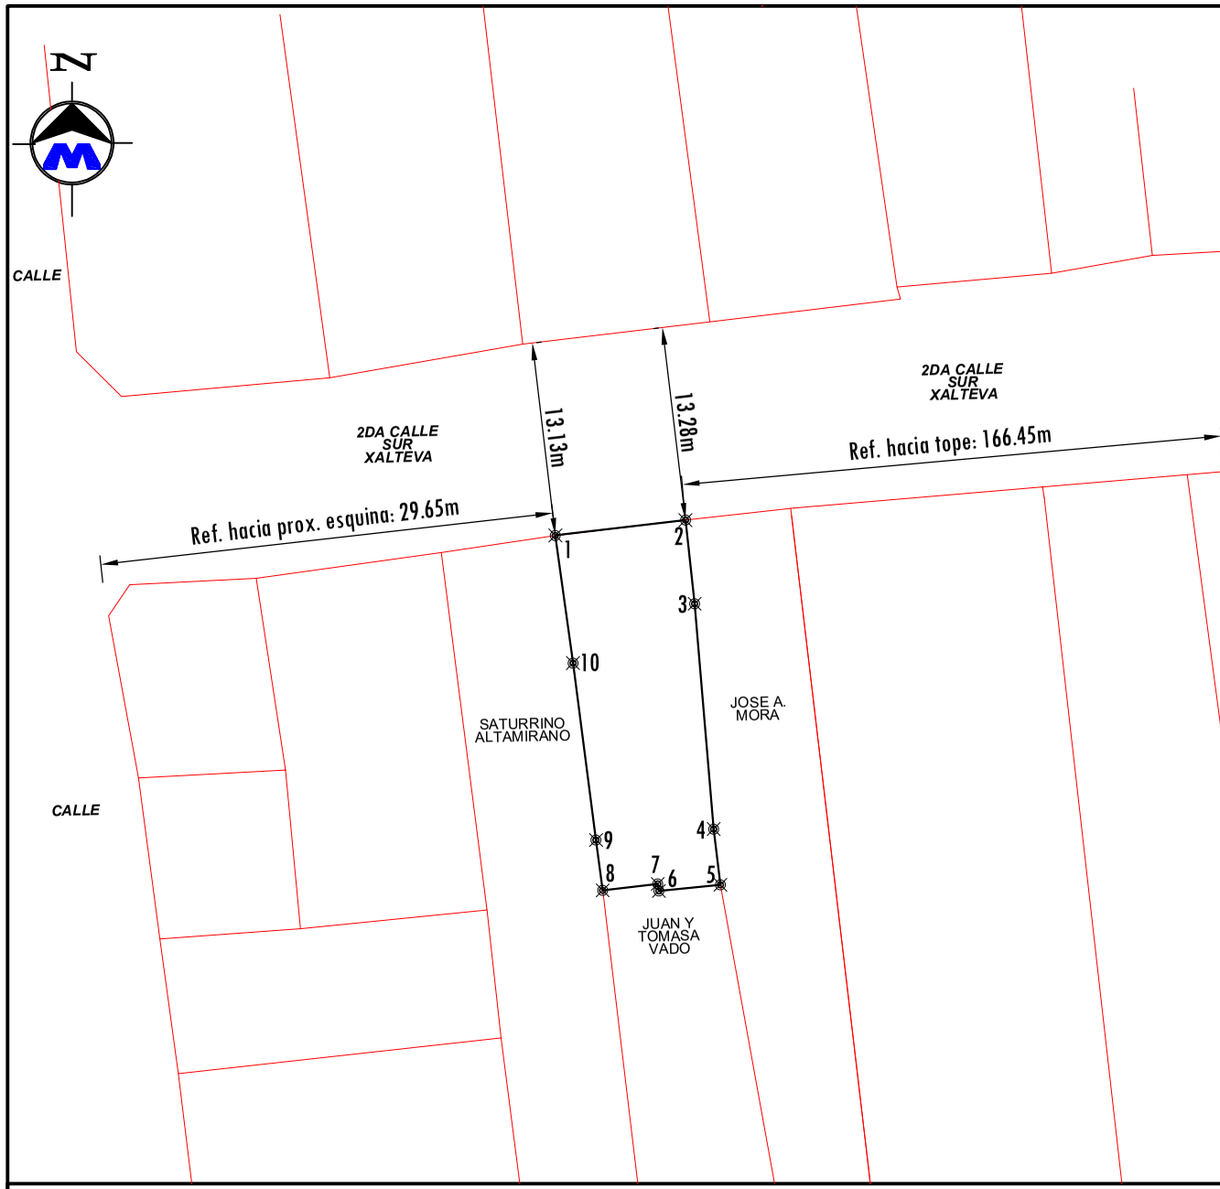

DEPARTAMENTO DE GRANADA MUNICIPIO DE GRANADA

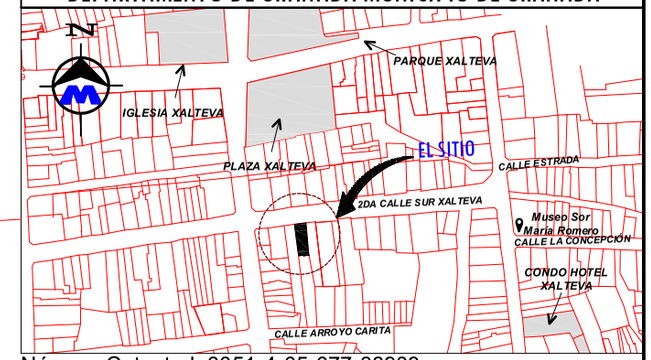

Número Catastral: 3051-4-05-077-38903
Planta de Ubicación Sin Escala

COORDENADAS NO VINCULADAS A LA RED GEODESICA DE NICARAGUA

CUADRO DE CONSTRUCCION

LADO EST	LADO PV	RUMBO	DISTANCIA	V	COORDENADAS Y	COORDENADAS X
				1	1,318,750.4184	613,229.7037
1	2	N 83°22'14.85" E	9.465	2	1,318,751.5111	613,239.1056
2	3	S 06°13'59.29" E	6.087	3	1,318,745.4599	613,239.7665
3	4	S 04°50'50.67" E	16.345	4	1,318,729.1729	613,241.1477
4	5	S 06°55'58.74" E	4.057	5	1,318,725.1457	613,241.6374
5	6	S 84°08'11.31" W	4.478	6	1,318,724.6883	613,237.1830
6	7	N 09°00'22.16" W	0.529	7	1,318,725.2105	613,237.1002
7	8	S 83°13'42.66" W	3.996	8	1,318,724.7393	613,233.1320
8	9	N 07°36'15.53" W	3.666	9	1,318,728.3734	613,232.6468
9	10	N 07°25'30.04" W	12.912	10	1,318,741.1770	613,230.9782
10	1	N 07°51'08.94" W	9.329	1	1,318,750.4184	613,229.7037

SUPERFICIE = 234.609 m2 = 332.77 Vrs2

Objeto Lev: Venta Total	Número Catastral: 3051-4-05-077-38903	FIRMA:
Enajenante: Christian Nicholas James James,Pasaporte: 8 0143 0245 Maria Magdalena Enriquez Angulo, Pasaporte: 8 0081 0763	Ubicación: De Iglesia Xalteva 1c al Sur, ½ c al Este, 2da calle Sur Xalteva. Municipio de Granada, Departamento de Granada.	Ejecuta: Ing.Bosco Javier Morgan Lic. Catastral: BMM100426 Cel: 8883-7568 Email: ingmorgan73@gmail.com
Adquiriente: Jesse Joseph Teschner, Pasaporte: A72809310 Jessica Angelica Alvarado Guevara, Ced: 281-241190-0012K	Área: 234.609 m2 = 332.77 Vrs2 — Escala: 1 / 500	Fecha: 14 de Febrero del 2026

ESPACIO PARA ESQUELA