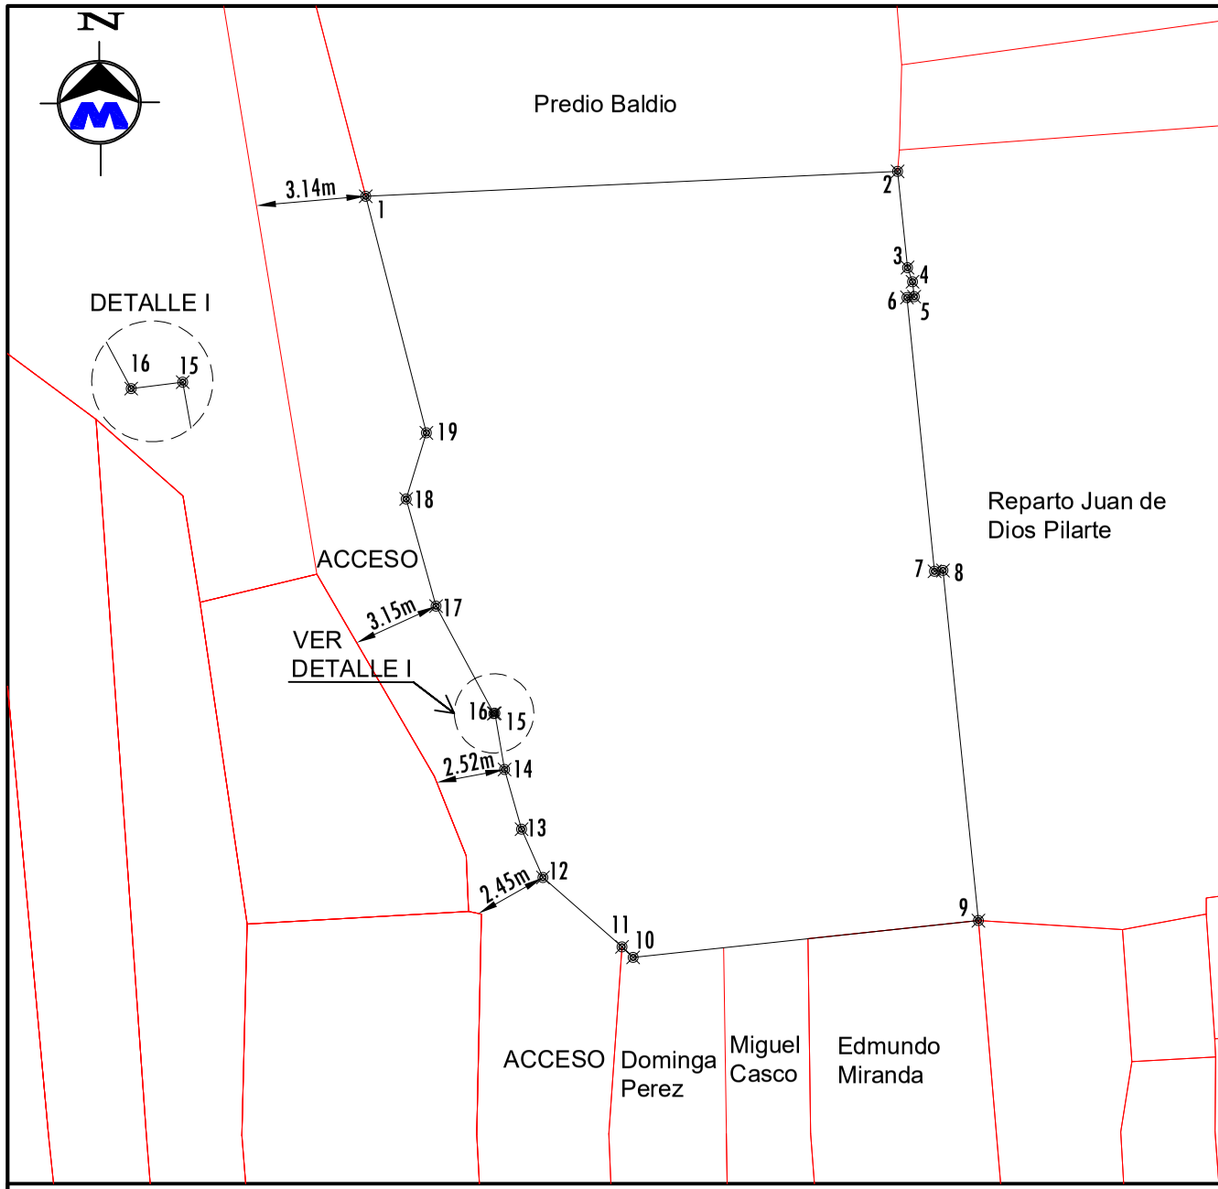

MUNICIPIO DE GRANADA. DEPARTAMENTO DE GRANADA

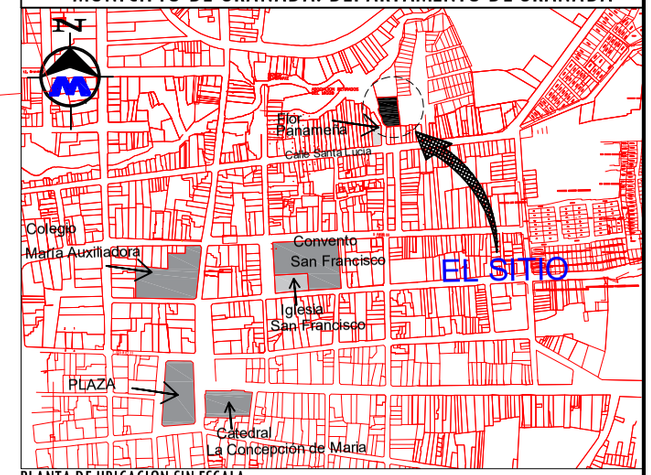

PLANTA DE UBICACION SIN ESCALA

Número Catastral: 6311-4925-8553-10

COORDENADAS NO VINCULADAS A LA RED GEODESICA DE NICARAGUA

CUADRO DE CONSTRUCCION

LADO EST	LADO PV	RUMBO	DISTANCIA	V	COORDENADAS Y	COORDENADAS X
				1	1,319,586.9226	614,266.9198
1	2	N 87°19'12.29" E	38.485	2	1,319,588.7220	614,305.3623
2	3	S 05°46'46.18" E	7.000	3	1,319,581.7576	614,306.0672
3	4	S 19°59'43.24" E	1.080	4	1,319,580.7427	614,306.4365
4	5	S 05°46'33.23" E	1.100	5	1,319,579.6483	614,306.5472
5	6	S 84°13'36.86" W	0.520	6	1,319,579.5960	614,306.0299
6	7	S 05°46'44.71" E	19.910	7	1,319,559.7872	614,308.0347
7	8	N 84°13'18.97" E	0.600	8	1,319,559.8476	614,308.6316
8	9	S 05°46'45.20" E	25.445	9	1,319,534.5319	614,311.1938
9	10	S 83°54'34.10" W	25.100	10	1,319,531.8688	614,286.2355
10	11	N 46°22'53.88" W	1.220	11	1,319,532.7104	614,285.3523
11	12	N 48°46'45.54" W	7.490	12	1,319,537.6461	614,279.7184
12	13	N 23°46'41.11" W	3.830	13	1,319,541.1509	614,278.1742
13	14	N 15°48'04.20" W	4.480	14	1,319,545.4616	614,276.9543
14	15	N 09°58'50.65" W	4.130	15	1,319,549.5291	614,276.2385
15	16	S 80°04'00.12" W	0.080	16	1,319,549.5153	614,276.1597
16	17	N 28°11'29.34" W	8.800	17	1,319,557.2714	614,272.0024
17	18	N 15°37'54.33" W	8.060	18	1,319,565.0333	614,269.8306
18	19	N 17°08'07.13" E	4.990	19	1,319,569.8018	614,271.3008
19	1	N 14°21'11.85" W	17.672	1	1,319,586.9226	614,266.9198

SUPERFICIE = 1,924.350 m2 = 2,729.53 Vrs2

Objeto: Mensura Judicial	Número Catastral: 6311-4925-8553-10		FIRMA:
Propietario: Jose Luis Marcia Ordoñez, Ced: 201-031153-0001M	**Ubicación:** De la Flor Panameña 31.52m al Norte. Municipio de Granada, Departamento de Granada.		Ejecuta: Ing.Bosco Javier Morgan Lic. Catastral: BMM100426 Cel: 8883-7568 Email: ingmorgan73@gmail.com www.morganconstrucciones.com
Factor de escala: 1.418415	Área: 1,924.350 m2 = 2,729.53 Vrs2	Escala: 1: 500	Fecha:07 de Febrero del 2026

ESPACIO PARA ESQUELA