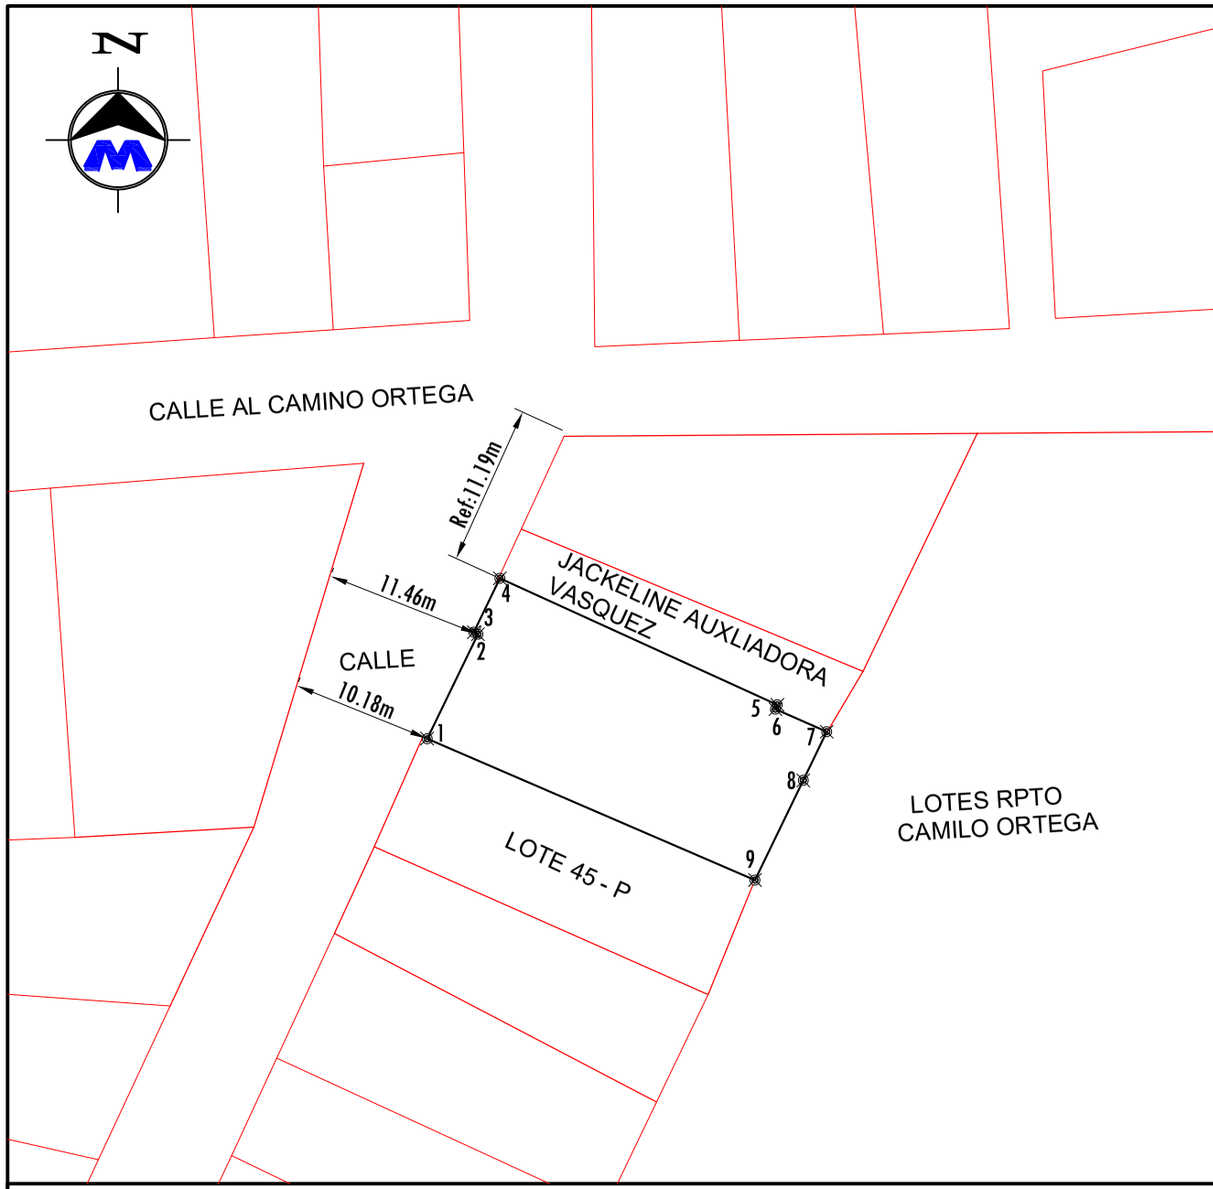

DEPARTAMENTO DE GRANADA MUNICIPIO DE GRANADA

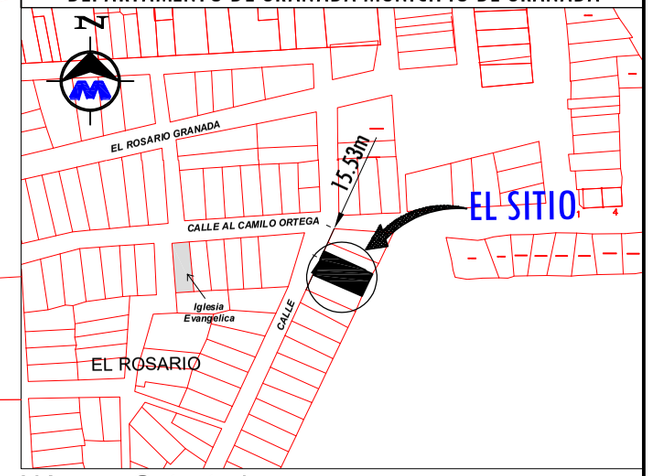

Número Catastral:
63113820272417 / 63113820169814
Planta de Ubicación Sin Escala

COORDENADAS NO VINCULADAS A LA RED GEODESICA DE NICARAGUA

CUADRO DE CONSTRUCCION

LADO EST	LADO PV	RUMBO	DISTANCIA	V	COORDENADAS Y	COORDENADAS X
				1	1,318,076.2143	613,212.4098
1	2	N 25°51'49.97" E	8.400	2	1,318,083.7729	613,216.0742
2	3	N 65°45'39.72" W	0.324	3	1,318,083.9061	613,215.7784
3	4	N 25°45'45.94" E	4.334	4	1,318,087.8090	613,217.6620
4	5	S 65°28'42.45" E	22.051	5	1,318,078.6569	613,237.7245
5	6	S 23°46'14.29" W	0.339	6	1,318,078.3464	613,237.5878
6	7	S 66°13'45.71" E	4.046	7	1,318,076.7157	613,241.2904
7	8	S 25°34'58.56" W	3.910	8	1,318,073.1890	613,239.6020
8	9	S 25°51'19.95" W	8.000	9	1,318,065.9898	613,236.1132
9	1	N 66°40'01.08" W	25.815	1	1,318,076.2143	613,212.4098

SUPERFICIE = 321.55 m2 = 456.09 Vrs2

ESPACIO PARA ESQUELA

Objeto Lev: Fusión	Número Catastral: 63113820272417 / 63113820169814		FIRMA:
Propietario: Josefa del Carmen Vasquez Vega Ced: 203-180457-0000L	Ubicación: Rpto. Rosario, Iglesia Evangelica 1c al Este y 11.19m al Suroeste. Municipio de Granada, Departamento de Granada.		Ejecuta: Ing.Bosco Javier Morgan Lic. Catastral: BMM100426 Cel: 8883-7568 Email: ingmorgan73@gmail.com servicios topograficos
Factor de escala: 1.418415	Área: 321.55 m2 = 456.09 Vrs2	Escala: 1 / 500	Fecha: 14 de Febrero 2025