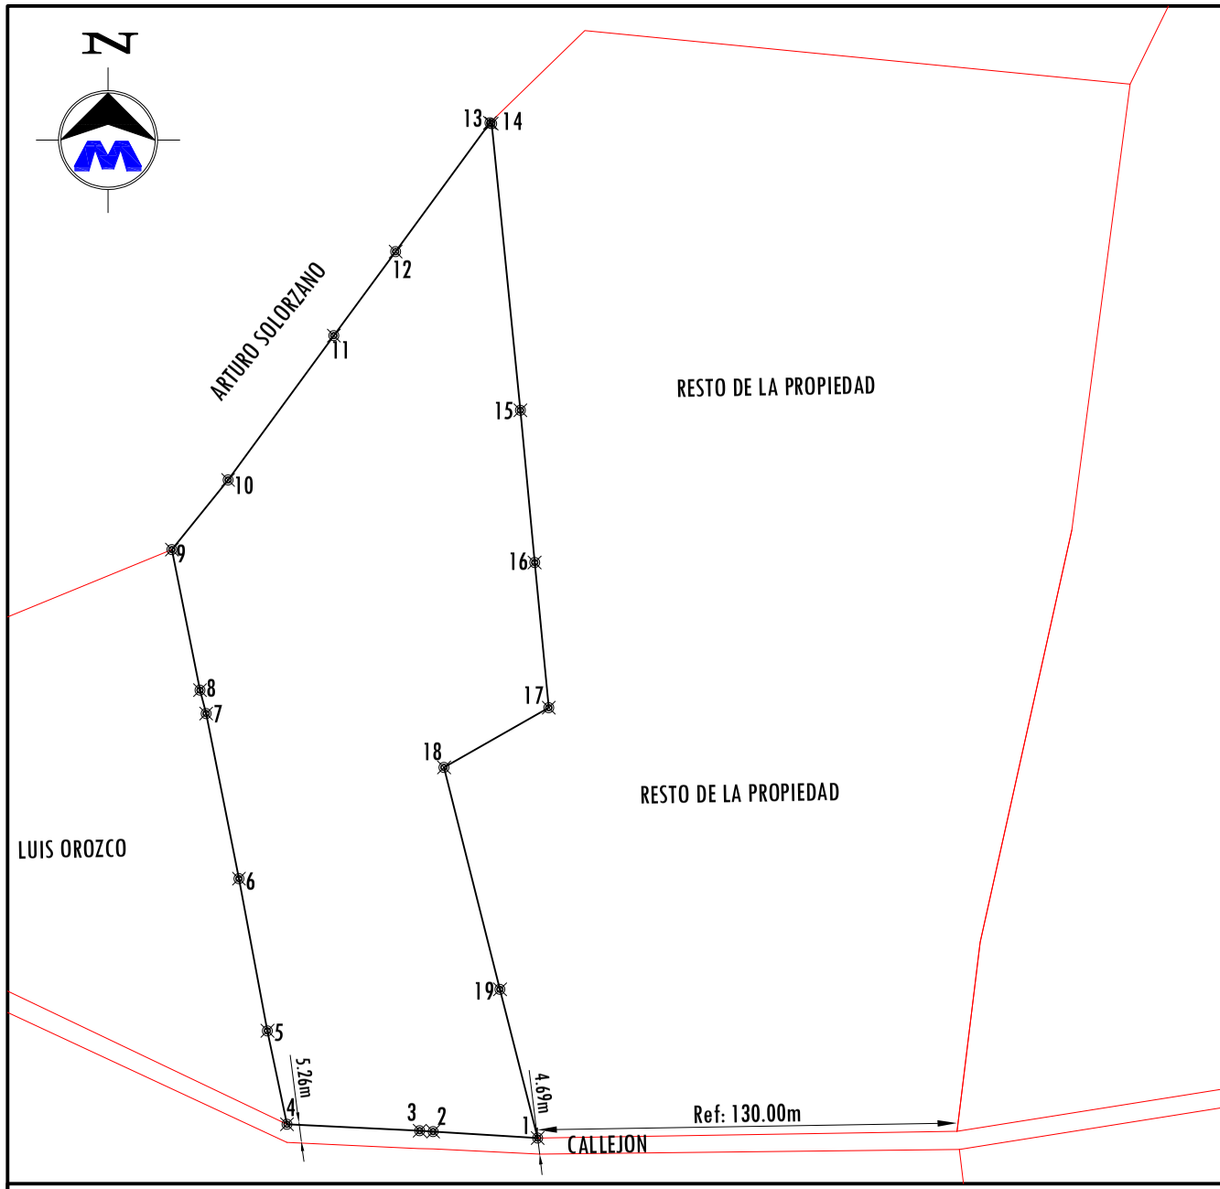

DEPARTAMENTO DE GRANADA MUNICIPIO DE GRANADA

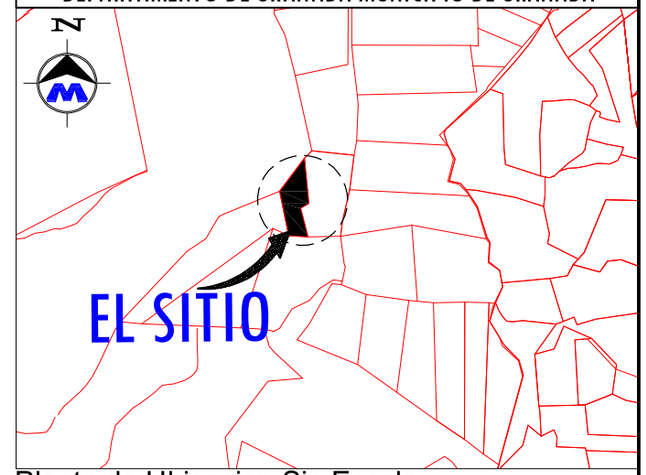

Planta de Ubicacion Sin Escala
Número Catastra: 3051-4-09-000-05929

COORDENADAS NO VINCULADAS A LA RED GEODESICA DE NICARAGUA

CUADRO DE CONSTRUCCION

LADO EST	LADO PV	RUMBO	DISTANCIA	V	COORDENADAS Y	COORDENADAS X
				1	1,314,016.0754	612,790.7771
1	2	N 86°28'24.42" W	30.286	2	1,314,017.9383	612,760.5489
2	3	N 86°06'21.23" W	3.841	3	1,314,018.1992	612,756.7169
3	4	N 87°14'52.55" W	38.470	4	1,314,020.0463	612,718.2914
4	5	N 11°42'41.20" W	27.641	5	1,314,047.1117	612,712.6807
5	6	N 10°36'17.10" W	44.754	6	1,314,091.1014	612,704.4445
6	7	N 11°14'58.31" W	48.712	7	1,314,138.8770	612,694.9418
7	8	N 14°30'20.28" W	6.954	8	1,314,145.6098	612,693.1999
8	9	N 11°20'31.30" W	41.510	9	1,314,186.3093	612,685.0362
9	10	N 38°57'14.67" E	25.871	10	1,314,206.4280	612,701.3013
10	11	N 36°14'20.58" E	51.748	11	1,314,248.1654	612,731.8922
11	12	N 36°14'26.91" E	30.189	12	1,314,272.5139	612,749.7392
12	13	N 36°09'49.40" E	46.139	13	1,314,309.7634	612,776.9656
13	14	S 66°17'53.71" E	0.592	14	1,314,309.5256	612,777.5073
14	15	S 05°42'01.16" E	83.313	15	1,314,226.6248	612,785.7823
15	16	S 05°21'41.15" E	44.233	16	1,314,182.5857	612,789.9154
16	17	S 05°36'48.06" E	42.213	17	1,314,140.5748	612,794.0444
17	18	S 60°17'05.43" W	34.893	18	1,314,123.2786	612,763.7395
18	19	S 14°08'21.55" E	66.198	19	1,314,059.0864	612,779.9103
19	1	S 14°10'45.03" E	44.362	1	1,314,016.0754	612,790.7771

SUPERFICIE = 19,732.799 m2 = 27,989.30 Vrs2

Objeto Lev: Venta Parcial	Número Catastral: 3051-4-09-000-05929	Fecha: 13 de Febrero del 2026	FIRMA:
Enajenante: Luis ALberto Montalvan Sandoval Cédula: 201-260142-0003J	Ubicación: De las Pilas 150m al Este. Cmca la Joya. Mombacho. Municipio de Granada, Departamento de Granada	Ejecuta: Ing.Bosco Javier Morgan Lic. Catastral: BMM100426 Cel: 8883-7568 Email: ingmorgan73@gmail.com servicios topograficos	
Adquiere: Leonor del Carmen Montalban Sandoval c.c. Leonor Montalvan Sandoval Cédula: 201-180146-0002T	Área: 19,732.799 m2 = 27,989.30 Vrs2	Escala: 1 / 2000	

ESPACIO PARA ESQUELA