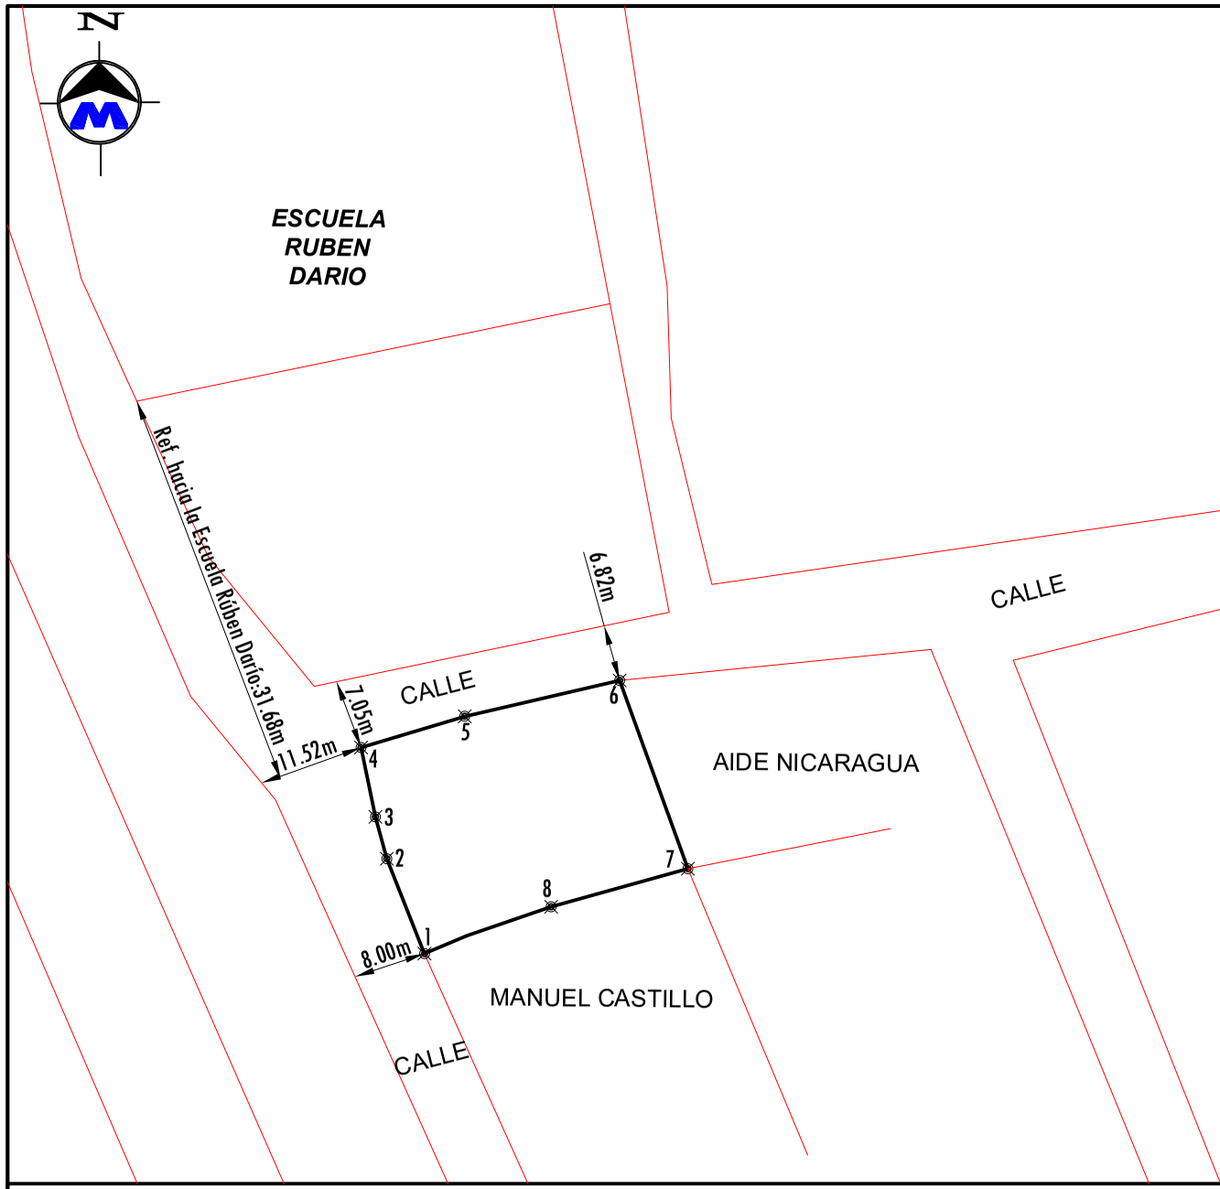

MUNICIPIO DE NANDAIME. DEPARTAMENTO DE GRANADA

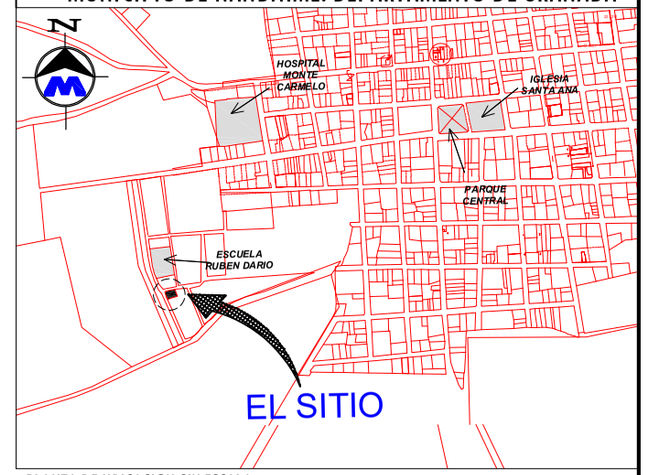

PLANTA DE UBICACION SIN ESCALA

Numero Catastral: 2951-2-08-000-19301

COORDENADAS NO VINCULADAS A LA RED GEODESICA DE NICARAGUA

CUADRO DE CONSTRUCCION

LADO EST	LADO PV	RUMBO	DISTANCIA	V	COORDENADAS Y	COORDENADAS X
				1	1,299,427.8929	602,597.5664
1	2	N 21°36'25.43" W	7.385	2	1,299,434.7585	602,594.8471
2	3	N 15°18'36.93" W	3.142	3	1,299,437.7885	602,594.0176
3	4	N 11°35'29.25" W	5.121	4	1,299,442.8055	602,592.9885
4	5	N 73°16'41.67" E	7.818	5	1,299,445.0548	602,600.4755
5	6	N 76°56'29.56" E	11.491	6	1,299,447.6511	602,611.6693
6	7	S 19°56'31.95" E	14.485	7	1,299,434.0345	602,616.6098
7	8	S 74°24'53.71" W	10.265	8	1,299,431.2765	602,606.7218
8	9	S 70°59'29.13" W	6.442	9	1,299,429.1781	602,600.6308
9	1	S 67°14'46.00" W	3.323	1	1,299,427.8929	602,597.5664

SUPERFICIE = 298.357 m2 = 423.19 Vrs2

Objeto: Donación Total	Número Catastral: 2951-2-08-000-19301		FIRMA:
Enajenante: Augusto de Jesus Tercero Traña; Ced: 202-061065-0003R Lilliam del Socorro Mendoza; Ced: 001-130373-0030B	Ubicación:De la escuela Rúben Darío 31.68m al Sur Municipio de Nandaime, Departamento de Granada.		Ejecuta: Ing.Bosco Javier Morgan Lic. Catastral: BMM100426 Cel: 8883-7568 Email: ingmorgan73@gmail.com www.morganconstrucciones.com
Adquiriente: Walmer Jose Tercero Montoya Ced: 202-190690-0001F	Área = 298.357 m2 = 423.19 Vrs2	Escala: 1:500	Fecha: 16 de Febrero del 2026

ESPACIO PARA ESQUELA