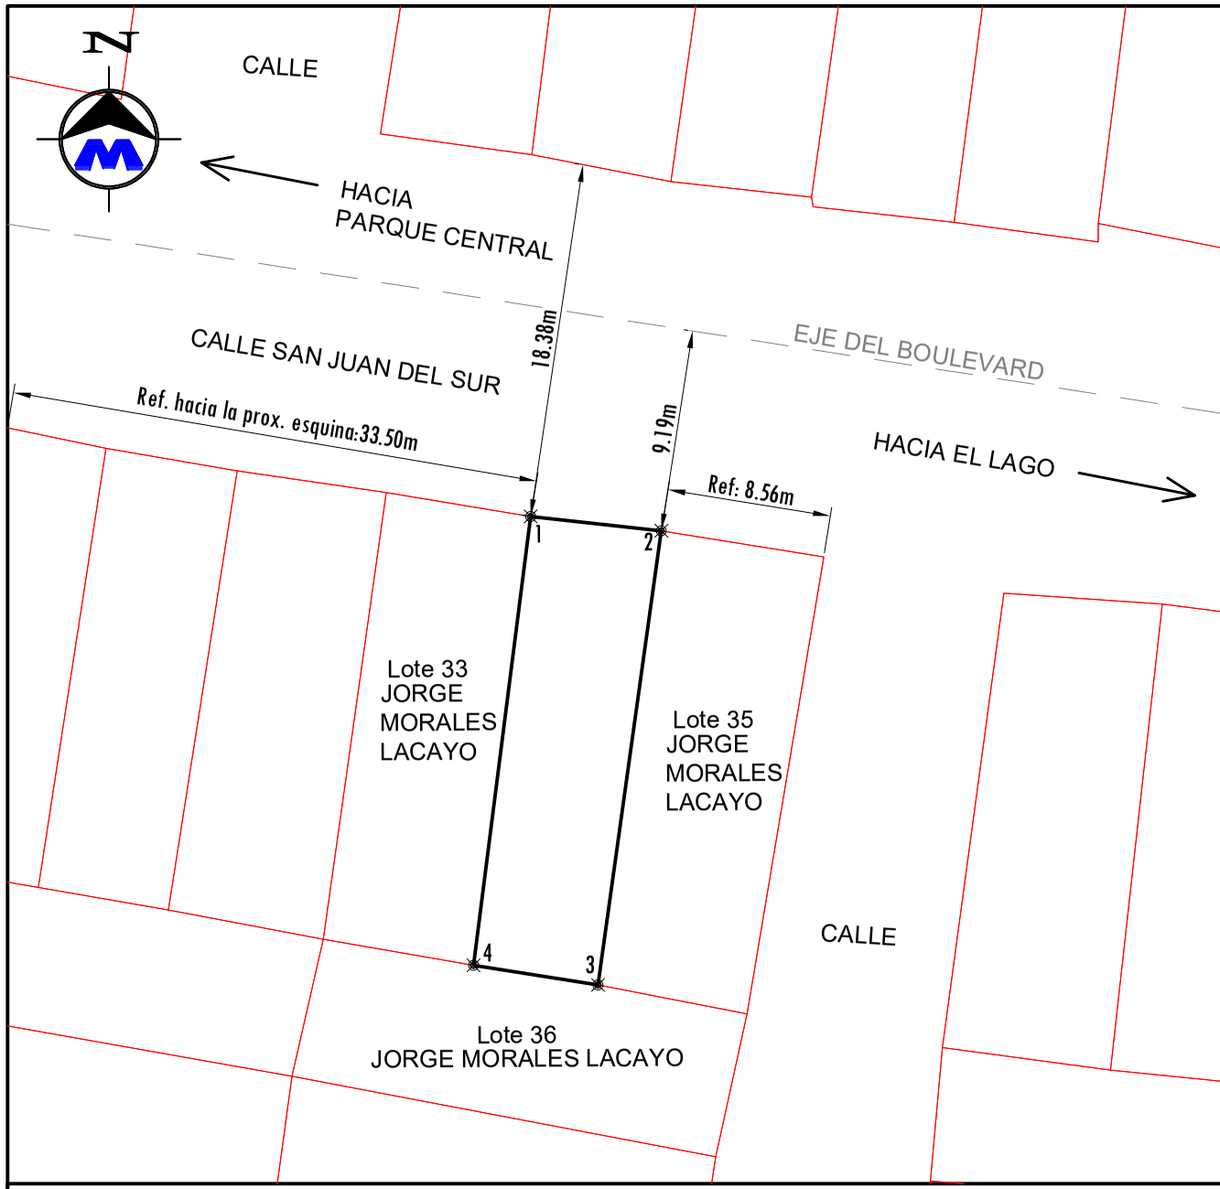

DEPARTAMENTO DE GRANADA MUNICIPIO DE GRANADA

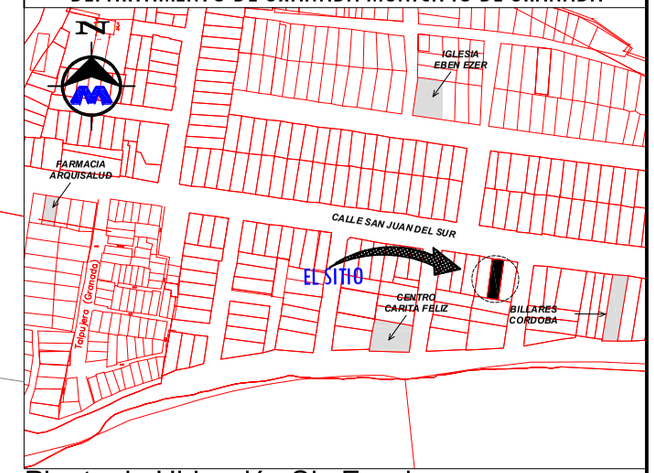

Planta de Ubicación Sin Escala
Número Catastral: 3051-4-05-079-20400

COORDENADAS NO VINCULADAS A LA RED GEODESICA DE NICARAGUA

CUADRO DE CONSTRUCCION

LADO EST	LADO PV	RUMBO	DISTANCIA	V	COORDENADAS Y	COORDENADAS X
				1	1,318,794.5620	614,980.2454
1	2	S 83°44'04.86" E	7.605	2	1,318,793.7320	614,987.8054
2	3	S 07°55'42.78" W	26.534	3	1,318,767.4520	614,984.1454
3	4	N 81°00'10.28" W	7.290	4	1,318,768.5920	614,976.9454
4	1	N 07°14'30.29" E	26.179	1	1,318,794.5620	614,980.2454

SUPERFICIE = 196.230 m2 = 278.34 Vrs2

Objeto Lev: Verificación de área	Número Catastral: 3051-4-05-079-20400		FIRMA:
Propietario: William Tyrone Zambrana Dominguez Ced: 201-240564-00107T	Ubicación: Del Centro Carita Feliz 51.12m al N, 33.50 m al E. Municipio de Granada, Departamento de Granada.		Ejecuta: Ing.Bosco Javier Morgan Lic. Catastral: BMM100426 Cel: 8883-7568 Email: ingmorgan73@gmail.com SERVICIOS TOPOGRAFICOS
Factor de escala: 1.418415	Área: 196.230 m2 = 278.34 Vrs2	Escala: 1 /400	Fecha: 23 de Enero del 2026

ESPACIO PARA ESQUELA