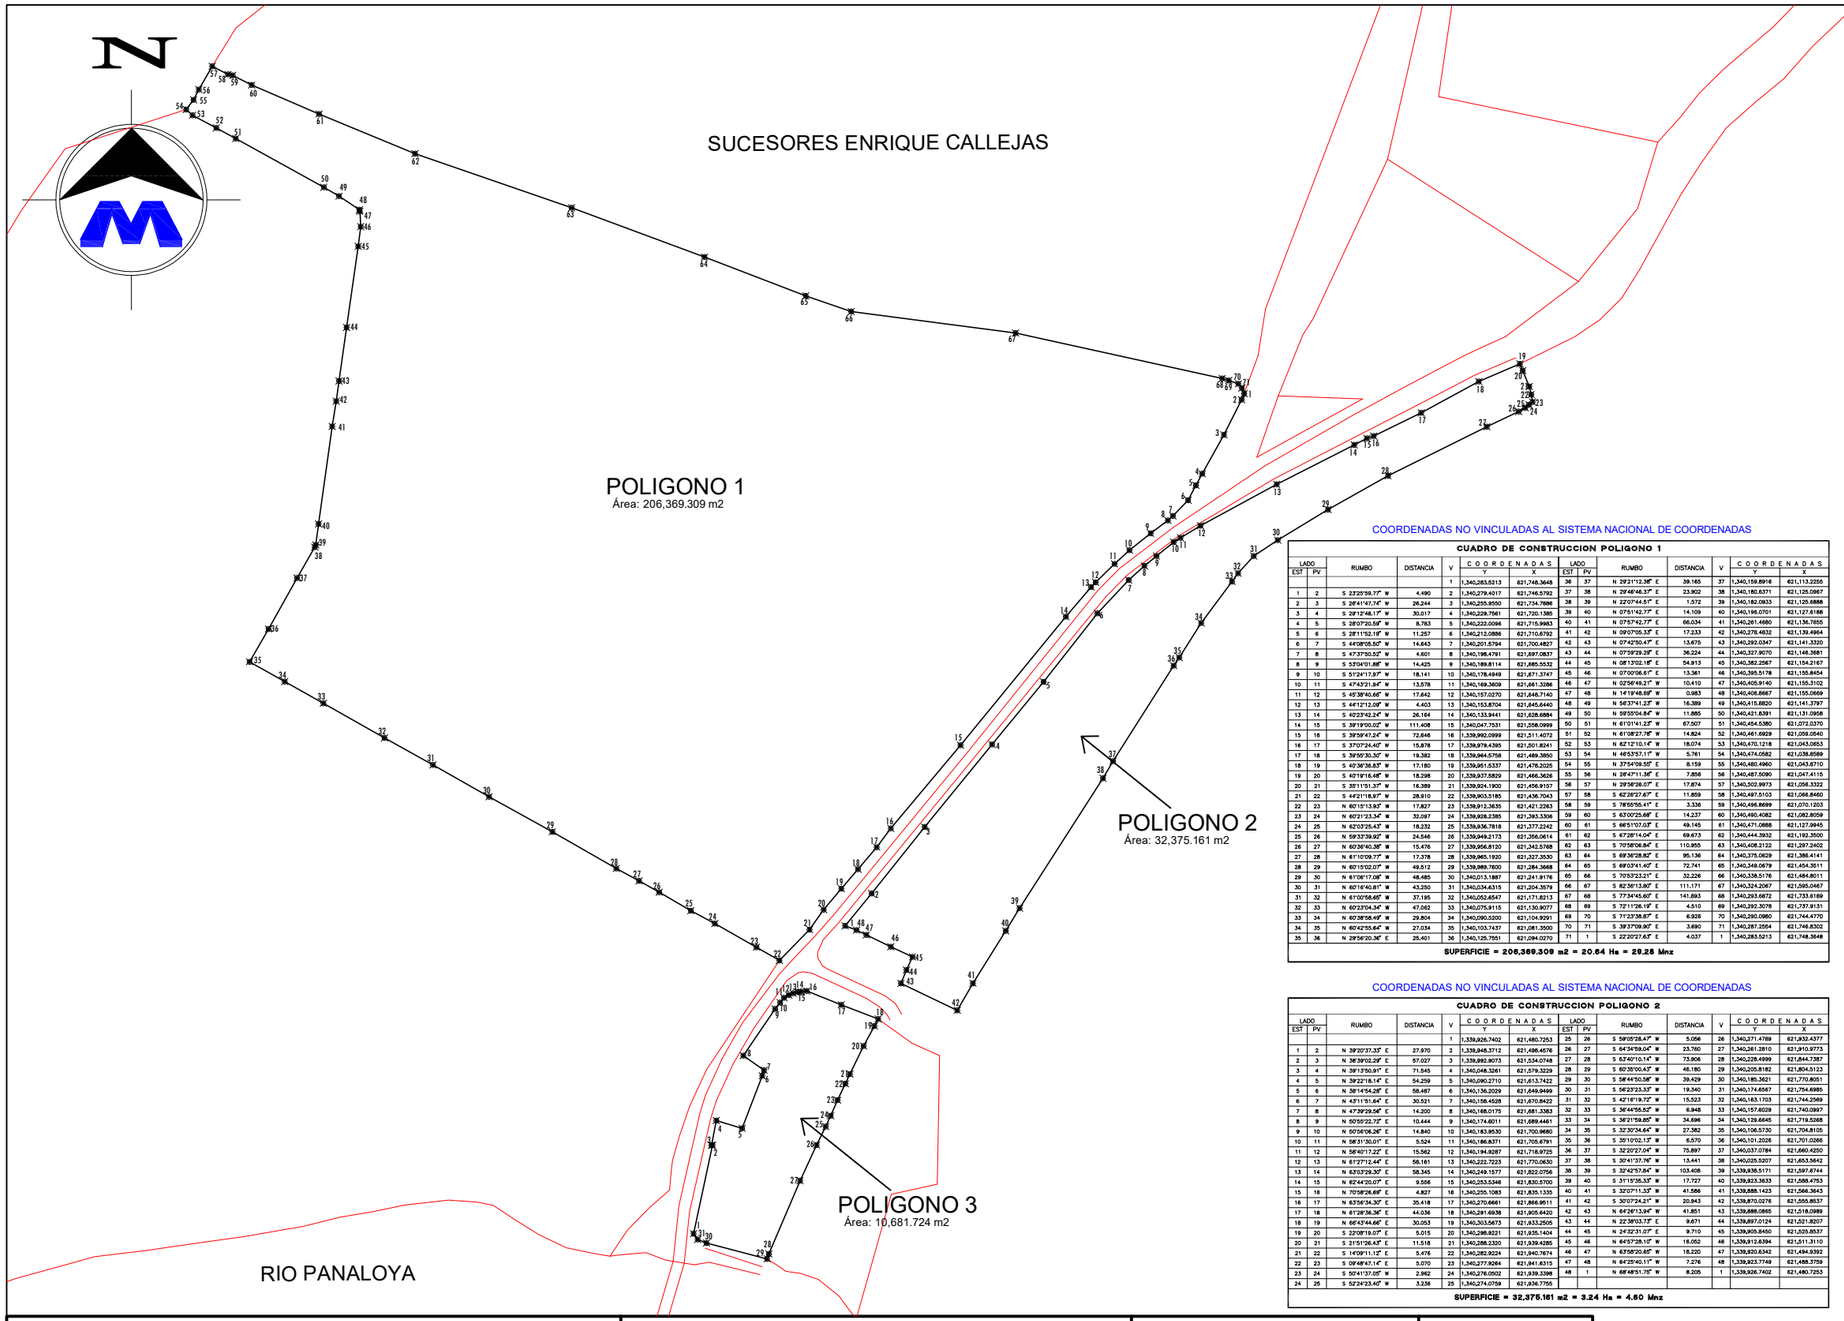

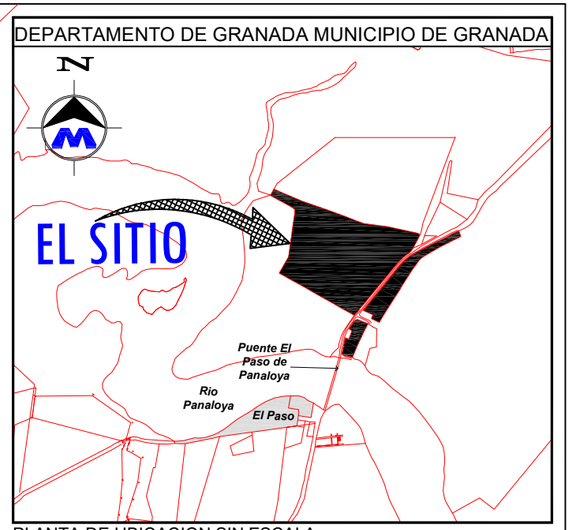

PLANTA DE UBICACION SIN ESCALA
Número Catastral: 3052-3-06-000-01101

COORDENADAS NO VINCULADAS AL SISTEMA NACIONAL DE COORDENADAS

CUADRO DE CONSTRUCCION POLIGONO 1

LADO EST	LADO PV	RUMBO	DISTANCIA	V	COORDENADAS Y	COORDENADAS X	LADO EST	LADO PV	RUMBO	DISTANCIA	V	COORDENADAS Y	COORDENADAS X
				1	1,340,283.5213	621,748.3648	36	37	N 29°21'12.38" E	39.165	37	1,340,159.8916	621,113.2255
1	2	S 23°25'59.77" W	4.490	2	1,340,279.4017	621,746.5792	37	38	N 29°46'46.37" E	23.902	38	1,340,180.6371	621,125.0967
2	3	S 28°41'47.74" W	26.244	3	1,340,255.9550	621,734.7886	38	39	N 22°07'44.51" E	1.572	39	1,340,182.0933	621,125.6888
3	4	S 29°12'48.17" W	30.017	4	1,340,229.7561	621,720.1385	39	40	N 07°51'42.77" E	14.109	40	1,340,196.0701	621,127.6188
4	5	S 28°07'20.59" W	8.763	5	1,340,223.0096	621,715.9983	40	41	N 07°57'42.77" E	66.034	41	1,340,261.4680	621,136.7655
5	6	S 28°11'52.19" W	11.257	6	1,340,212.0886	621,710.6792	41	42	N 09°07'05.33" E	17.233	42	1,340,278.4832	621,139.4964
6	7	S 44°08'05.50" W	14.643	7	1,340,201.5794	621,700.4827	42	43	N 07°42'50.47" E	13.675	43	1,340,292.0347	621,141.3320
7	8	S 47°37'50.52" W	4.601	8	1,340,198.4791	621,697.0837	43	44	N 07°59'29.39" E	36.224	44	1,340,327.9070	621,146.3881
8	9	S 53°04'01.88" W	14.425	9	1,340,189.8114	621,685.5532	44	45	N 08°13'02.18" E	54.913	45	1,340,382.2567	621,154.2167
9	10	S 51°24'11.97" W	18.141	10	1,340,178.6849	621,671.3747	45	46	N 07°00'06.61" E	13.361	46	1,340,395.5178	621,155.8454
10	11	S 47°43'21.94" W	13.576	11	1,340,169.3609	621,661.3286	46	47	N 02°56'49.21" W	10.410	47	1,340,405.8140	621,155.3102
11	12	S 45°39'40.66" W	17.642	12	1,340,157.0270	621,648.7140	47	48	N 14°19'48.68" W	0.983	48	1,340,406.8667	621,155.0669
12	13	S 44°12'12.09" W	4.403	13	1,340,153.8704	621,645.8440	48	49	N 58°37'41.23" W	16.389	49	1,340,415.8820	621,141.3797
13	14	S 42°23'42.24" W	26.164	14	1,340,133.8441	621,628.6884	49	50	N 59°50'04.84" W	11.885	50	1,340,421.8391	621,131.0956
14	15	S 39°19'00.02" W	111.408	15	1,340,047.7531	621,558.0999	50	51	N 61°01'41.33" W	67.507	51	1,340,454.5380	621,072.0370
15	16	S 39°59'47.24" W	72.646	16	1,339,992.0999	621,511.4072	51	52	N 61°08'27.78" W	14.824	52	1,340,461.6929	621,059.0540
16	17	S 37°07'24.40" W	15.878	17	1,339,979.4395	621,501.8241	52	53	N 62°12'10.16" W	18.074	53	1,340,470.1218	621,043.0653
17	18	S 39°55'30.30" W	19.382	18	1,339,964.5758	621,489.3850	53	54	N 45°57'51.11" W	5.761	54	1,340,474.0582	621,038.8589
18	19	S 40°36'58.83" W	17.180	19	1,339,951.5337	621,478.3025	54	55	N 37°54'09.55" E	8.159	55	1,340,480.4960	621,043.8710
19	20	S 42°19'16.48" W	18.298	20	1,339,937.5829	621,466.3626	55	56	N 28°47'11.36" E	7.856	56	1,340,487.5090	621,047.4115
20	21	S 35°11'51.37" W	16.389	21	1,339,924.1900	621,456.9157	56	57	N 29°56'26.07" E	17.874	57	1,340,502.8973	621,056.3322
21	22	S 44°21'18.97" W	28.910	22	1,339,903.5185	621,436.7043	57	58	S 62°39'27.67" E	11.859	58	1,340,497.5103	621,066.8440
22	23	N 60°15'13.93" W	17.827	23	1,339,912.3635	621,421.2263	58	59	S 78°55'55.41" E	3.336	59	1,340,496.8699	621,070.1203
23	24	N 60°21'23.34" W	32.097	24	1,339,928.2385	621,393.3306	59	60	S 63°00'25.66" E	14.237	60	1,340,490.4082	621,082.8059
24	25	N 62°37'25.43" W	18.232	25	1,339,936.7818	621,377.2242	60	61	S 66°51'07.03" E	49.145	61	1,340,471.0888	621,127.9945
25	26	N 59°37'39.92" W	24.546	26	1,339,949.2173	621,356.0614	61	62	S 67°28'14.04" E	69.673	62	1,340,444.3032	621,192.3500
26	27	N 60°36'40.38" W	15.476	27	1,339,956.8120	621,342.5768	62	63	S 70°58'06.84" E	110.955	63	1,340,408.2122	621,297.2402
27	28	N 61°10'09.77" W	17.378	28	1,339,965.1920	621,327.3530	63	64	S 69°36'28.82" E	95.136	64	1,340,375.0629	621,386.4141
28	29	N 60°15'02.07" W	49.512	29	1,339,989.7600	621,284.3668	64	65	S 69°03'41.40" E	72.741	65	1,340,349.0679	621,454.3511
29	30	N 61°06'17.06" W	48.485	30	1,340,013.1887	621,241.9176	65	66	S 70°52'23.21" E	32.226	66	1,340,338.5176	621,484.8011
30	31	N 60°16'40.81" W	43.250	31	1,340,034.4315	621,204.3579	66	67	S 82°36'13.80" E	111.171	67	1,340,324.2067	621,595.0467
31	32	N 61°00'56.66" W	37.195	32	1,340,052.6547	621,171.8213	67	68	S 77°54'45.60" E	141.893	68	1,340,293.6672	621,733.6189
32	33	N 60°23'04.34" W	47.062	33	1,340,075.9115	621,130.9077	68	69	S 72°11'06.19" E	4.510	69	1,340,292.3078	621,737.9131
33	34	N 60°38'58.49" W	29.804	34	1,340,090.5200	621,104.9291	69	70	S 7°23'38.87" E	6.926	70	1,340,290.0860	621,744.4770
34	35	N 60°42'55.44" W	27.034	35	1,340,103.7437	621,081.3500	70	71	S 39°37'09.90" E	3.690	71	1,340,287.2564	621,746.8302
35	36	N 29°56'20.36" E	25.401	36	1,340,125.7551	621,094.0270	71	1	S 22°20'27.67" E	4.037	1	1,340,283.5213	621,748.3648

SUPERFICIE = 206,369.309 m2 = 20.64 Ha = 29.28 Mnz

COORDENADAS NO VINCULADAS AL SISTEMA NACIONAL DE COORDENADAS

CUADRO DE CONSTRUCCION POLIGONO 2

LADO EST	LADO PV	RUMBO	DISTANCIA	V	COORDENADAS Y	COORDENADAS X	LADO EST	LADO PV	RUMBO	DISTANCIA	V	COORDENADAS Y	COORDENADAS X
				1	1,339,826.7402	621,480.7253	25	26	S 59°05'28.47" W	5.056	26	1,340,271.4789	621,932.4377
1	2	N 39°20'37.33" E	27.970	2	1,339,848.3712	621,498.4576	26	27	S 64°34'59.04" W	23.760	27	1,340,261.2810	621,910.9773
2	3	N 38°39'02.29" E	57.027	3	1,339,892.9073	621,534.0748	27	28	S 63°40'10.14" W	73.906	28	1,340,228.4999	621,844.7387
3	4	N 39°13'50.91" E	71.545	4	1,340,048.3261	621,579.3229	28	29	S 60°30'00.43" W	46.180	29	1,340,205.8182	621,804.5123
4	5	N 39°22'18.14" E	54.259	5	1,340,090.2710	621,613.7422	29	30	S 58°44'50.58" W	39.429	30	1,340,185.3621	621,770.8051
5	6	N 38°14'54.28" E	58.487	6	1,340,136.2029	621,649.9499	30	31	S 56°23'33.53" W	18.340	31	1,340,174.6567	621,754.4985
6	7	N 43°11'51.44" E	30.521	7	1,340,158.4528	621,670.8422	31	32	S 42°18'19.72" W	15.523	32	1,340,163.1703	621,744.2569
7	8	N 47°39'29.58" E	14.200	8	1,340,168.0175	621,681.3383	32	33	S 36°44'55.52" W	6.948	33	1,340,157.6029	621,740.0997
8	9	N 50°59'22.72" E	10.444	9	1,340,174.6011	621,689.4461	33	34	S 36°21'59.85" W	34.696	34	1,340,129.6645	621,719.5268
9	10	N 50°58'06.26" E	14.840	10	1,340,183.9530	621,700.9680	34	35	S 32°30'34.64" W	27.382	35	1,340,106.5730	621,704.8105
10	11	N 58°31'30.01" E	5.524	11	1,340,186.8371	621,705.6791	35	36	S 35°10'02.13" W	6.570	36	1,340,101.2026	621,701.0266
11	12	N 58°40'17.22" E	15.562	12	1,340,194.9287	621,718.9725	36	37	S 32°20'27.04" W	75.897	37	1,340,037.0784	621,660.4250
12	13	N 61°27'12.44" E	58.161	13	1,340,222.7223	621,770.0630	37	38	S 30°41'37.76" W	13.441	38	1,340,025.5207	621,653.5642
13	14	N 63°07'29.30" E	58.345	14	1,340,248.1577	621,822.0754	38	39	S 32°42'57.84" W	103.408	39	1,339,938.1571	621,597.6744
14	15	N 62°44'20.07" E	9.556	15	1,340,253.5346	621,830.5700	39	40	S 31°19'35.33" W	17.727	40	1,339,923.3633	621,588.4753
15	16	N 70°58'26.69" E	4.827	16	1,340,255.1083	621,835.1335	40	41	S 32°07'11.33" W	41.586	41	1,339,888.1423	621,566.3643
16	17	N 83°36'34.30" E	35.418	17	1,340,270.6661	621,866.9511	41	42	S 30°07'24.31" W	20.943	42	1,339,870.0276	621,555.8537
17	18	N 61°28'36.36" E	44.036	18	1,340,291.6838	621,905.6420	42	43	N 64°26'13.94" W	41.851	43	1,339,888.0865	621,518.0989
18	19	N 66°43'44.66" E	30.053	19	1,340,303.5673	621,933.2505	43	44	N 23°80'03.73" E	9.671	44	1,339,897.0124	621,521.8207
19	20	S 22°08'19.07" E	5.015	20	1,340,298.9221	621,935.1404	44	45	N 24°32'31.07" E	9.710	45	1,339,905.8450	621,525.8537
20	21	S 21°51'08.43" E	11.518	21	1,340,288.3320	621,939.4285	45	46	N 64°37'28.10" W	18.052	46	1,339,912.6594	621,511.3110
21	22	S 14°09'11.12" E	5.476	22	1,340,283.9024	621,940.7674	46	47	N 63°58'20.65" W	18.220	47	1,339,920.6342	621,494.9392
22	23	S 09°48'47.14" E	5.070	23	1,340,277.9264	621,941.6315	47	48	N 64°25'40.11" W	7.276	48	1,339,923.7749	621,488.3759
23	24	S 50°41'37.05" W	2.962	24	1,340,276.0502	621,939.3398	48	1	N 68°48'51.75" W	8.205	1	1,339,926.7402	621,480.7253
24	25	S 52°30'23.40" W	3.236	25	1,340,274.0769	621,936.7755							

SUPERFICIE = 32,375.161 m2 = 3.24 Ha = 4.60 Mnz

COORDENADAS NO VINCULADAS AL SISTEMA NACIONAL DE COORDENADAS

CUADRO DE CONSTRUCCION POLIGONO 3

LADO EST	LADO PV	RUMBO	DISTANCIA	V	COORDENADAS Y	COORDENADAS X
				1	1,339,720.1939	621,379.0532
1	2	N 12°04'00.38" E	60.752	2	1,339,779.6037	621,391.7535
2	3	S 79°56'19.36" W	0.596	3	1,339,779.4995	621,391.1666
3	4	N 11°01'36.37" E	16.803	4	1,339,796.0907	621,394.3997
4	5	S 73°19'13.14" E	17.837	5	1,339,790.8423	621,411.0518
5	6	N 21°12'16.45" E	37.680	6	1,339,826.0527	621,425.2035
6	7	N 15°59'03.37" E	3.958	7	1,339,829.8169	621,426.4263
7	8	N 54°45'47.80" W	17.058	8	1,339,839.6586	621,412.4939
8	9	N 34°08'48.22" E	37.922	9	1,339,871.0450	621,433.7803
9	10	N 39°14'55.77" E	5.445	10	1,339,875.2594	621,437.2251
10	11	N 39°34'34.35" E	4.018	11	1,339,878.3565	621,439.7850
11	12	N 58°22'47.28" E	3.650	12	1,339,880.2704	621,442.8630
12	13	N 69°11'15.41" E	3.215	13	1,339,881.4126	621,445.8986
13	14	N 73°48'46.60" E	3.436	14	1,339,882.3704	621,449.1982
14	15	N 80°03'32.40" E	2.108	15	1,339,882.5168	621,451.2992
15	16	N 83°48'54.20" E	3.636	16	1,339,882.9085	621,454.6139
16	17	S 68°32'00.28" E	25.000	17	1,339,873.7598	621,478.1794
17	18	S 68°53'56.17" E	26.550	18	1,339,864.2011	621,502.9485
18	19	S 29°19'40.89" W	5.363	19	1,339,859.5083	621,500.3133
19	20	S 28°07'32.47" W	15.227	20	1,339,846.0793	621,493.1349
20	21	S 25°55'57.99" W	20.873	21	1,339,827.3078	621,484.0066
21	22	S 28°28'28.12" W	7.254	22	1,339,820.7569	621,480.8903
22	23	S 25°24'02.22" W	12.192	23	1,339,809.7436	621,475.6604
23	24	S 23°32'17.90" W	11.365	24	1,339,799.3240	621,471.1217
24	25	S 24°51'39.56" W	8.011	25	1,339,792.0554	621,467.7538
25	26	S 26°13'00.05" W	13.798	26	1,339,779.6769	621,461.6583
26	27	S 25°02'18.18" W	26.410	27	1,339,755.7418	621,450.4849
27	28	S 23°29'31.62" W	53.296	28	1,339,706.7408	621,429.5348
28	29	S 17°42'39.67" W	3.525	29	1,339,703.3832	621,428.4625
29	30	N 78°31'10.66" W	42.068	30	1,339,713.9022	621,387.7307
30	31	N 6°56'13.45" W	6.395	31	1,339,716.3045	621,381.8036
31	1	N 35°16'01.30" W	4.764	1	1,339,720.1939	621,379.0532

SUPERFICIE = 10,681.724 m2 = 1.07 Ha = 1.52 Mnz

Área Poligono 1: 206,369.309 m2 = 20.64 Ha = 29.28 Mnz
Área Poligono 2: 32,375.161 m2 = 3.24 Ha = 4.60 Mnz
Área Poligono 3: 10,681.724 m2 = 1.07 Ha = 1.52 Mnz
ÁREA TOTAL: 249,426.194 m2 = 24.94 Ha = 35.38Mnz

Objeto Lev: Verificación de área	Número Catastral: 3052-3-06-000-01101	FIRMA:	SELLO
Propietario: Hugo Leonel Morales Muñoz Ced: 201-070365-0013R	Ubicación: Del Puente el Paso de Panaloya 90m al Norte. Municipio de Granada, Departamento de Granada.	Ejecuta: Ing.Bosco Javier Morgan Lic. Catastral: BMM 100426 Celular: 8883-7568 SERVICIOS TOPOGRAFICOS	
Factor de escala: 1.418415	Área: Indicada — Escala: 1/4,000	Fecha: 30 de Enero del 2026	