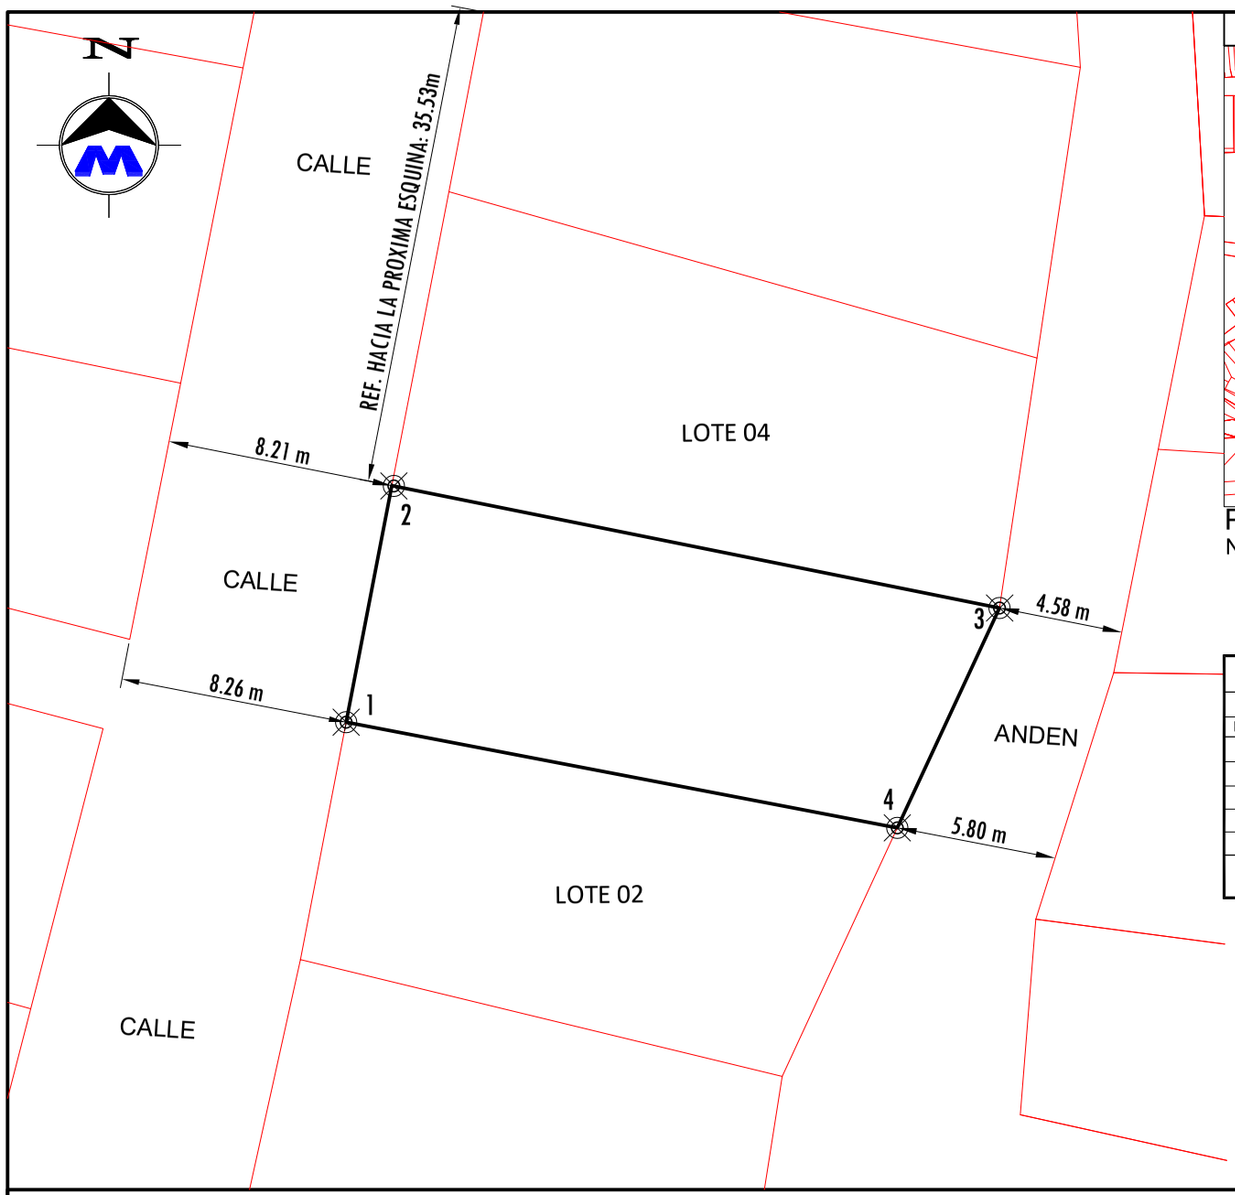

DEPARTAMENTO DE GRANADA MUNICIPIO DE GRANADA

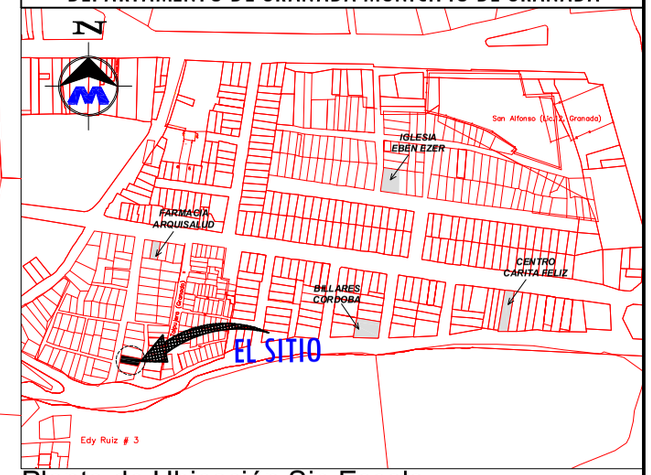

Planta de Ubicación Sin Escala
Número Catastral: 6311-4867-5062-17

COORDENADAS NO VINCULADAS A LA RED GEODESICA DE NICARAGUA

CUADRO DE CONSTRUCCION

LADO EST	LADO PV	RUMBO	DISTANCIA	V	COORDENADAS Y	COORDENADAS X
				1	1,318,706.8150	614,650.0590
1	2	N 10°55'37.22" E	8.714	2	1,318,715.3714	614,651.7109
2	3	S 78°36'53.15" E	22.371	3	1,318,710.9553	614,673.6417
3	4	S 24°44'12.53" W	8.760	4	1,318,702.9990	614,669.9760
4	1	N 79°09'13.86" W	20.279	1	1,318,706.8150	614,650.0590

SUPERFICIE = 183.70 m2 =260.56 Vrs2

Objeto Lev: Venta Total	Número Catastral: 6311-4867-5062-17		FIRMA:
Enajenante: Nelson Roque Calderon Avendaño; Ced: 449-210268-0004C	Ubicación: San Juan del Sur, lote 3, manzana 3. Municipio de Granada, Departamento de Granada.		Ejecuta: Ing.Bosco Javier Morgan Lic. Catastral: BMM100426 Cel: 8883-7568 Email: ingmorgan73@gmail.com SERVICIOS TOPOGRAFICOS
Adquiriente: Ana Ester Hernandez; Ced: 201-300756-0001D	Área: 183.70 m2 =260.56 Vrs2	Escala: 1 /250	Fecha: 28 de Febrero del 2026

ESPACIO PARA ESQUELA